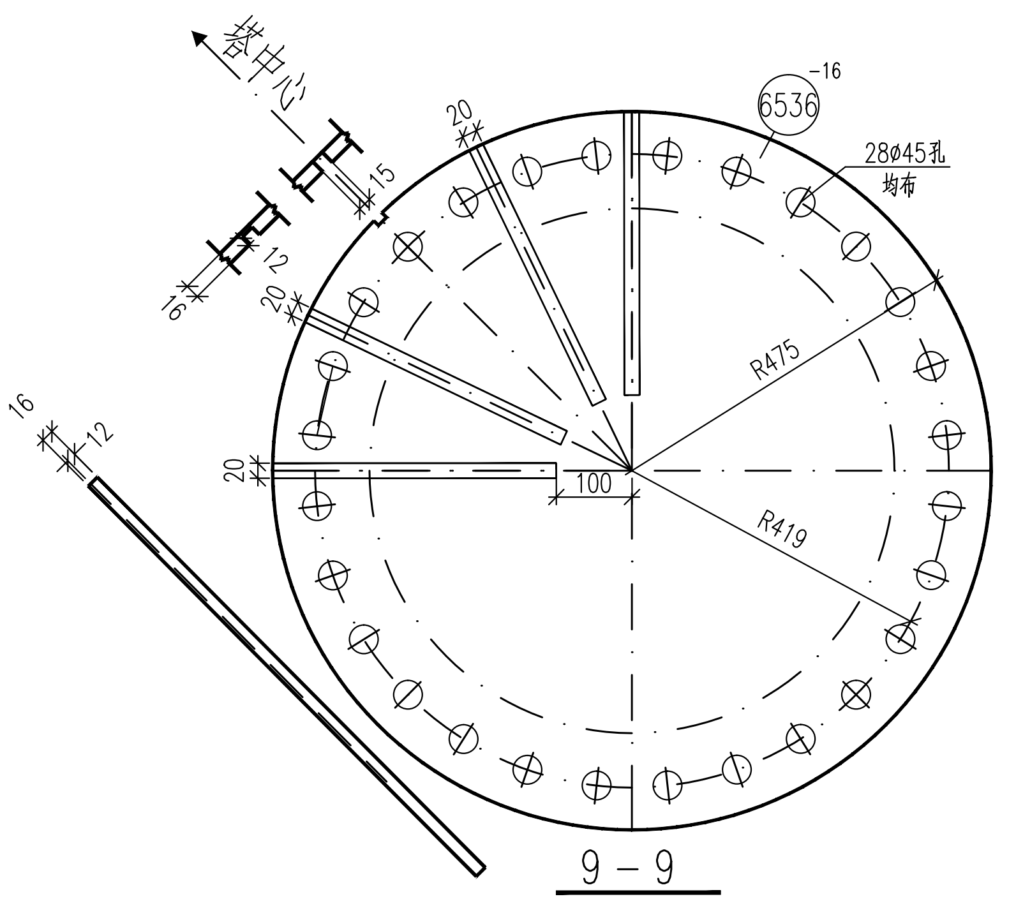

9 - 9
1:20

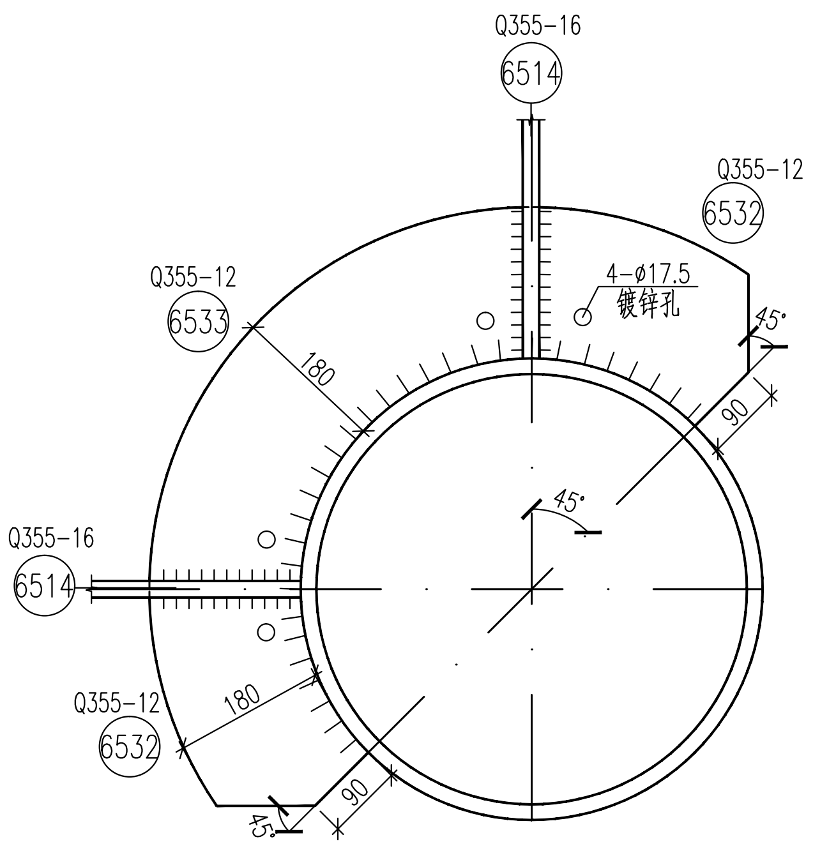

10 - 10
1:20

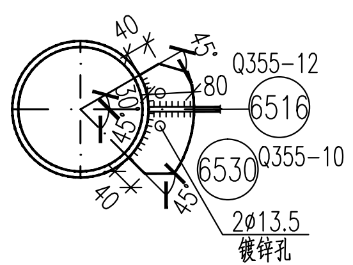

12 - 12
1:10

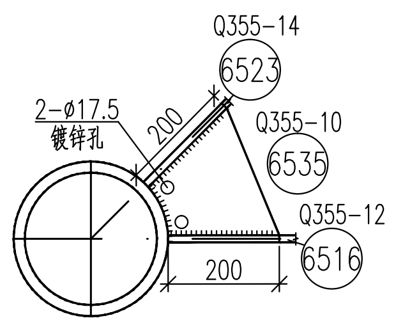

13 - 13
1:10

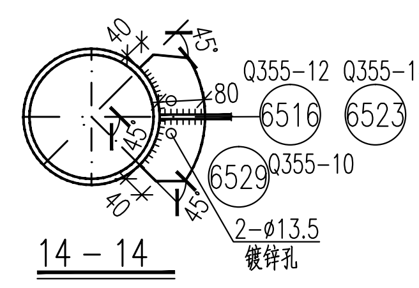

14 - 14
1:10

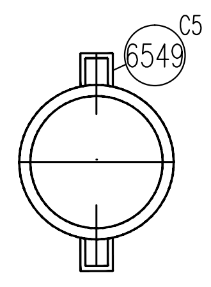

15 - 15
1:10

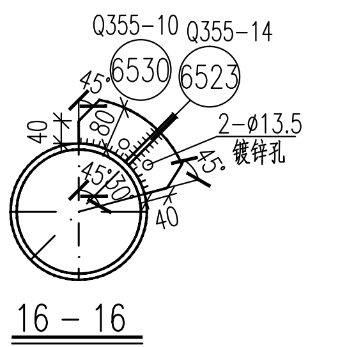

16 - 16
1:10

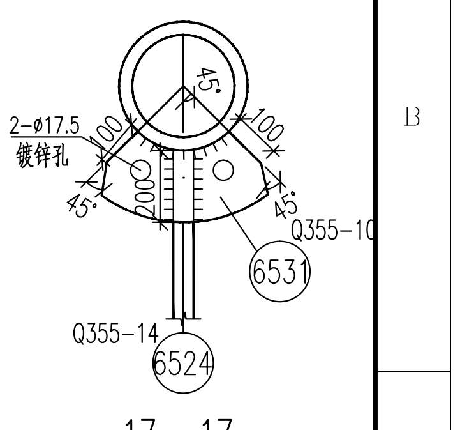

17 - 17
1:10

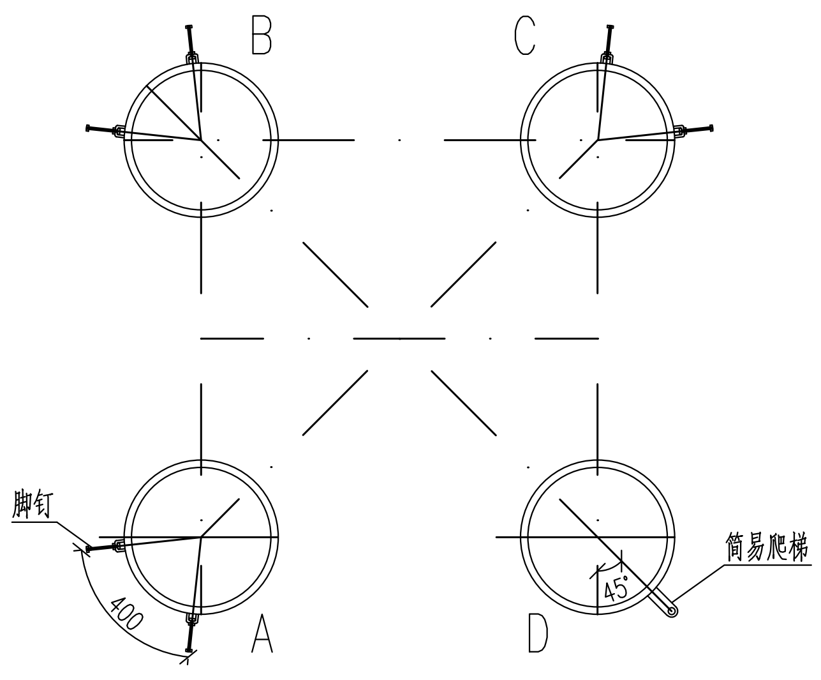

爬梯脚钉示意图

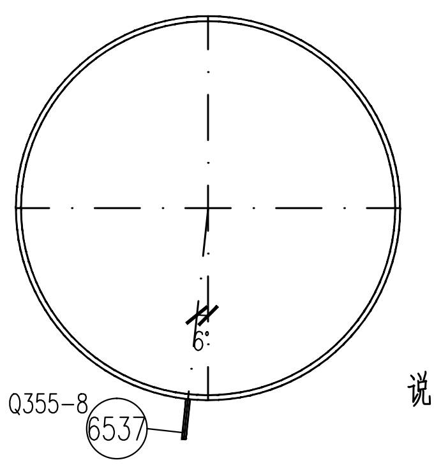

接地孔位置示意图
1:20

说明：接地孔安装板 ⑥⑤③⑦ 避开法兰加劲板和地脚法兰螺栓所在角度,以避免接地引下线和法兰加劲板相碰.

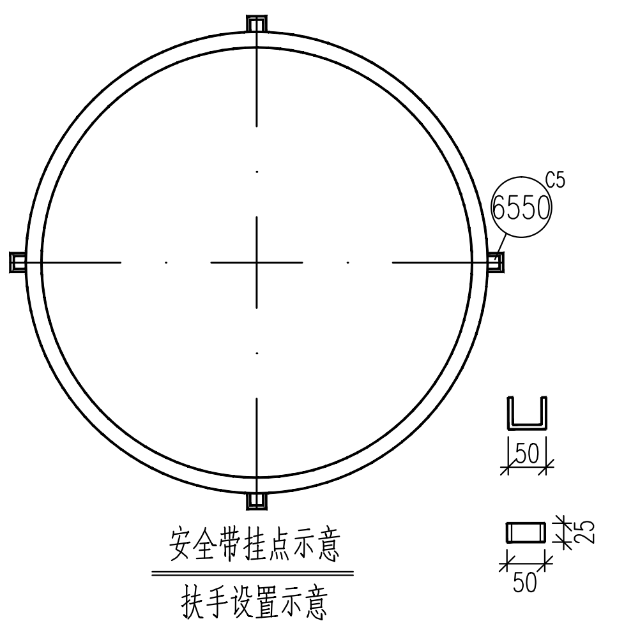

安全带挂点示意
扶手设置示意

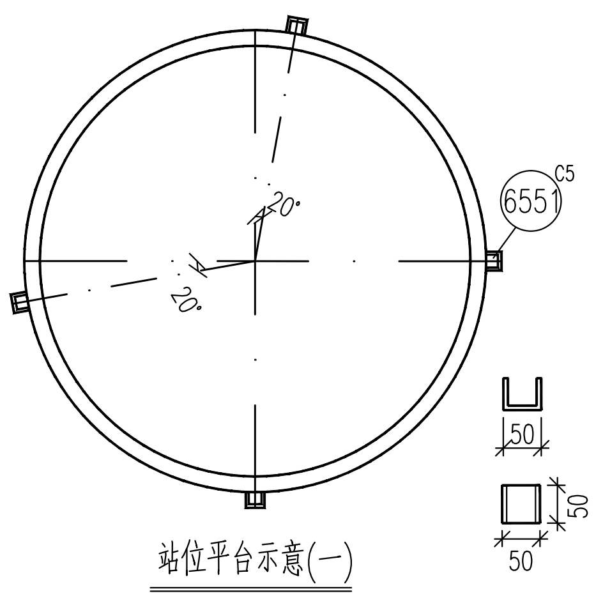

站位平台示意(一)

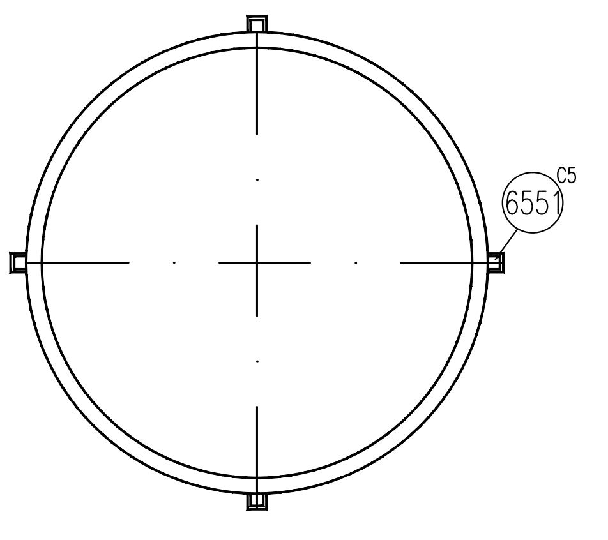

站位平台示意(二)

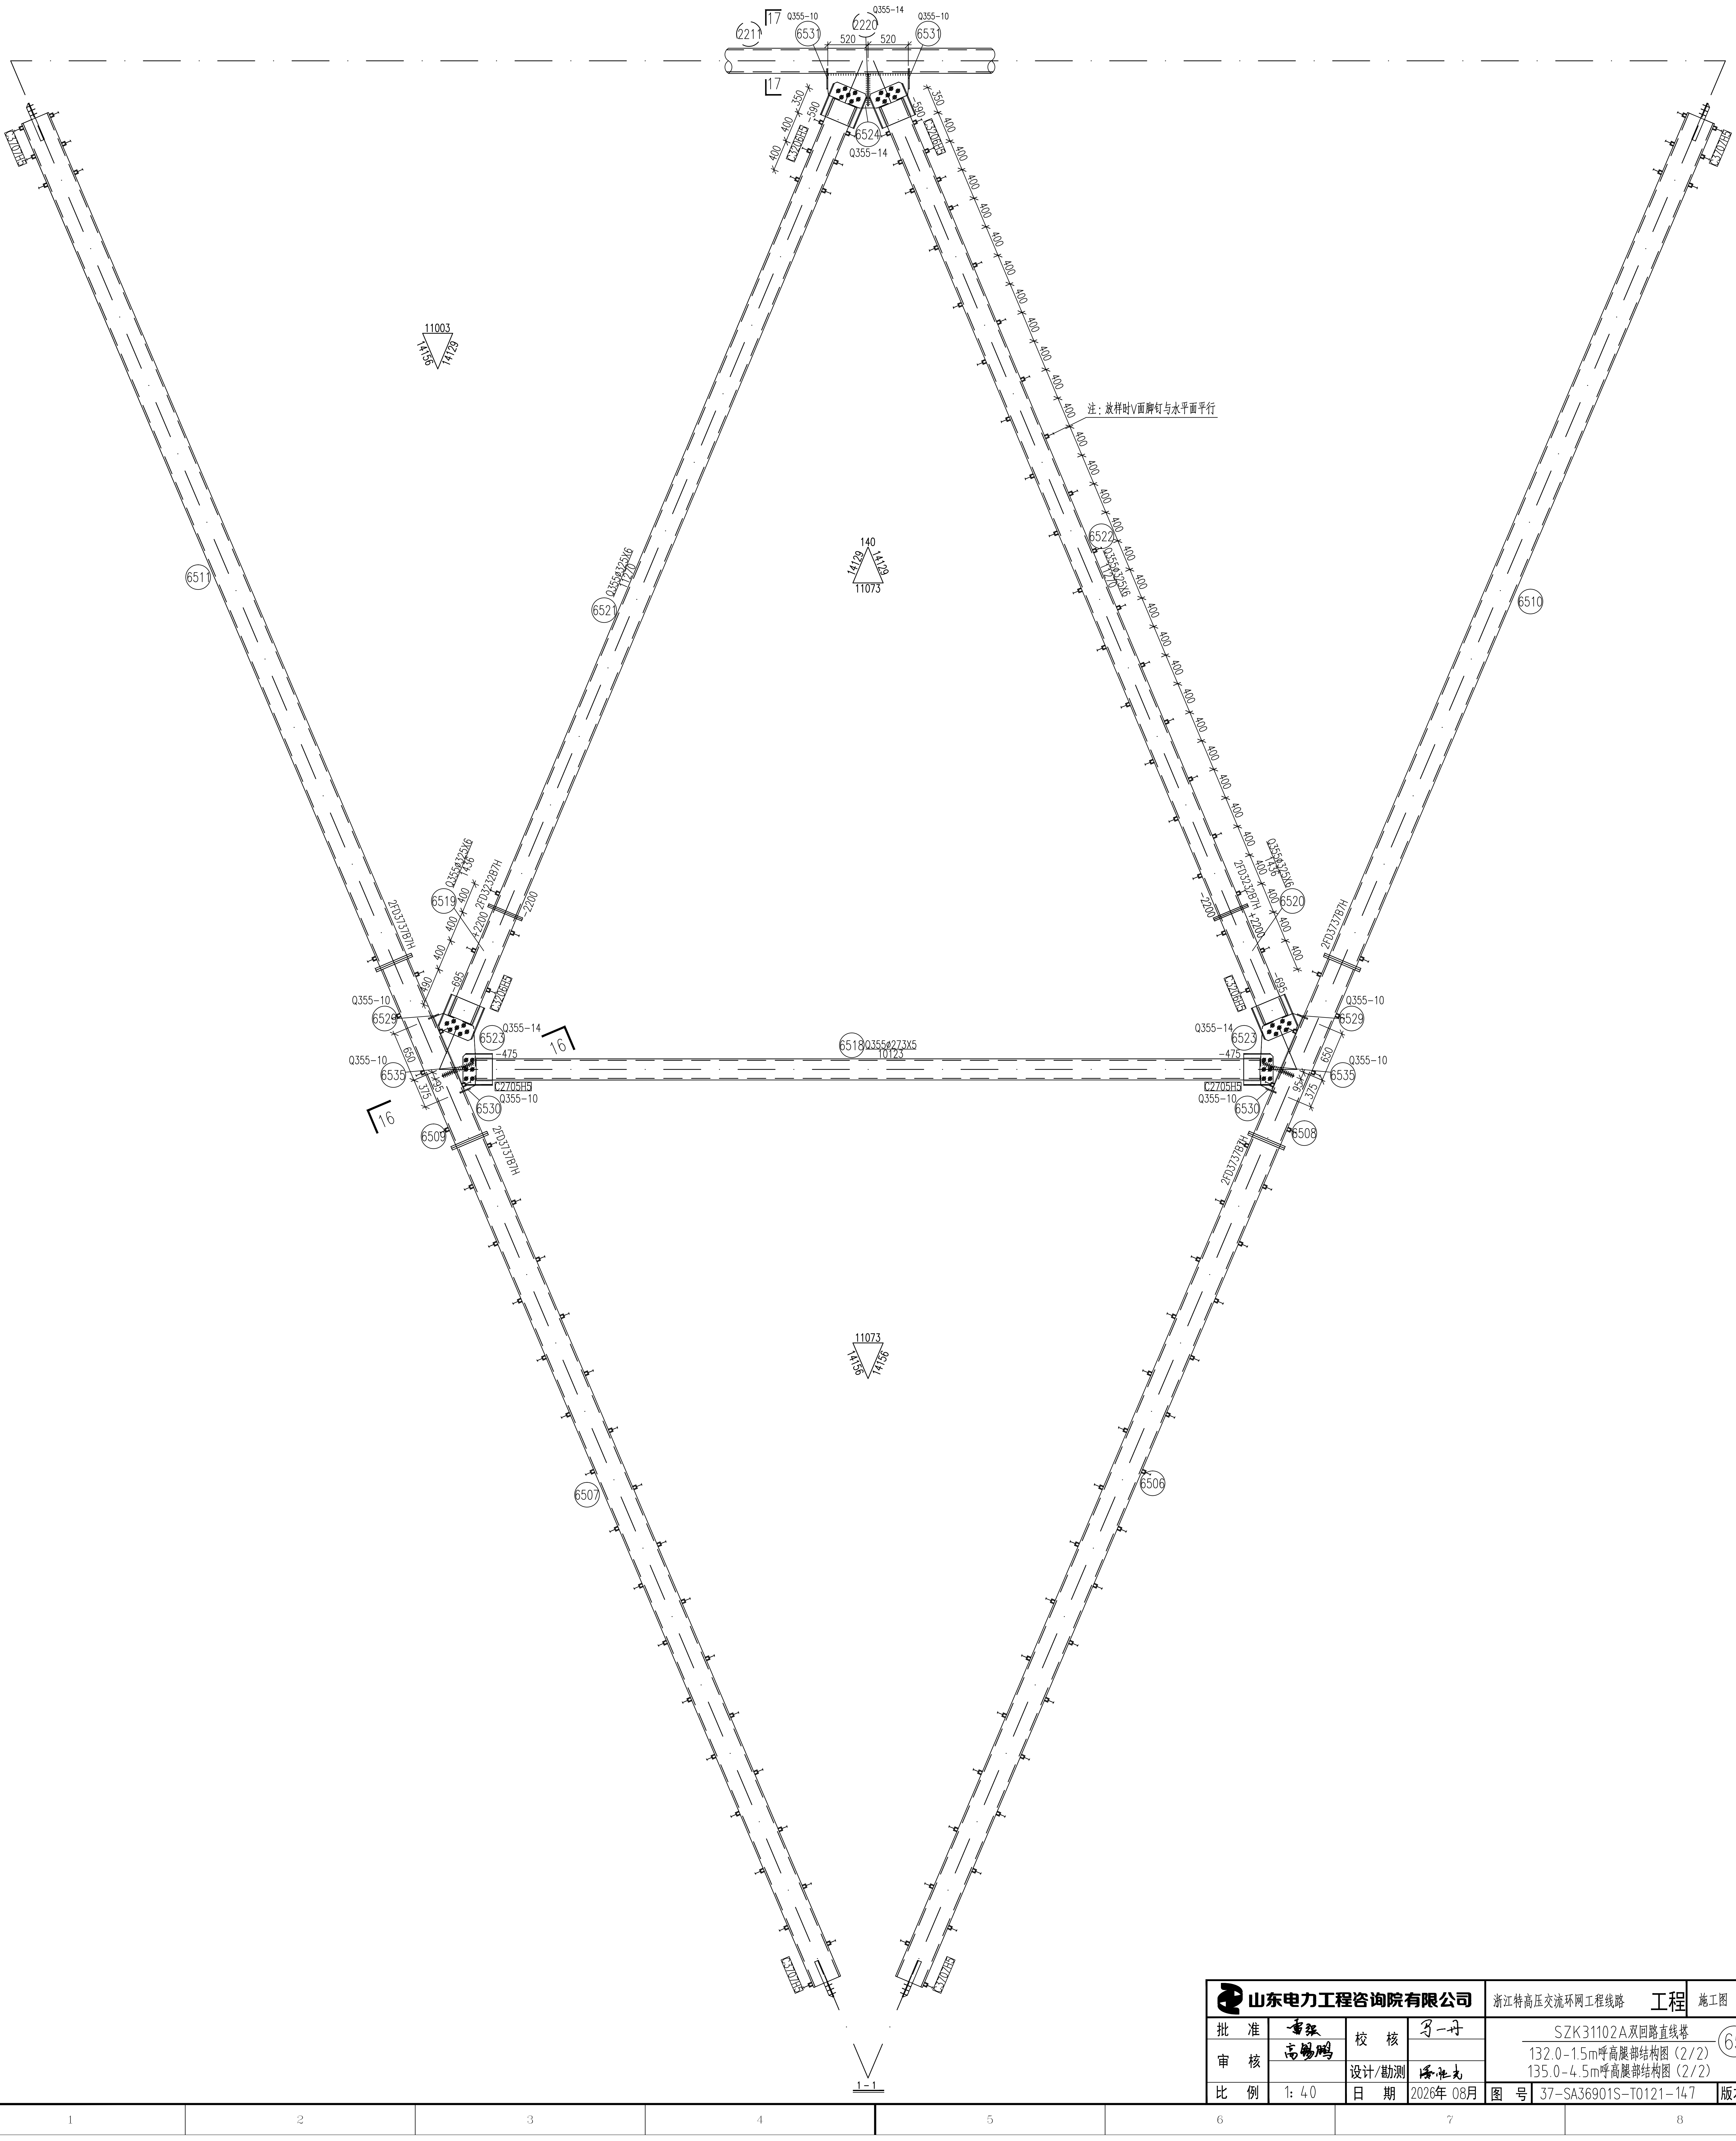

1-1

山东电力工程咨询院有限公司		浙江特高压交流环网工程线路 工程	施工图 设计阶段
批准	雷强	校核	马一丹
审核	高锡鹏		
		设计/勘测	潘旺克
比例	1:40	日期	2026年 08月

SZK31102A双回路直线塔 ⑥⑤
132.0-1.5m呼高腿部结构图（2/2）
135.0-4.5m呼高腿部结构图（2/2）

图号 37-SA36901S-T0121-147 版本