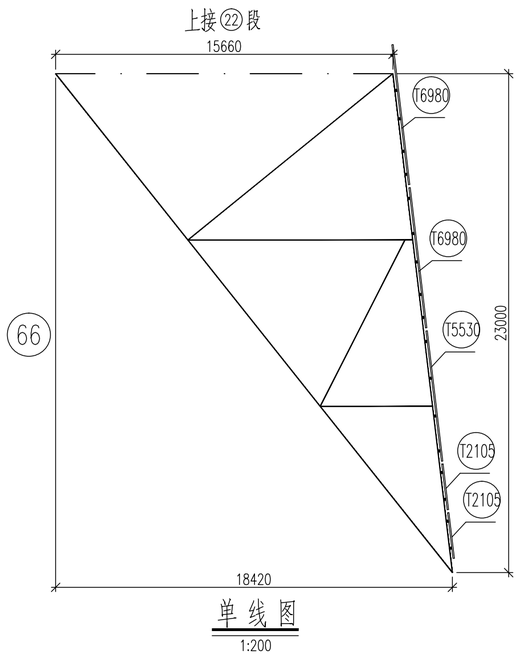

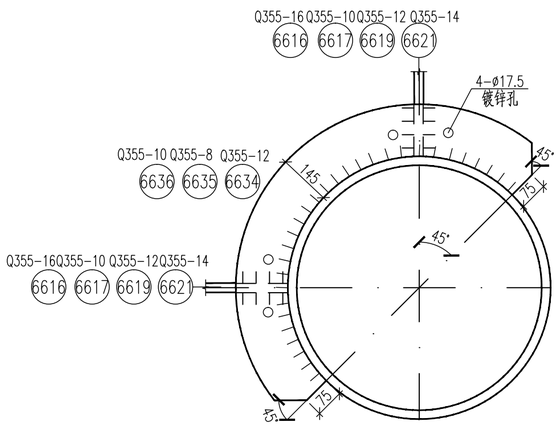

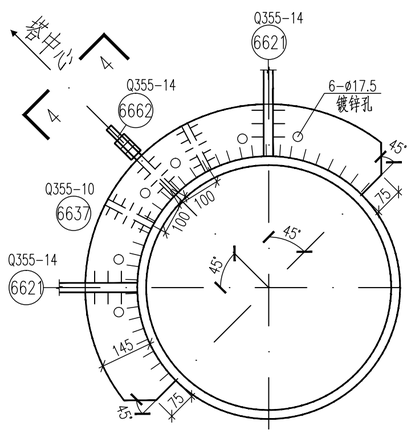

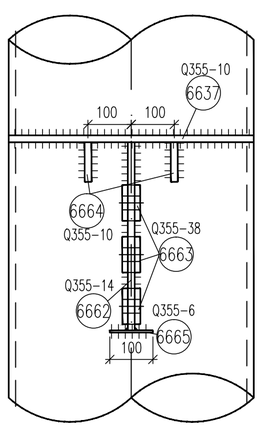

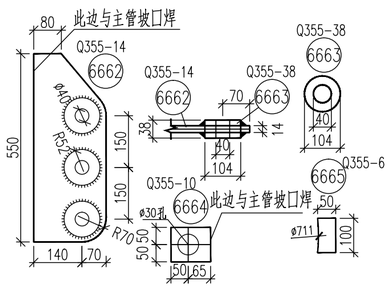

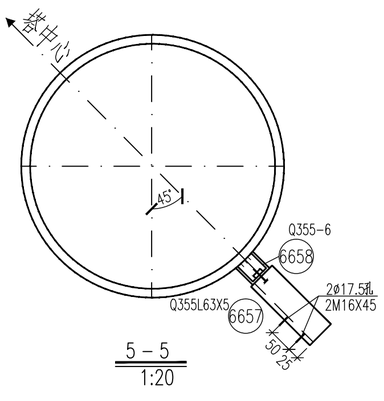

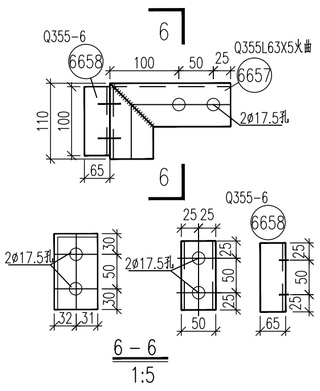

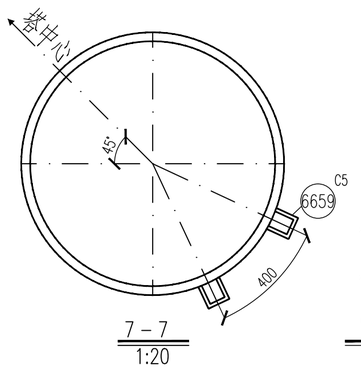

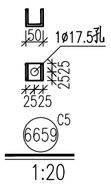

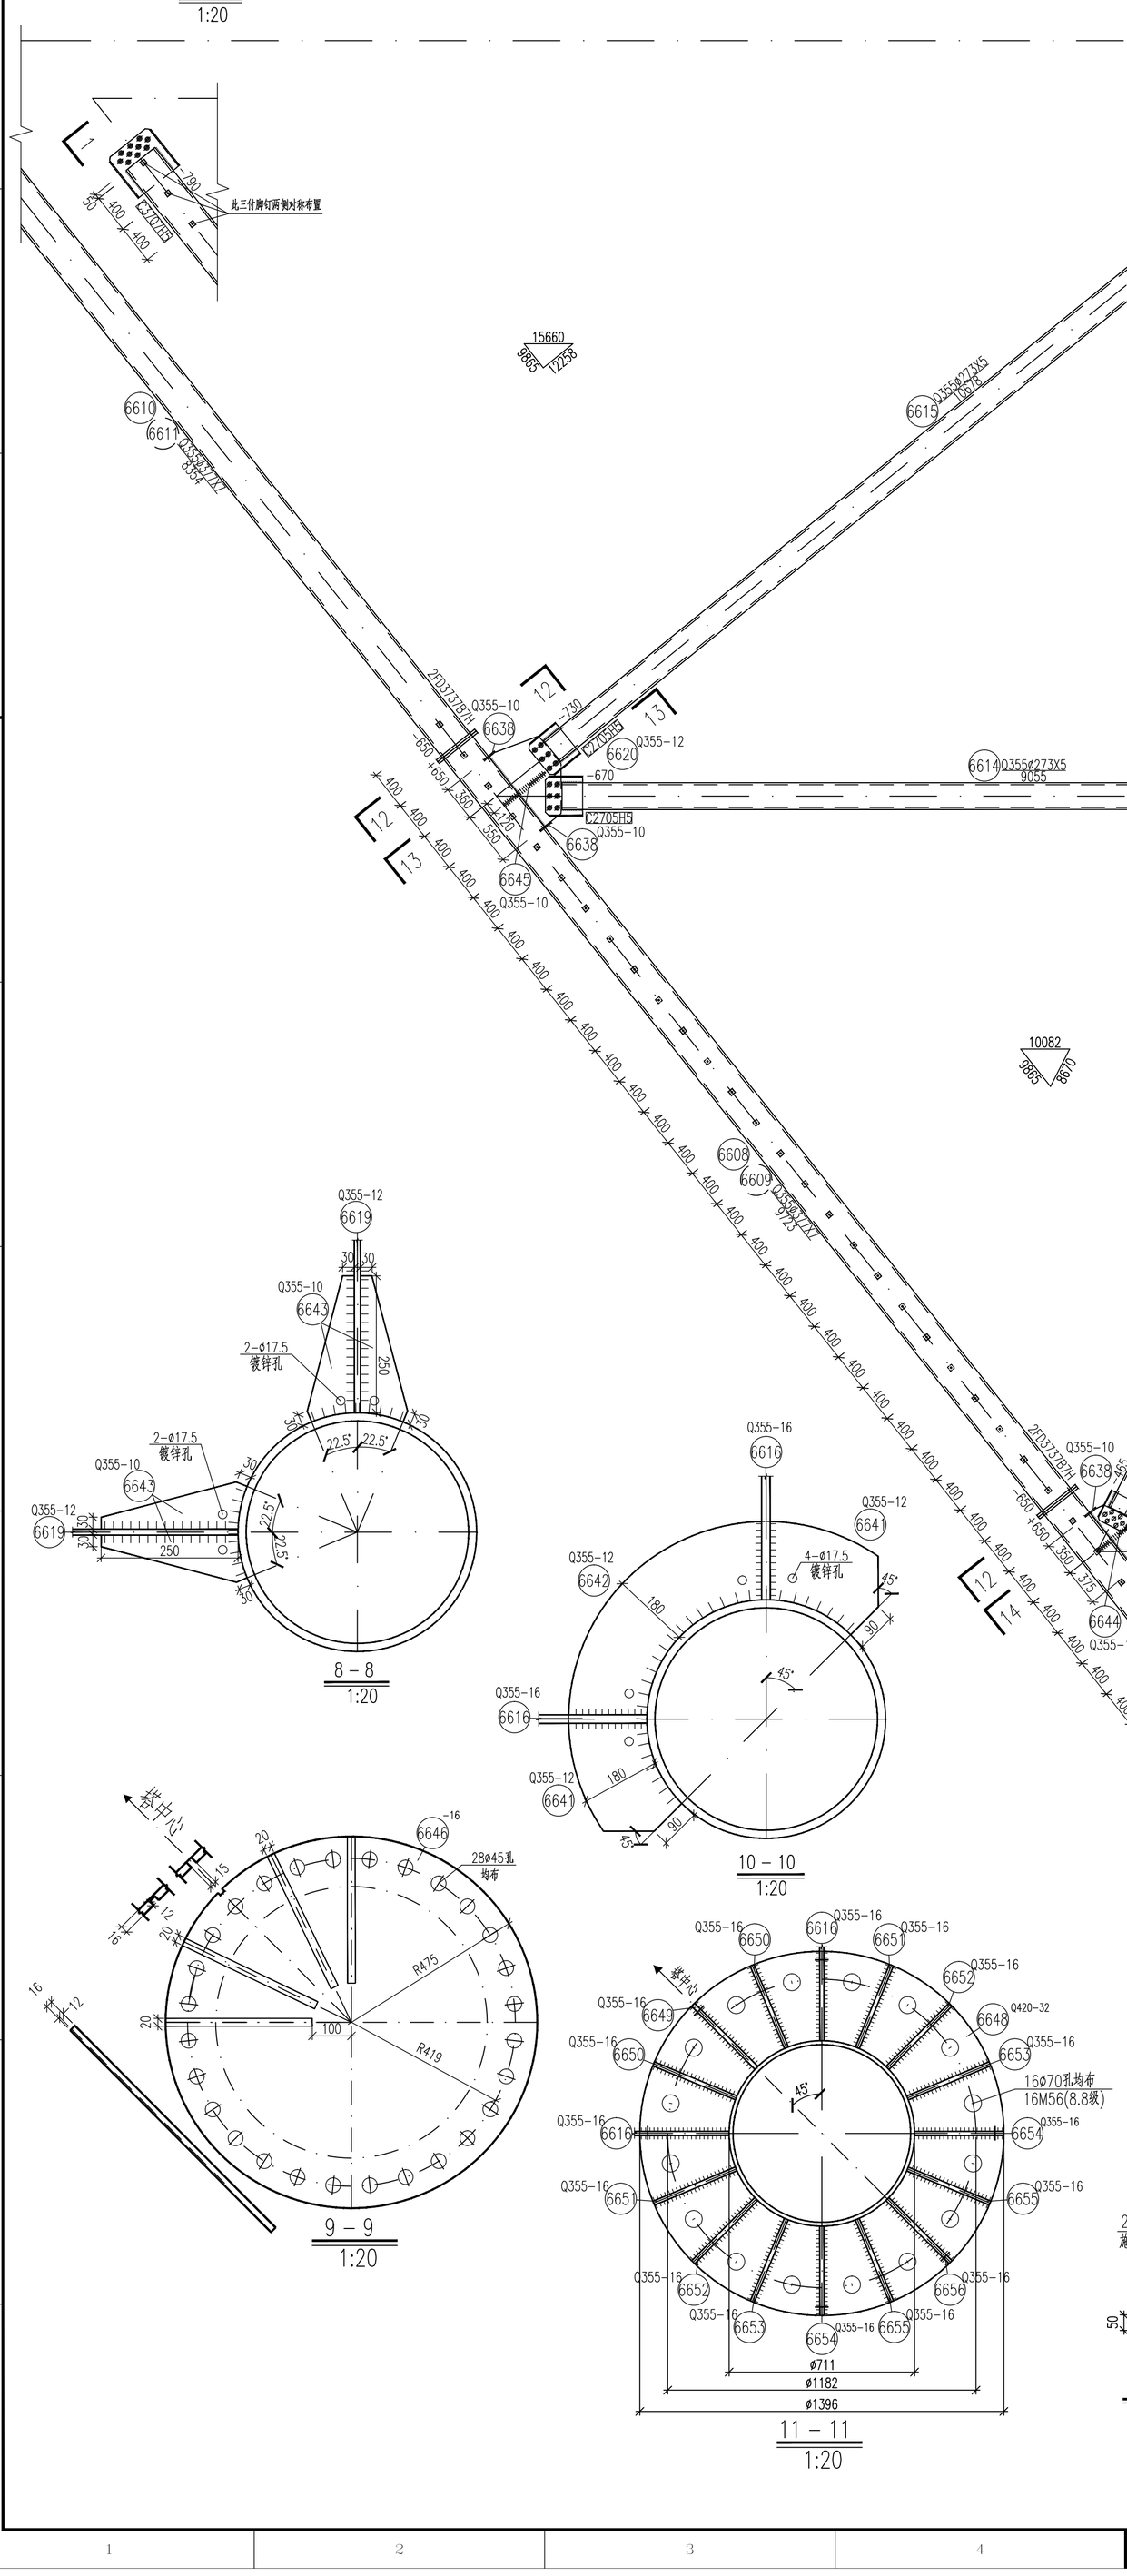

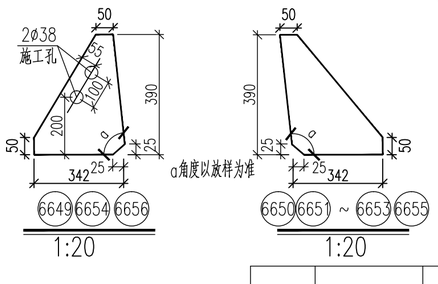

上接㉒段
66
15660
18420
23000
T6980
T5530
T2105
单线图
1:200
2－2
1:20
3－3
1:20
4－4
1:20
5－5
1:20
6－6
1:5
7－7
1:20
8－8
1:20
9－9
1:20
10－10
1:20
11－11
1:20
1:20
塔中心
此边与主管坡口焊
此三付脚钉两侧对称布置
4-ø17.5
镀锌孔
6-ø17.5
2-ø17.5
16ø70孔均布
16M56(8.8级)
28ø45孔均布
2ø38
施工孔
角度以放样为准
接地孔
ø711
ø1182
ø1396

构件明细表

编号	规格	长度 (mm)	数量	重量(kg) 一件	重量(kg) 小计	备注
6601	Q420ø711X15	2234	1	575.18	575.2	一端切弧 装爬梯
6601A	Q420ø711X15	2234	0	575.18	0.0	一端切弧 带脚钉
6602	Q420ø711X15	11489	1	2958.03	2958.0	装爬梯
6603	Q420ø711X15	11489	0	2958.03	0.0	带脚钉
6604	Q420ø711X15	9828	1	2530.38	2530.4	装爬梯
6605	Q420ø711X15	9828	0	2530.38	0.0	带脚钉
6606	Q355ø377X7	9029	1	576.71	576.7	带脚钉
6607	Q355ø377X7	9029	1	576.71	576.7	带脚钉
6608	Q355ø377X7	9723	1	621.04	621.0	带脚钉
6609	Q355ø377X7	9723	1	621.04	621.0	带脚钉
6610	Q355ø377X7	8354	1	533.60	533.6	带脚钉
6611	Q355ø377X7	8354	1	533.60	533.6	带脚钉
6612	Q355ø140X4	4215	2	56.55	113.1	
6613	Q355ø203X5	7690	2	187.75	375.5	带脚钉
6614	Q355ø273X5	9055	2	299.24	598.5	
6615	Q355ø273X5	10678	2	352.87	705.7	带脚钉
6616	Q355-16X673	1557	2	131.61	263.2	
6617	Q355-10X199	396	2	6.19	12.4	
6618	Q355-10X319	798	2	19.98	40.0	
6619	Q355-12X432	908	2	36.95	73.9	
6620	Q355-12X585	1001	2	55.16	110.3	
6621	Q355-14X495	1139	2	61.96	123.9	
6622	Q355ø180X5	6292	1	135.77	135.8	
6623	Q355ø219X5	4668	1	123.18	123.2	带脚钉
6624	Q355ø219X5	8338	1	220.02	220.0	带脚钉
6625	Q355ø219X5	3810	1	100.54	100.5	带脚钉
6626	Q355ø219X5	8480	1	223.77	223.8	带脚钉
6627	Q355ø273X5	10756	1	355.45	355.4	带脚钉
6628	Q355ø273X5	10756	1	355.45	355.4	带脚钉
6629	Q355-12X457	798	2	34.35	68.7	
6630	Q355-10X610	440	1	21.07	21.1	
6631	Q355-10X250	616	2	12.09	24.2	
6632	Q355-12X434	1001	2	40.92	81.8	
6633	Q355-12X397	1100	1	41.14	41.1	
6634	Q355-12X145	1480	1	20.22	20.2	
6635	Q355-8X145	1480	4	13.48	53.9	
6636	Q355-10X145	1480	1	16.85	16.8	
6637	Q355-10X145	1480	1	16.85	16.8	
6638	Q355-10X80	593	8	3.72	29.8	
6639	Q355-8X60	482	4	1.82	7.3	
6640	Q355-10X120	385	2	3.63	7.3	
6641	Q355-12X180	350	2	5.93	11.9	
6642	Q355-12X180	700	1	11.87	11.9	
6643	Q355-10X150	344	4	4.05	16.2	
6644	Q355-10X200	250	2	3.92	7.8	
6645	Q355-10X300	293	2	6.90	13.8	
6646	-16X950	950	1	89.03	89.0	遮水板
6647	Q355-8X80	110	1	0.55	0.6	接地孔用
6648	Q420-32X1396	1396	1	284.75	284.8	
6649	Q355-16X342	390	1	16.75	16.8	
6650	Q355-16X342	390	2	16.75	33.5	
6651	Q355-16X342	390	2	16.75	33.5	
6652	Q355-16X342	390	2	16.75	33.5	
6653	Q355-16X342	390	2	16.75	33.5	
6654	Q355-16X342	390	2	16.75	33.5	
6655	Q355-16X342	390	2	16.75	33.5	
6656	Q355-16X342	390	1	16.75	16.8	
6657	Q355L63X5	285	17	1.37	23.3	火曲 (用于主材装爬梯)
6658	Q355-6X100	180	17	0.85	14.4	火曲 (用于主材装爬梯)
6659	C5	50	219	0.27	59.1	槽钢 (用于主材装爬梯)
6659	C5	50	276	0.27	74.5	槽钢 (用于主材带脚钉)
6660	C5	25	12	0.14	1.7	槽钢
6661	C5	50	8	0.27	2.2	槽钢
6662	Q355-14X210	550	1	12.69	12.7	
6663	Q355-38X104	104	3	3.23	9.7	
6664	Q355-10X100	115	2	0.90	1.8	
6665	Q355-6X50	100	1	0.24	0.2	
6666	Q355-12X100	383	2	3.61	7.2	
	C1404H5		4	4.80	19.2	
	C1805H5		2	7.12	14.2	
	C2005H5		4	9.74	39.0	
	C2105H5		4	14.54	58.2	
	C2705H5		12	18.10	217.2	
	X2105H7		2	22.90	45.8	
	C3707H5		4	39.39	157.6	
	FD2121B7H		2	9.20	18.4	
	FD3737B7H		8	21.70	173.6	
	FD7171B7D		5	142.30	711.5	
	T2105		2	11.50	23.0	(用于主材装爬梯)
	T5530		1	28.80	28.8	(用于主材装爬梯)
	T6980		2	36.20	72.4	(用于主材装爬梯)
合计	16081.1 kg(用于主材带脚钉)					
合计	16227.6 kg(用于主材装爬梯)					

螺栓、脚钉、垫圈明细表

名称	级别	规格	符号	数量	重量(kg)	备注
螺栓	6.8级	M16X45	◎	68	11.5	用于主材装爬梯
		M20X65	∅	56	19.8	
		M20X75	⊗	32	12.1	
	8.8级	M24X75	∅	132	78.2	
		M20X90	○	14	6.6	法兰螺栓
		M24X110	○	88	72.4	法兰螺栓
		M42X190	○	56	250.7	法兰螺栓
		M42X205	○	28	131.5	法兰螺栓 无扣长101mm
脚钉	6.8级	M16X200	⊖	219	96.0	用于主材装爬梯
		M16X200	⊥	276	121.0	用于主材带脚钉
垫圈	Q235		规格X个数			
合计			692.3 kg		(用于主材带脚钉)	
合计			678.8 kg		(用于主材装爬梯)	

说明：1.材料表为一个塔腿的重量。

2.本段塔腿为铁塔D腿，安装爬梯，当为A、B、C腿时需焊接脚钉连接槽钢。

山东电力工程咨询院有限公司

浙江特高压交流环网工程线路 工程
施工图 设计阶段

SZK31102A双回路直线塔
132.0-0.0m呼高腿部结构图（1/2）
135.0-3.0m呼高腿部结构图（1/2）
66

批准		校核	马一丹		
审核	高锡鹏	设计/勘测			
比例	1: 40	日期	2026年 08月	图号	37-SA36901S-T0121-148
				版本	

电气	赵庆周	2026.08
专业	会签	日期