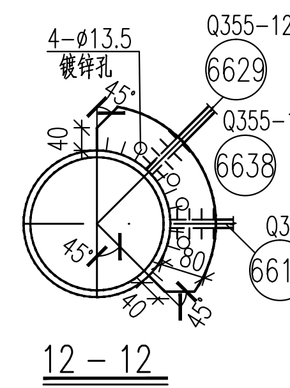

12-12
1:20

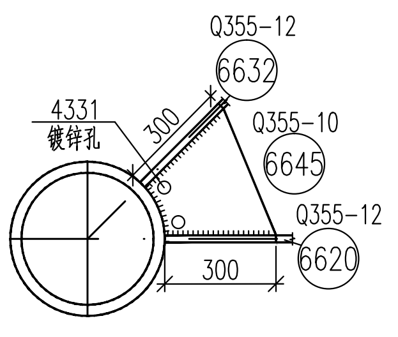

13-13
1:10

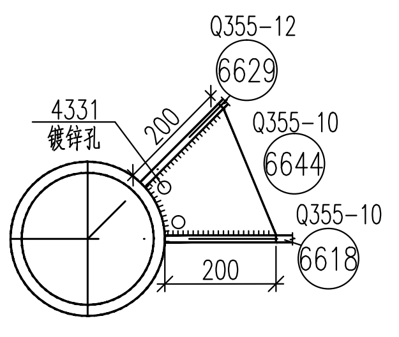

14-14
1:10

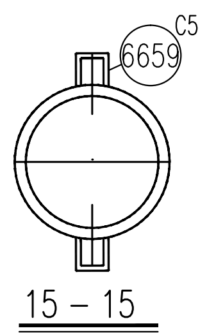

15-15
1:10

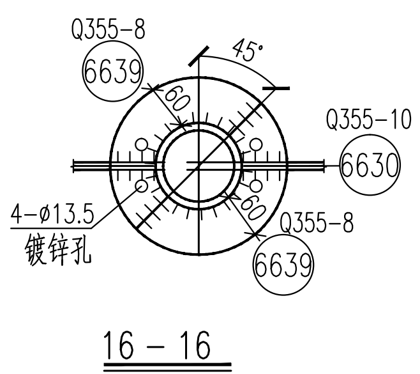

16-16
1:10

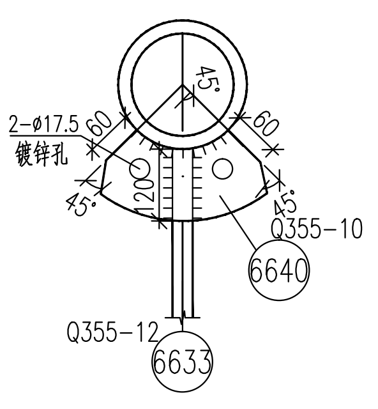

17-17
1:10

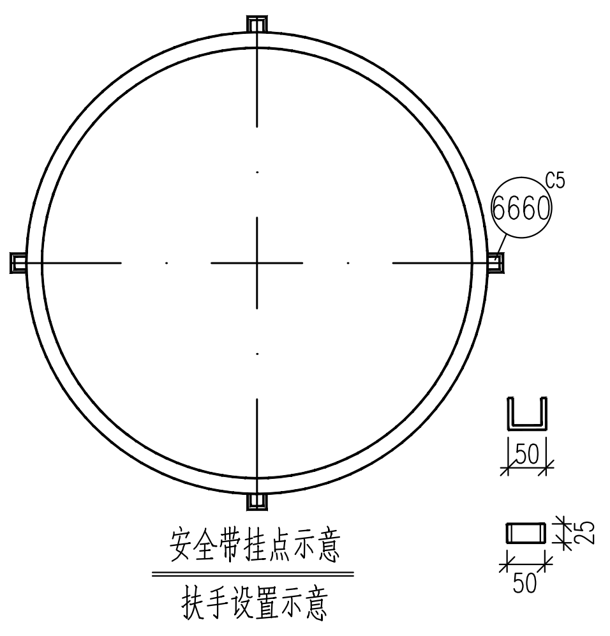

安全带挂点示意
扶手设置示意

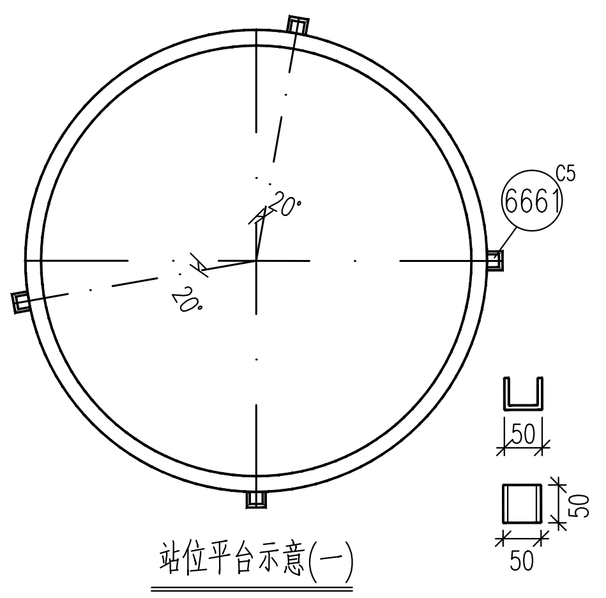

站位平台示意(一)

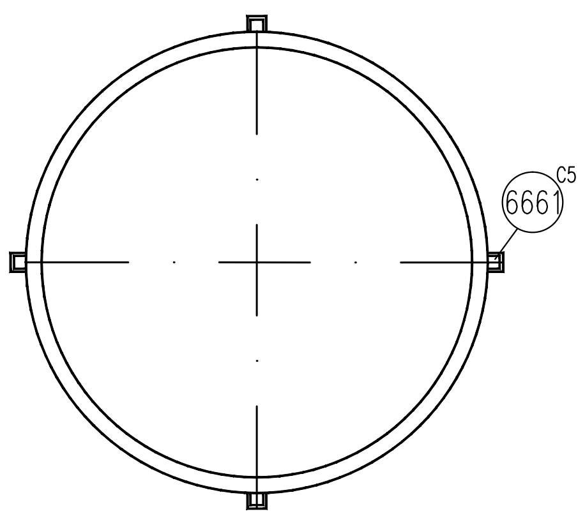

站位平台示意(二)

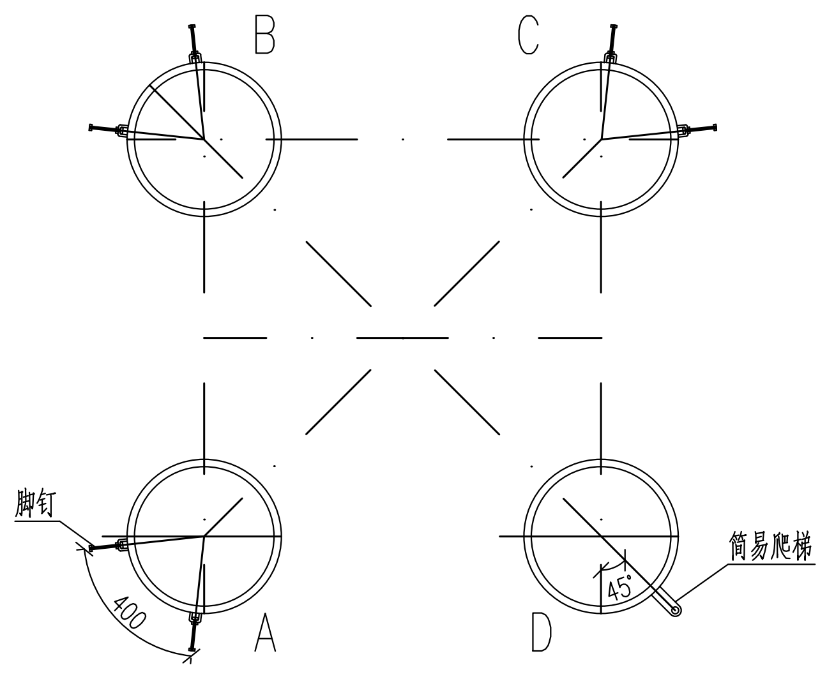

爬梯脚钉示意图

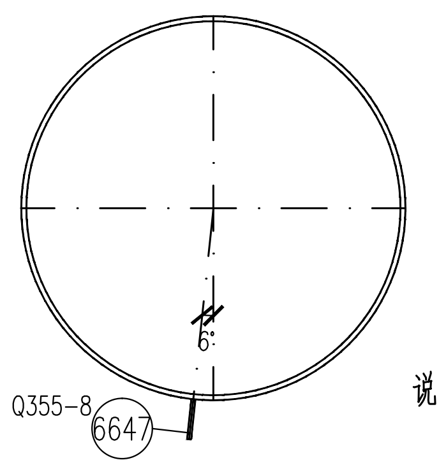

接地孔位置示意图
1:20

说明：接地孔安装板⑥⑥④⑦避开法兰加劲板和地脚法兰螺栓所在角度,以避免接地引下线和法兰加劲板相碰.

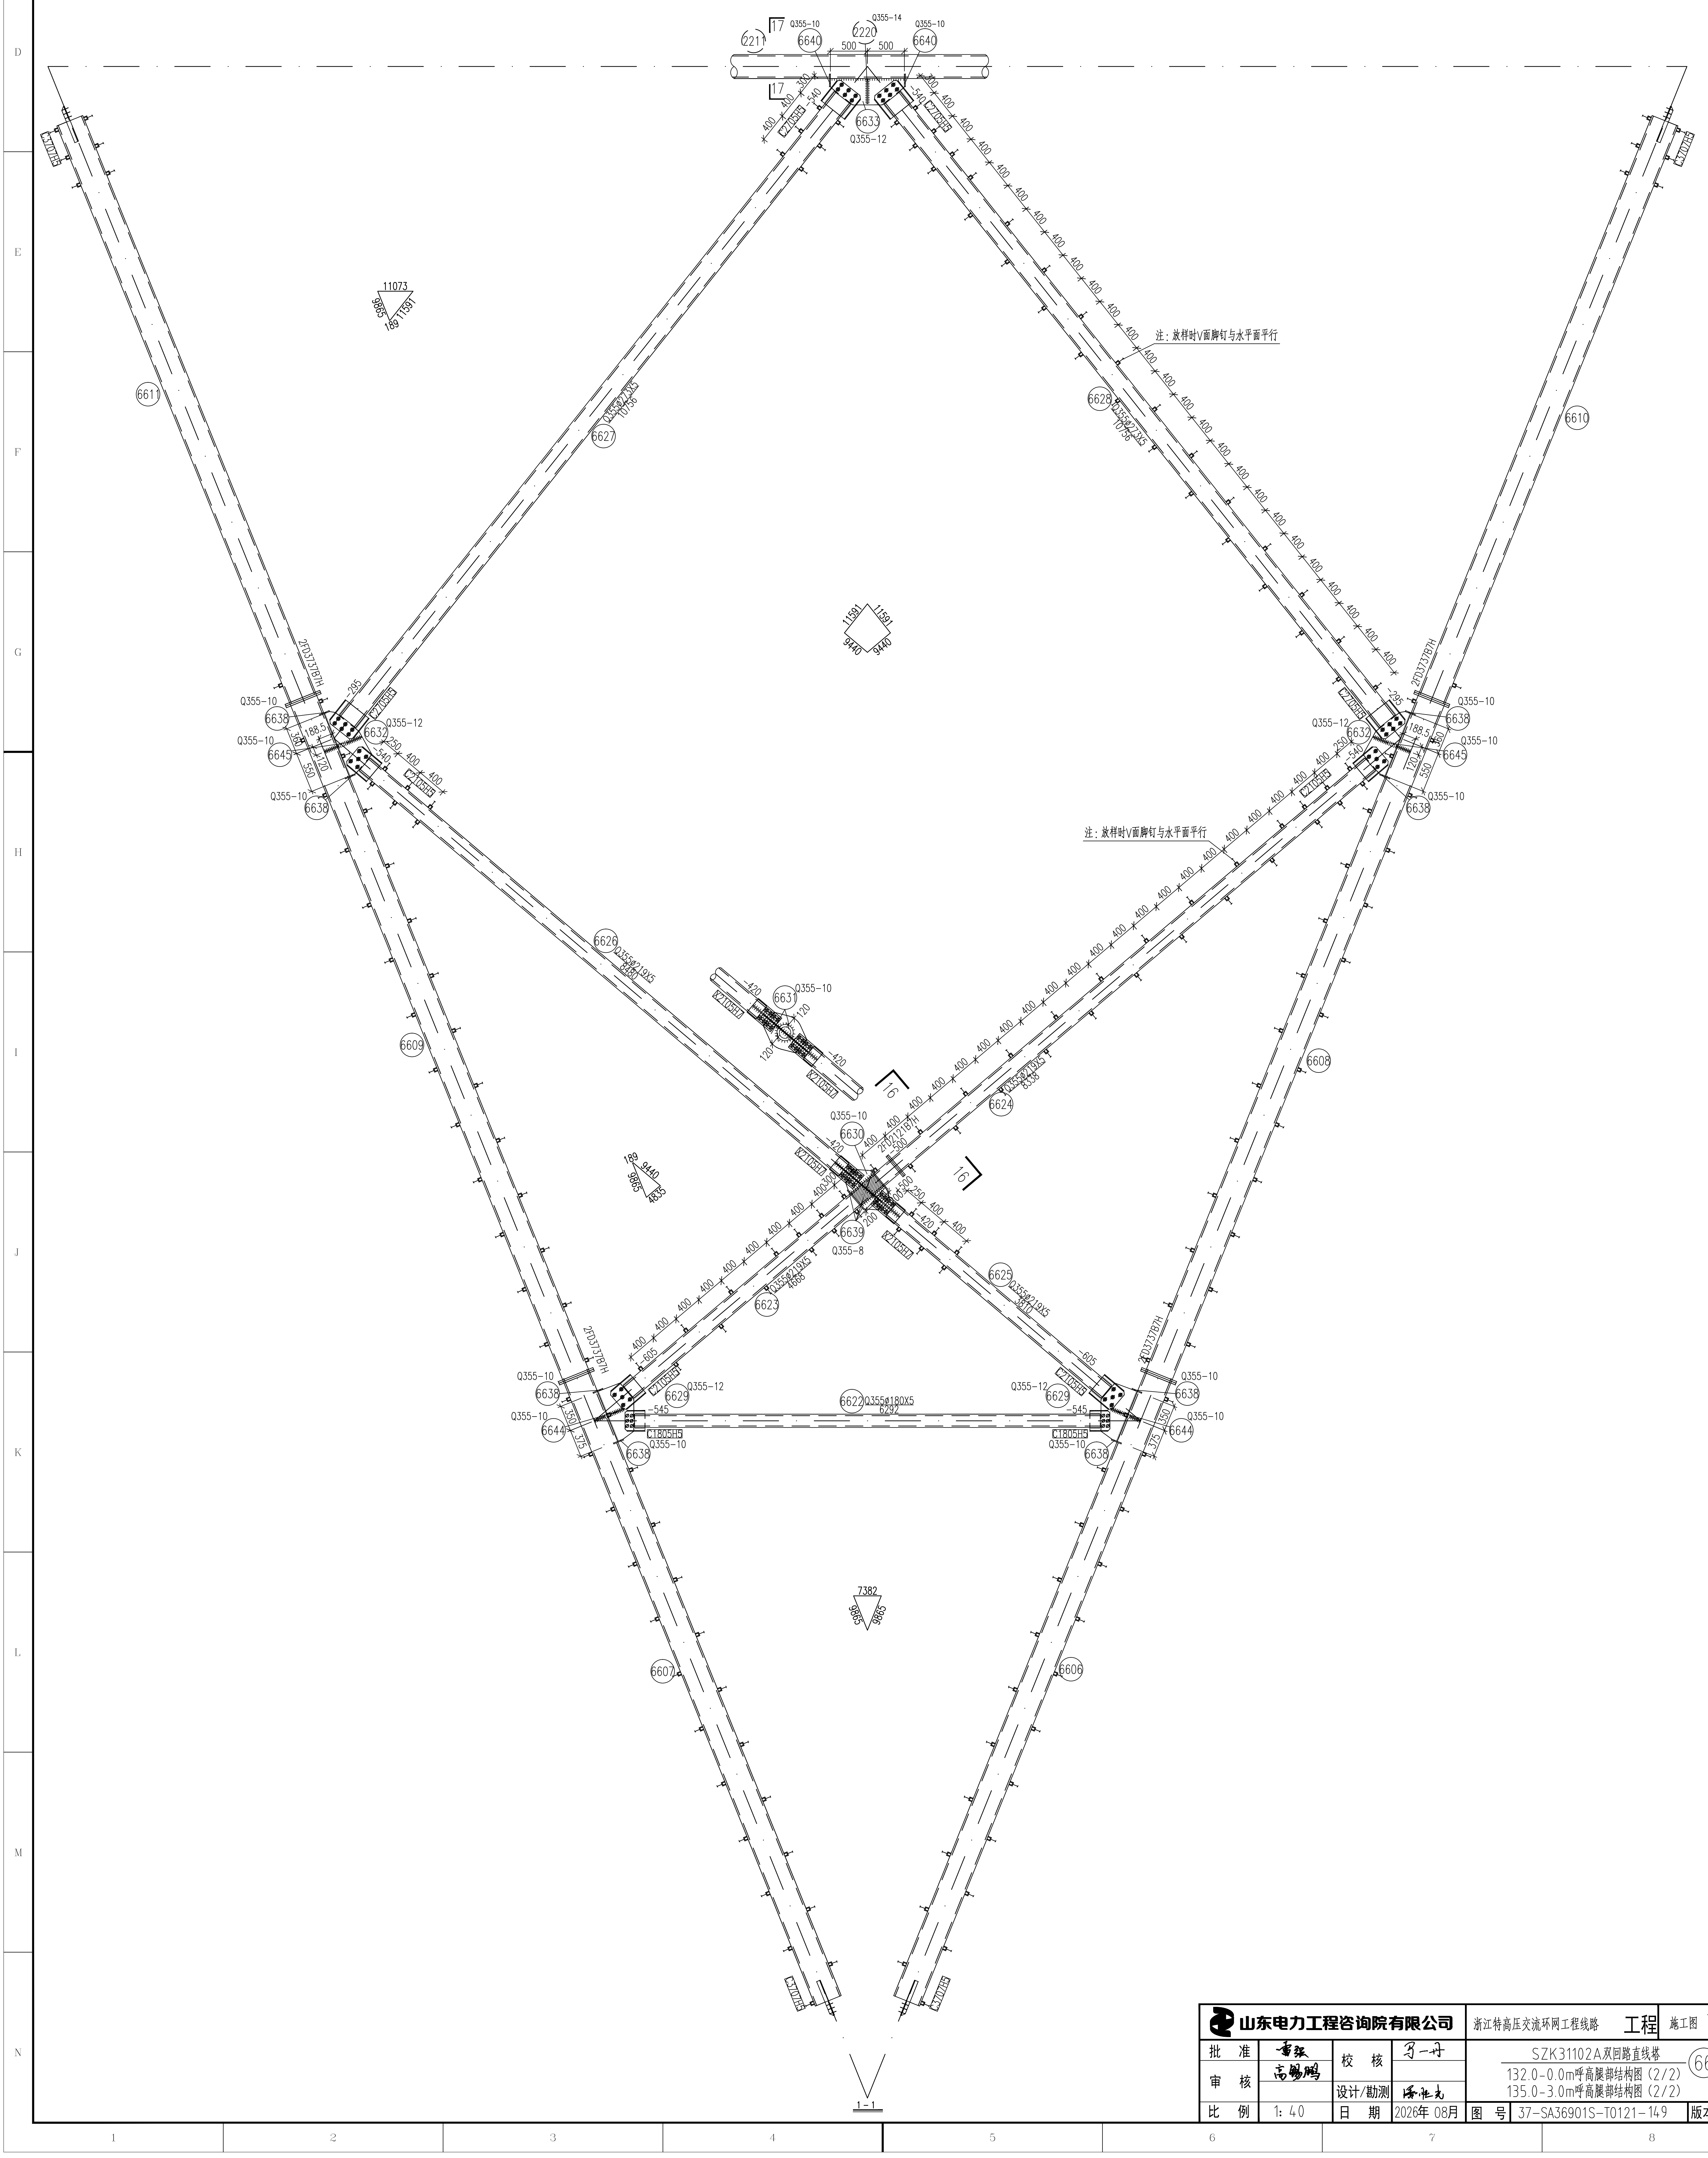

1-1

山东电力工程咨询院有限公司		浙江特高压交流环网工程线路 工程	施工图	设计阶段
批　准	雷张	校　核	马一丹	SZK31102A双回路直线塔 ⑥⑥ 132.0-0.0m呼高腿部结构图（2/2） 135.0-3.0m呼高腿部结构图（2/2）
审　核	高锡鹏	设计/勘测	潘胜光	
比　例	1：40	日　期	2026年 08月	图　号 37-SA36901S-T0121-149 版本