单线图
1:200


2 – 2
1:20

3 – 3
1:20

4 – 4
1:20

7 – 7
1:20

1:20

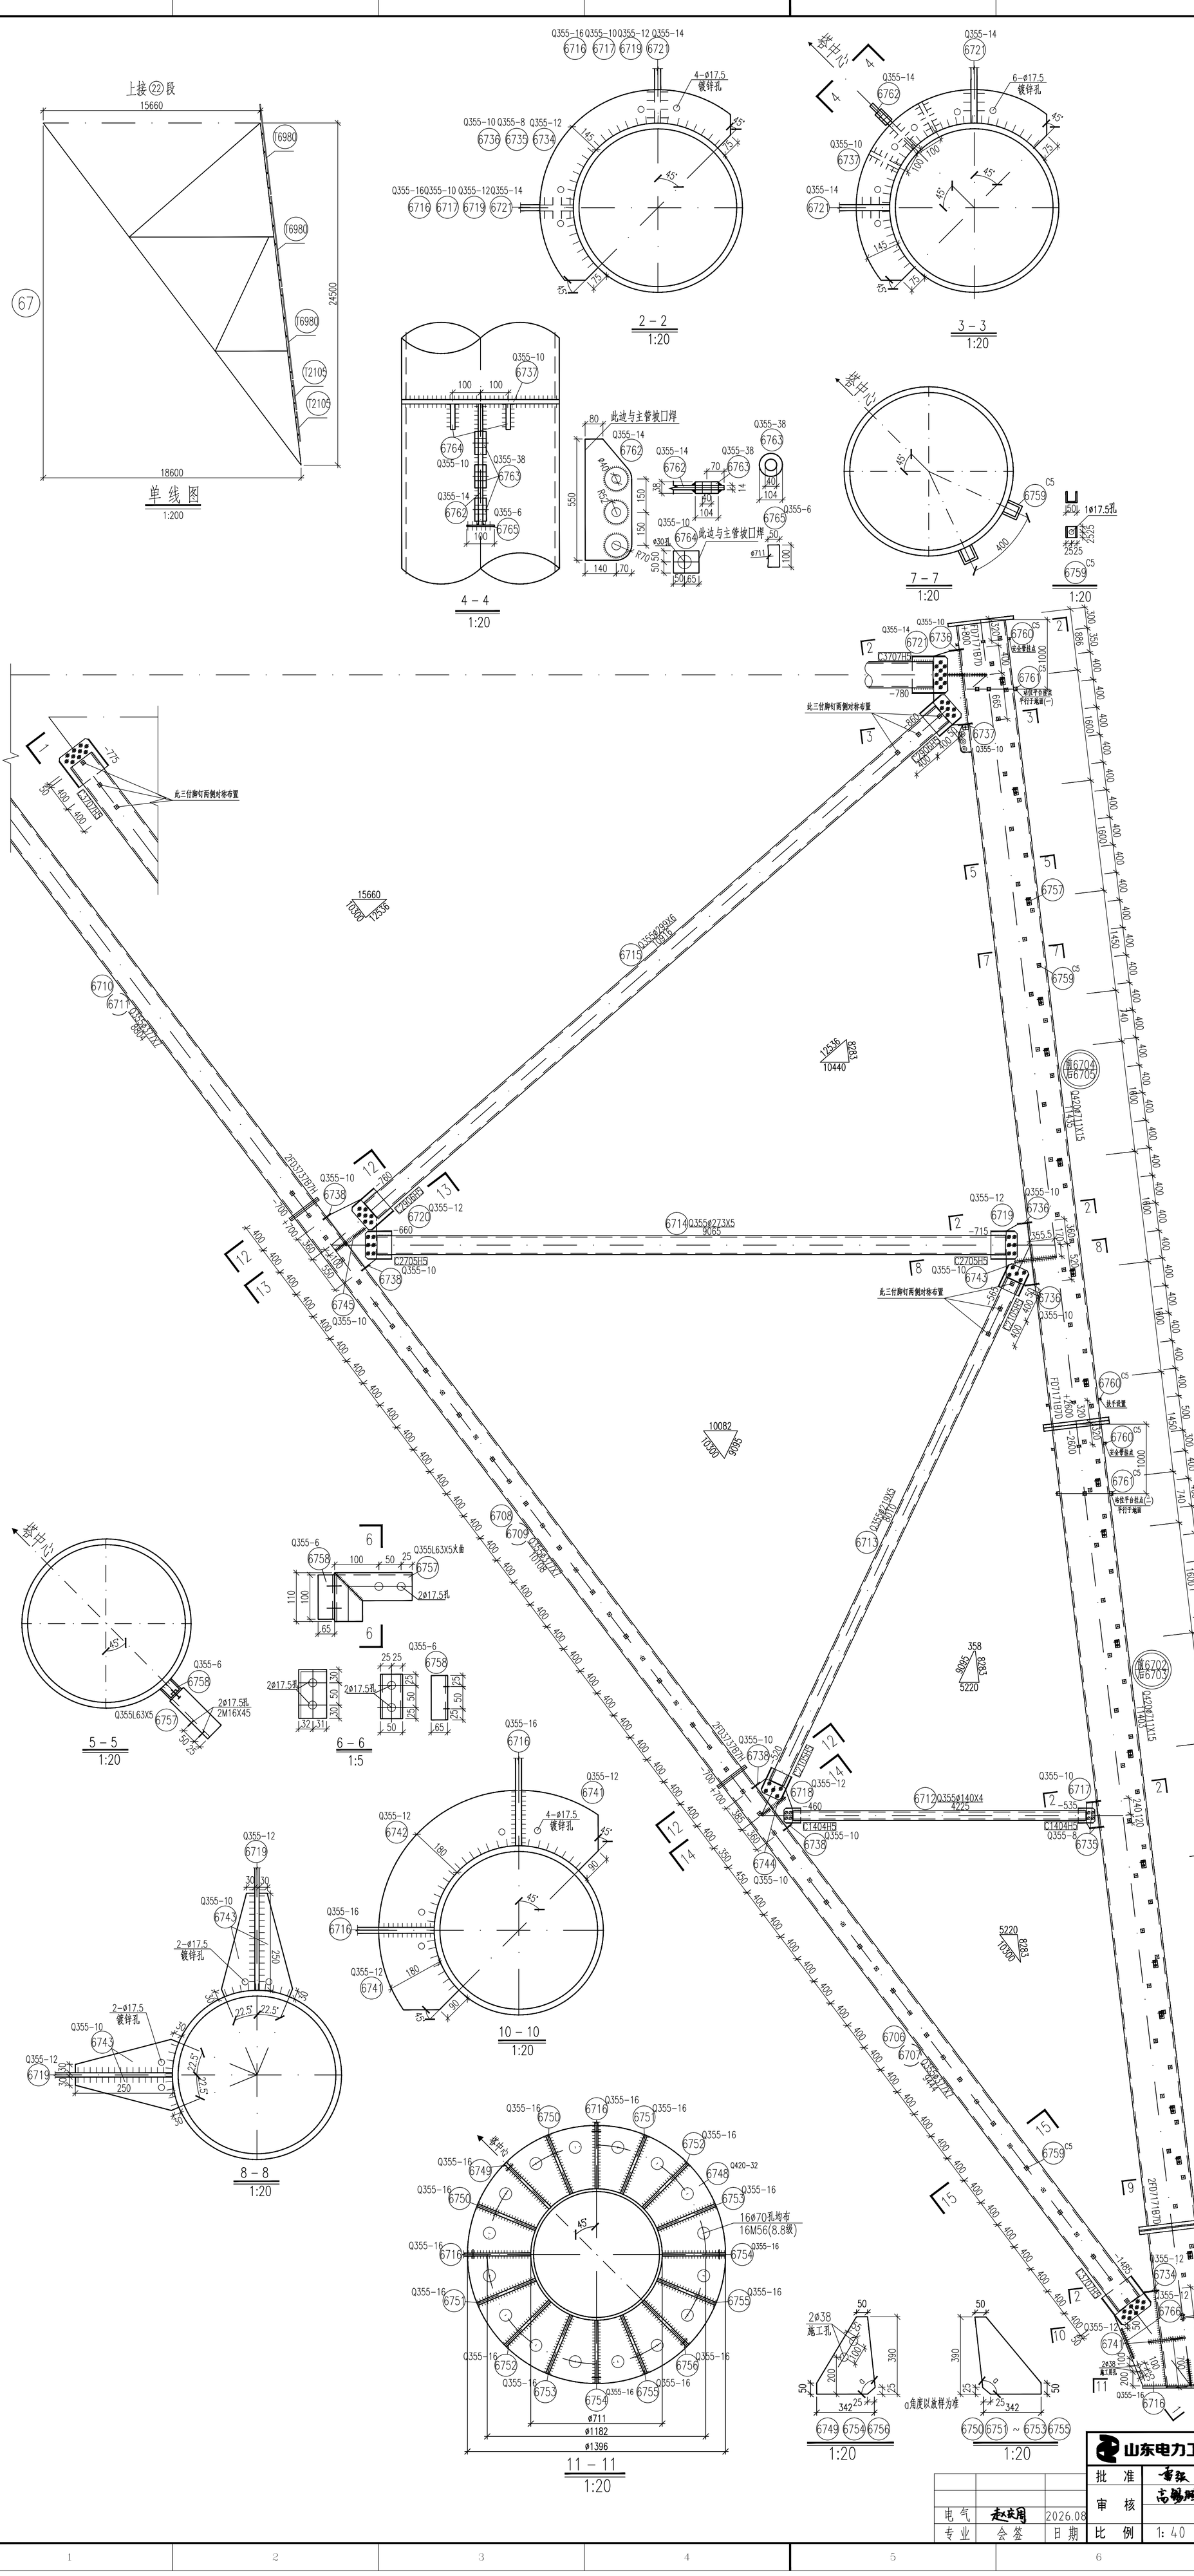

5 – 5
1:20

6 – 6
1:5

8 – 8
1:20

10 – 10
1:20

11 – 11
1:20

1:20

1:20

构件明细表

编号	规格	长度(mm)	数量	重量(kg) 一件	重量(kg) 小计	备注
6701	Q420ø711X15	2234	1	575.18	575.2	一端切弧 装爬梯
6701A	Q420ø711X15	2234	0	575.18	0.0	一端切弧 带脚钉
6702	Q420ø711X15	11403	1	2935.89	2935.9	装爬梯
6703	Q420ø711X15	11403	0	2935.89	0.0	带脚钉
6704	Q420ø711X15	11435	1	2944.12	2944.1	装爬梯
6705	Q420ø711X15	11435	0	2944.12	0.0	带脚钉
6706	Q355ø377X7	9444	1	603.22	603.2	带脚钉
6707	Q355ø377X7	9444	1	603.22	603.2	带脚钉
6708	Q355ø377X7	10108	1	645.63	645.6	带脚钉
6709	Q355ø377X7	10108	1	645.63	645.6	带脚钉
6710	Q355ø377X7	8804	1	562.34	562.3	带脚钉
6711	Q355ø377X7	8804	1	562.34	562.3	带脚钉
6712	Q355ø140X4	4225	2	56.68	113.4	
6713	Q355ø219X5	8010	2	211.37	422.7	带脚钉
6714	Q355ø273X5	9065	2	299.57	599.1	
6715	Q355ø299X6	10916	2	473.26	946.5	带脚钉
6716	Q355-16X681	1557	2	133.18	266.4	
6717	Q355-10X189	396	2	5.88	11.8	
6718	Q355-10X371	820	2	23.88	47.8	
6719	Q355-12X439	968	2	40.03	80.1	
6720	Q355-12X630	1001	2	59.41	118.8	
6721	Q355-14X509	1172	2	65.56	131.1	
6722	Q355ø180X5	6332	1	136.64	136.6	
6723	Q355ø219X5	4781	1	126.16	126.2	带脚钉
6724	Q355ø219X5	8538	1	225.30	225.3	带脚钉
6725	Q355ø219X5	3933	1	103.78	103.8	带脚钉
6726	Q355ø219X5	8690	1	229.31	229.3	带脚钉
6727	Q355ø273X5	11123	1	367.58	367.6	带脚钉
6728	Q355ø273X5	11123	1	367.58	367.6	带脚钉
6729	Q355-12X440	820	2	33.99	68.0	
6730	Q355-10X590	440	1	20.38	20.4	
6731	Q355-10X250	594	2	11.66	23.3	
6732	Q355-12X430	1001	2	40.55	81.1	
6733	Q355-12X398	1078	1	40.42	40.4	
6734	Q355-12X145	1480	1	20.22	20.2	
6735	Q355-8X145	1480	4	13.48	53.9	
6736	Q355-10X145	1480	1	16.85	16.8	
6737	Q355-10X145	1480	1	16.85	16.8	
6738	Q355-10X80	593	8	3.72	29.8	
6739	Q355-8X60	482	4	1.82	7.3	
6740	Q355-10X120	385	2	3.63	7.3	
6741	Q355-12X180	350	2	5.93	11.9	
6742	Q355-12X180	700	1	11.87	11.9	
6743	Q355-10X150	344	4	4.05	16.2	
6744	Q355-10X200	250	2	3.92	7.8	
6745	Q355-10X300	293	2	6.90	13.8	
6746	-16X950	950	1	89.03	89.0	遮水板
6747	Q355-8X80	110	1	0.55	0.6	接地孔用
6748	Q420-32X1396	1396	1	284.75	284.8	
6749	Q355-16X342	390	1	16.75	16.8	
6750	Q355-16X342	390	2	16.75	33.5	
6751	Q355-16X342	390	2	16.75	33.5	
6752	Q355-16X342	390	2	16.75	33.5	
6753	Q355-16X342	390	2	16.75	33.5	
6754	Q355-16X342	390	2	16.75	33.5	
6755	Q355-16X342	390	2	16.75	33.5	
6756	Q355-16X342	390	1	16.75	16.8	
6757	Q355L63X5	285	18	1.37	24.7	火曲 (用于主材装爬梯)
6758	Q355-6X100	180	18	0.85	15.3	火曲 (用于主材装爬梯)
6759	C5	50	224	0.27	60.5	槽钢 (用于主材装爬梯)
6759	C5	50	284	0.27	76.7	槽钢 (用于主材带脚钉)
6760	C5	25	12	0.14	1.7	槽钢
6761	C5	50	8	0.27	2.2	槽钢
6762	Q355-14X210	550	1	12.69	12.7	
6763	Q355-38X104	104	3	3.23	9.7	
6764	Q355-10X100	115	2	0.90	1.8	
6765	Q355-6X50	100	1	0.24	0.2	
6766	Q355-12X100	465	2	4.38	8.8	
	C1404H5		4	4.80	19.2	
	C1805H5		2	7.12	14.2	
	C2105H5		8	14.54	116.3	
	C2705H5		8	18.10	144.8	
	C2906H5		4	23.31	93.2	
	X2105H7		2	22.90	45.8	
	C3707H5		4	39.39	157.6	
	FD2121B7H		2	9.20	18.4	
	FD3737B7H		8	21.70	173.6	
	FD7171B7D		5	142.30	711.5	
	T2105		2	11.50	23.0	(用于主材装爬梯)
	T5530		1	28.80	28.8	(用于主材装爬梯)
	T6980		3	36.20	108.6	(用于主材装爬梯)
合计	17035.8 kg(用于主材带脚钉)					
合计	17220.0 kg(用于主材装爬梯)					

螺栓、脚钉、垫圈明细表

名称	级别	规格	符号	数量	重量(kg)	备注
螺栓	6.8级	M16X45		72	12.1	用于主材装爬梯
		M20X65		28	9.9	
		M20X75		32	12.1	
	8.8级	M24X75		156	92.5	
		M20X90		14	6.6	法兰螺栓
		M24X110		88	72.4	法兰螺栓
		M42X190		56	250.7	法兰螺栓
		M42X205		28	131.5	法兰螺栓 无扣长101mm
脚钉	6.8级	M16X200		224	98.2	用于主材装爬梯
		M16X200		284	124.5	用于主材带脚钉
垫圈	Q235		规格X个数			
合计			700.2 kg	(用于主材带脚钉)		
合计			686.0 kg	(用于主材装爬梯)		

说明：1.材料表为一个塔腿的重量。

2.本段塔腿为铁塔D腿，安装爬梯，
当为A、B、C腿时需焊接脚钉连接槽钢。

山东电力工程咨询院有限公司		浙江特高压交流环网工程线路 工程	施工图 设计阶段
批准	董强	校核	李一丹
审核	高鹏鹏		
电气	赵安周 2026.08	设计/勘测	潘祖光
专业	会签 日期	日期	2026年 08月
比例	1:40	图号	37-SA36901S-T0121-150 版本

SZK31102A双回路直线塔
135.0-1.5m呼高腿部结构图(1/2) 67