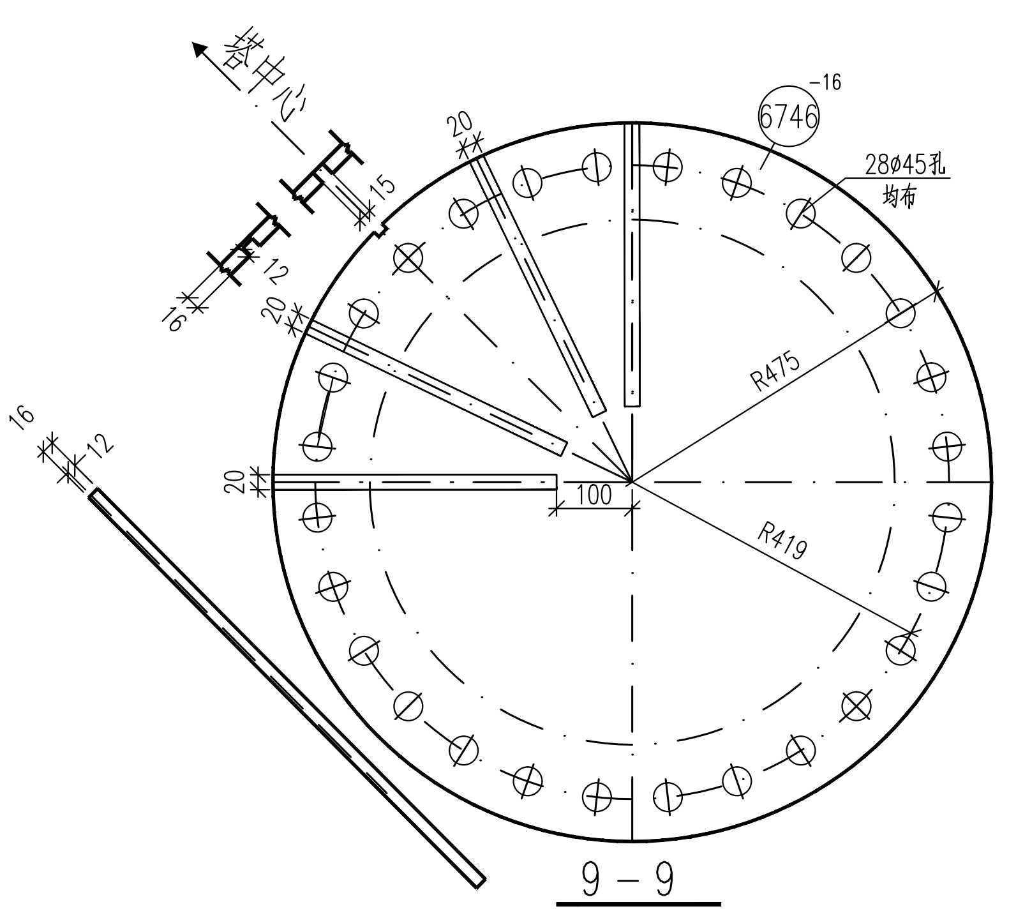

9 — 9
1:20

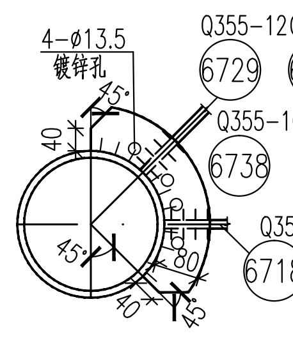

12 — 12
1:20

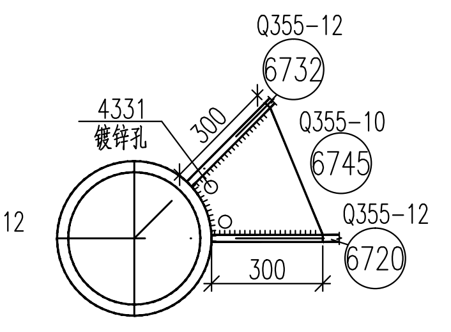

13 — 13
1:10

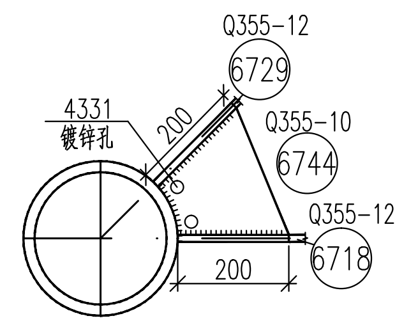

14 — 14
1:10

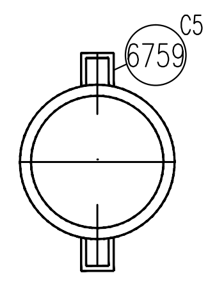

15 — 15
1:10

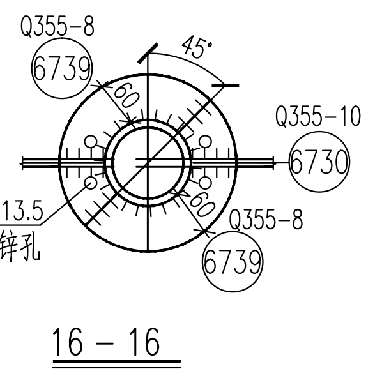

16 — 16
1:10

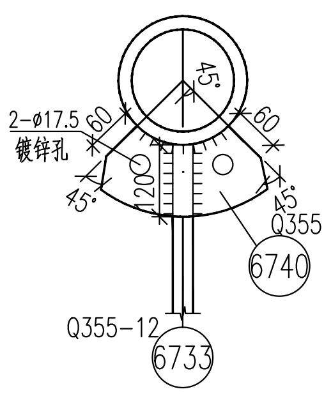

17 — 17
1:10

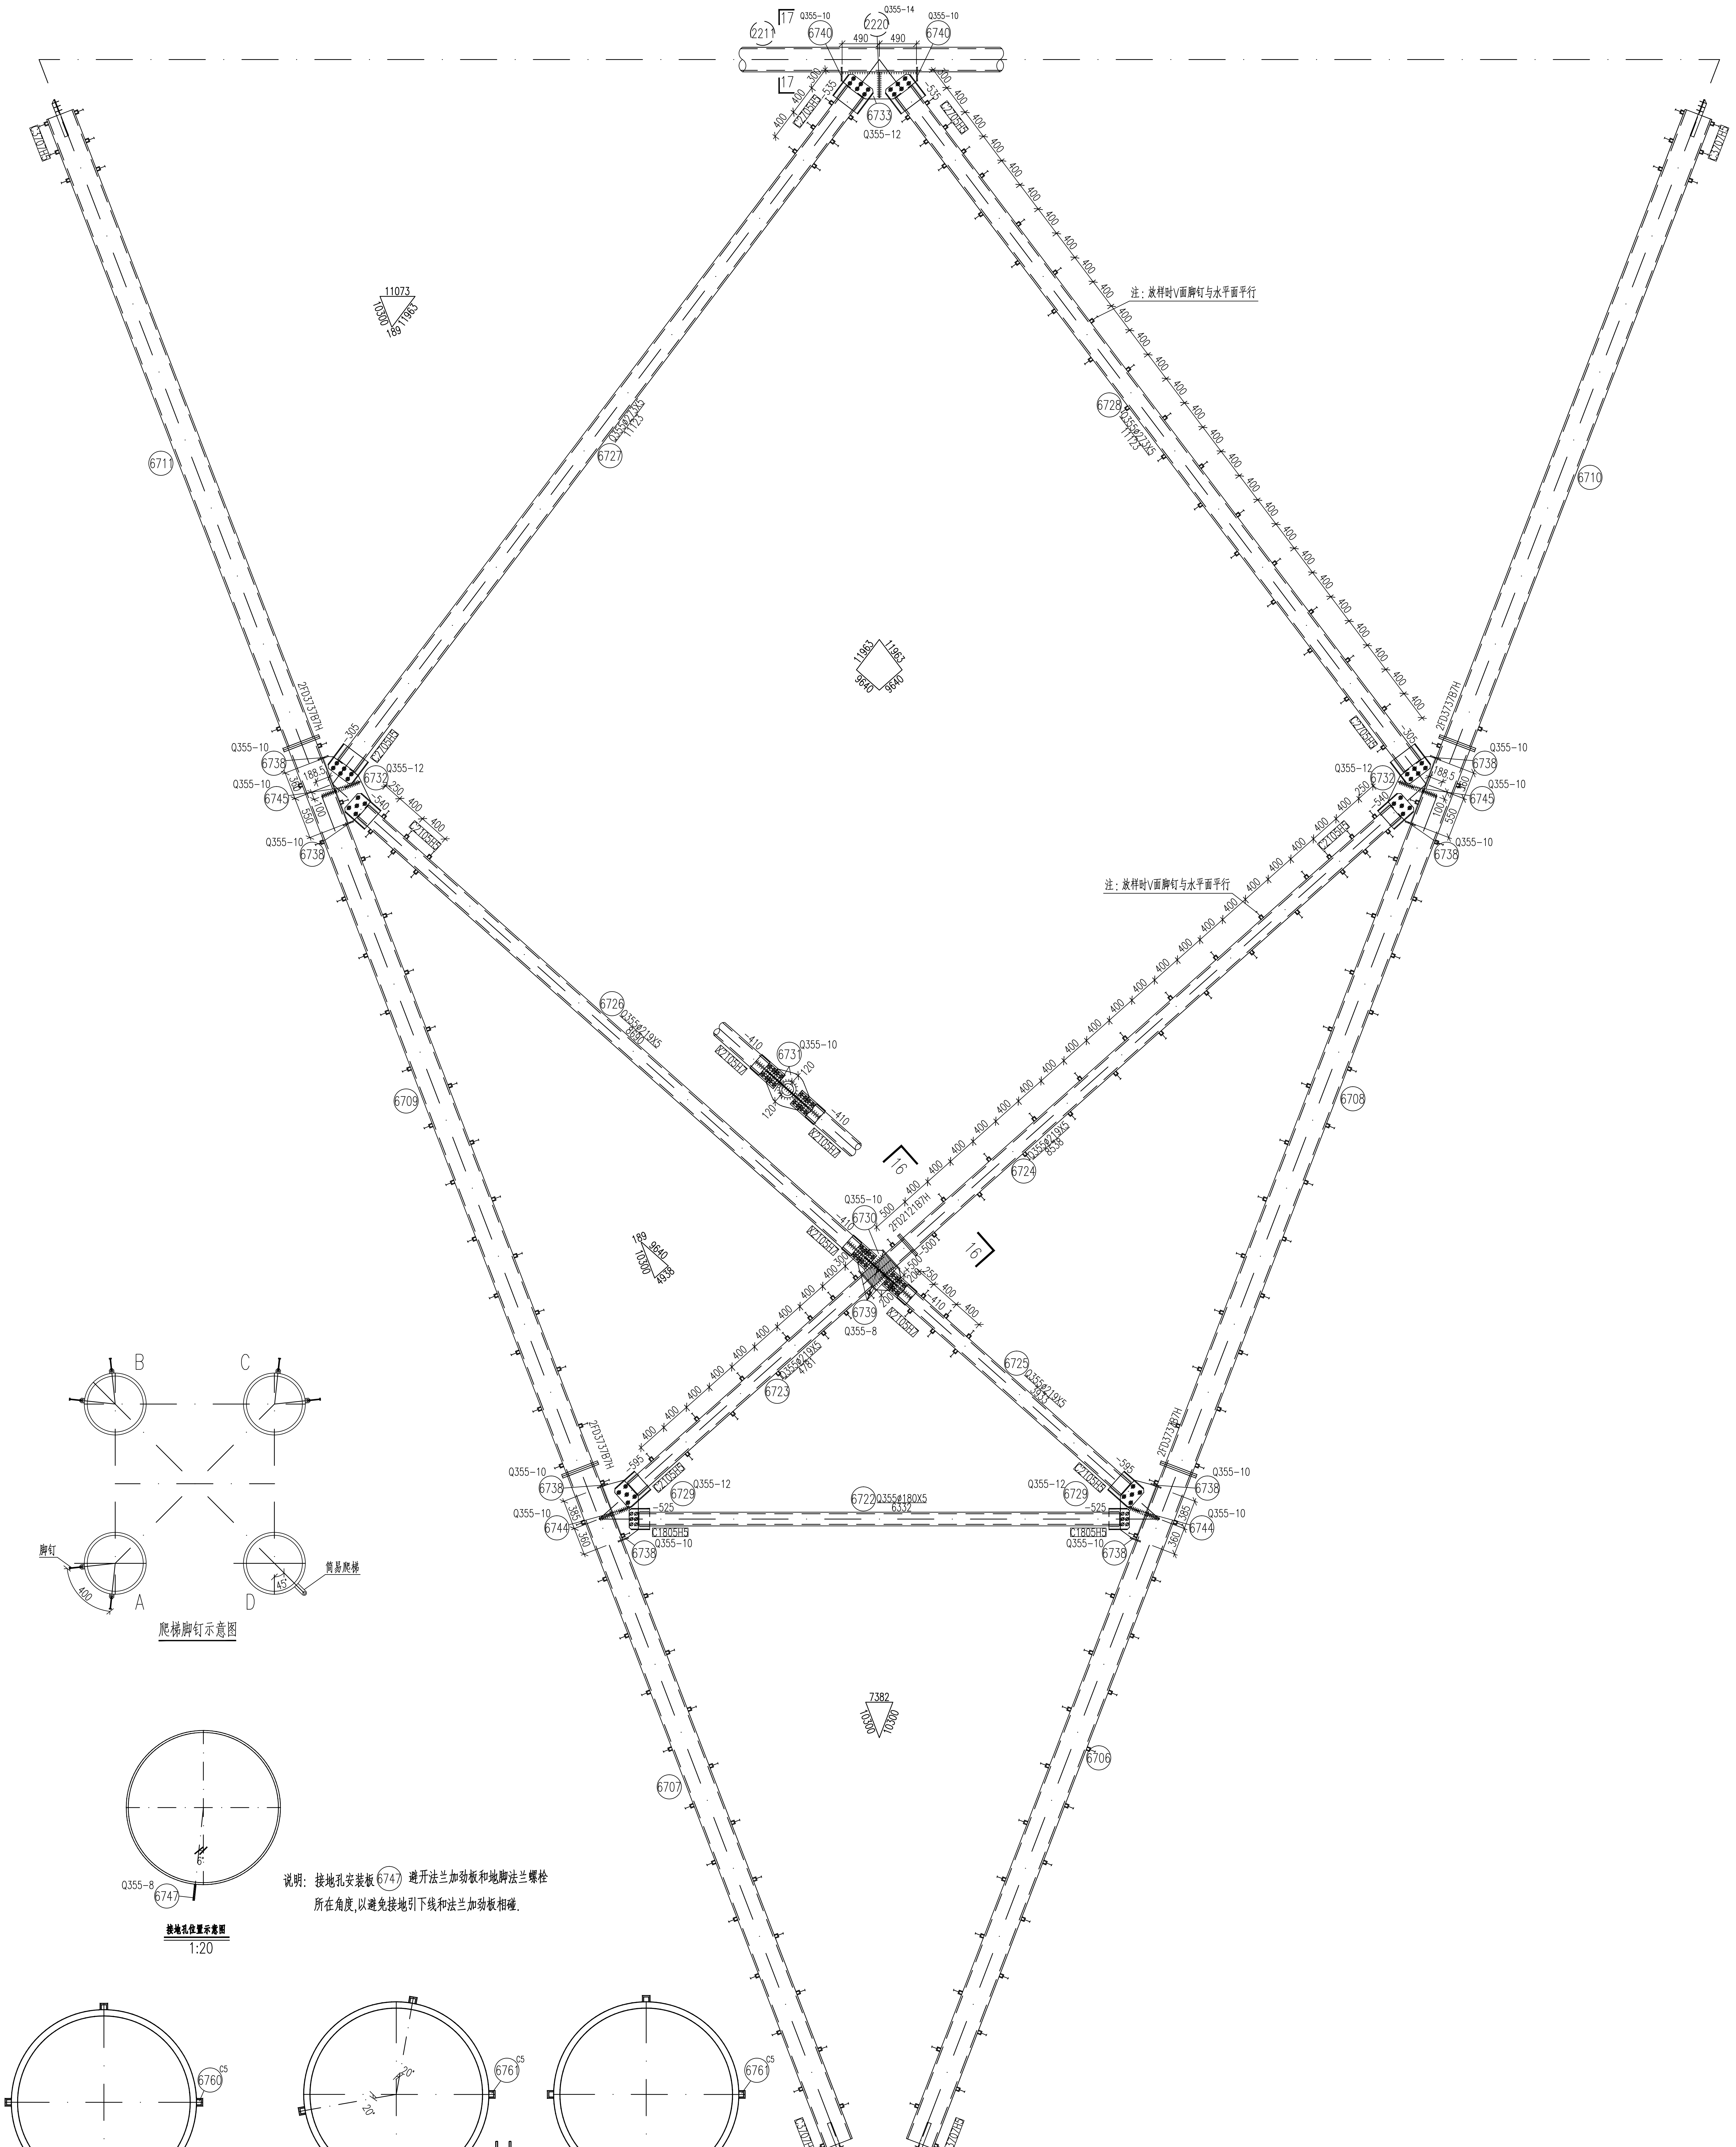

B
C
A
D
脚钉
400
45°
简易爬梯

爬梯脚钉示意图

Q355-8
6747
6°

接地孔位置示意图
1:20

说明：接地孔安装板 6747 避开法兰加劲板和地脚法兰螺栓
所在角度，以避免接地引下线和法兰加劲板相碰.

C5
6760
C5
6761
20°
20°
C5
6761
50
50
50
50

安全带挂点示意
扶手设置示意

站位平台示意(一)

站位平台示意(二)

1 — 1

山东电力工程咨询院有限公司				浙江特高压交流环网工程线路 工程	施工图	设计阶段
批 准	雷强	校 核	马一丹	SZK31102A双回路直线塔 135.0-1.5m呼高腿部结构图（2/2）	(67)	
审 核	高锡鹏					
		设计/勘测	潘旭光			
比 例	1: 40	日 期	2026年 08月	图 号	37-SA36901S-T0121-151	版本