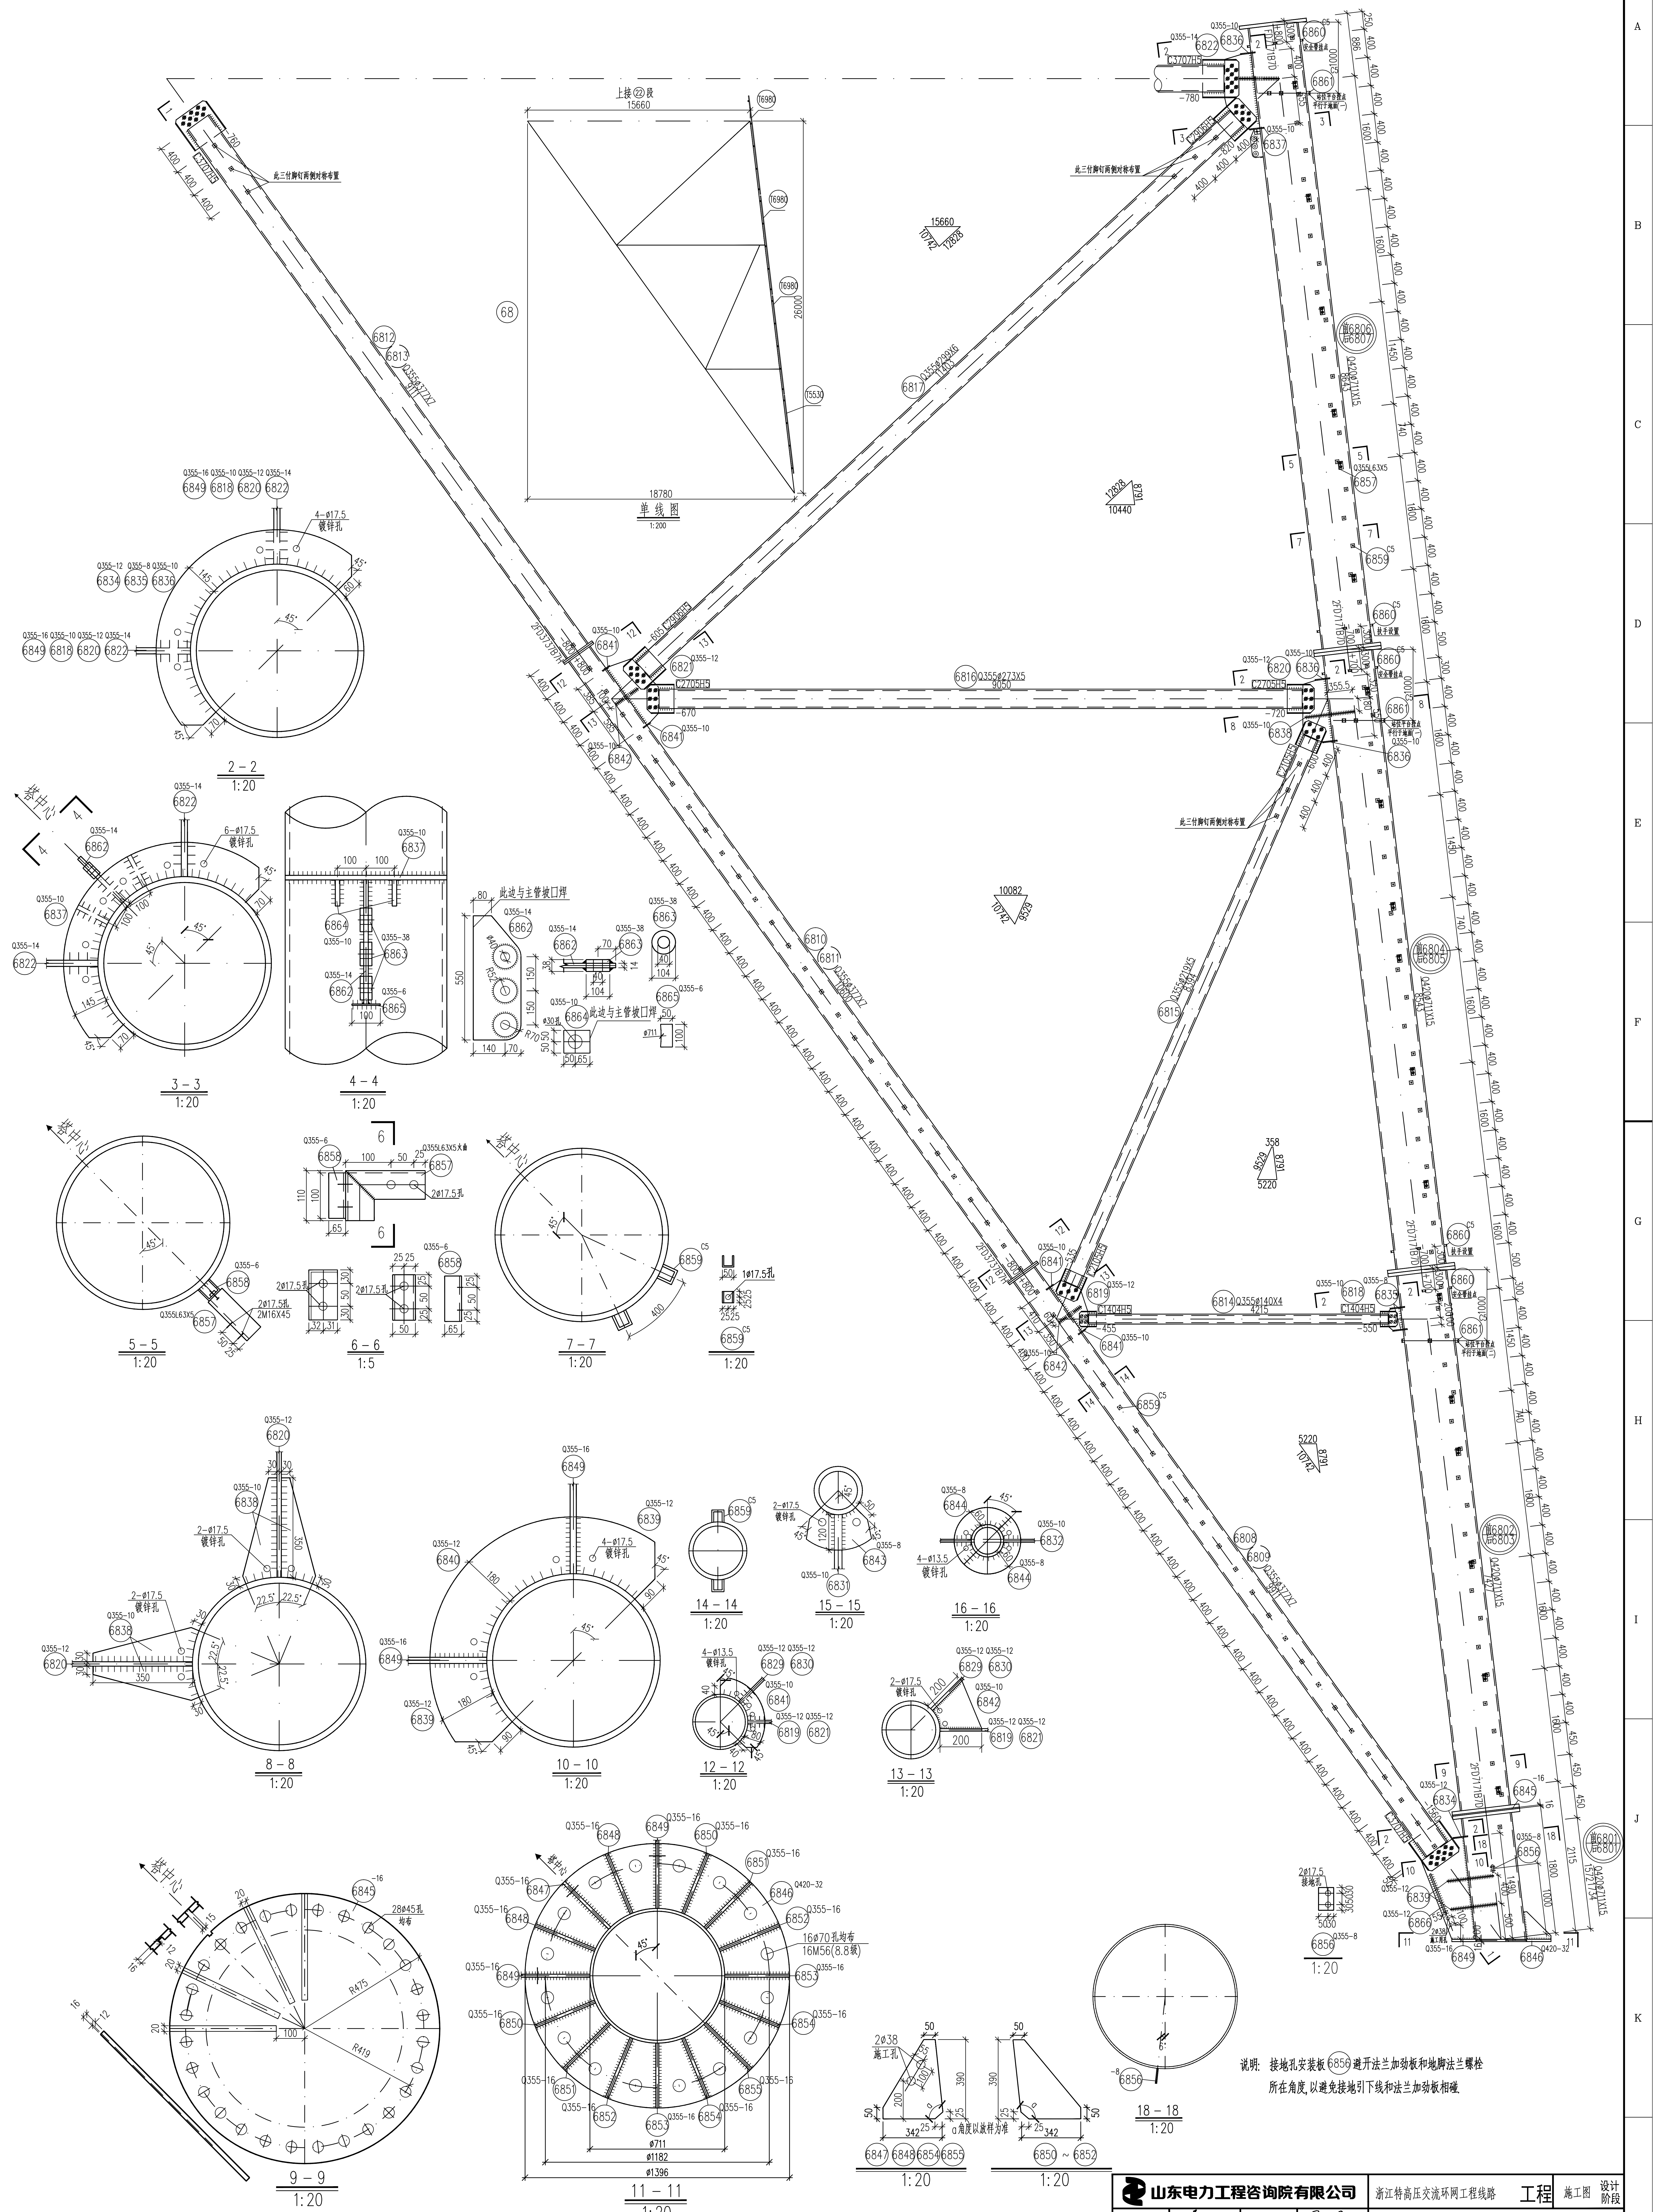

说明：接地孔安装板⑥⑧⑤⑥避开法兰加劲板和地脚法兰螺栓所在角度，以避免接地引下线和法兰加劲板相碰。

			山东电力工程咨询院有限公司		浙江特高压交流环网工程线路 工程	施工图 设计阶段
			批 准	雷强	校 核	马一丹
			审 核	高锡鹏		
电 气	赵庆周	2026.08			设计/勘测	潘胜志
专 业	会 签	日 期	比 例	1:40	日 期	2026年 08月

SZK31102A双回路直线塔
135.0-0.0m塔腿结构图(1/2) ⑥⑧

图 号 37-SA36901S-T0121-152 版本