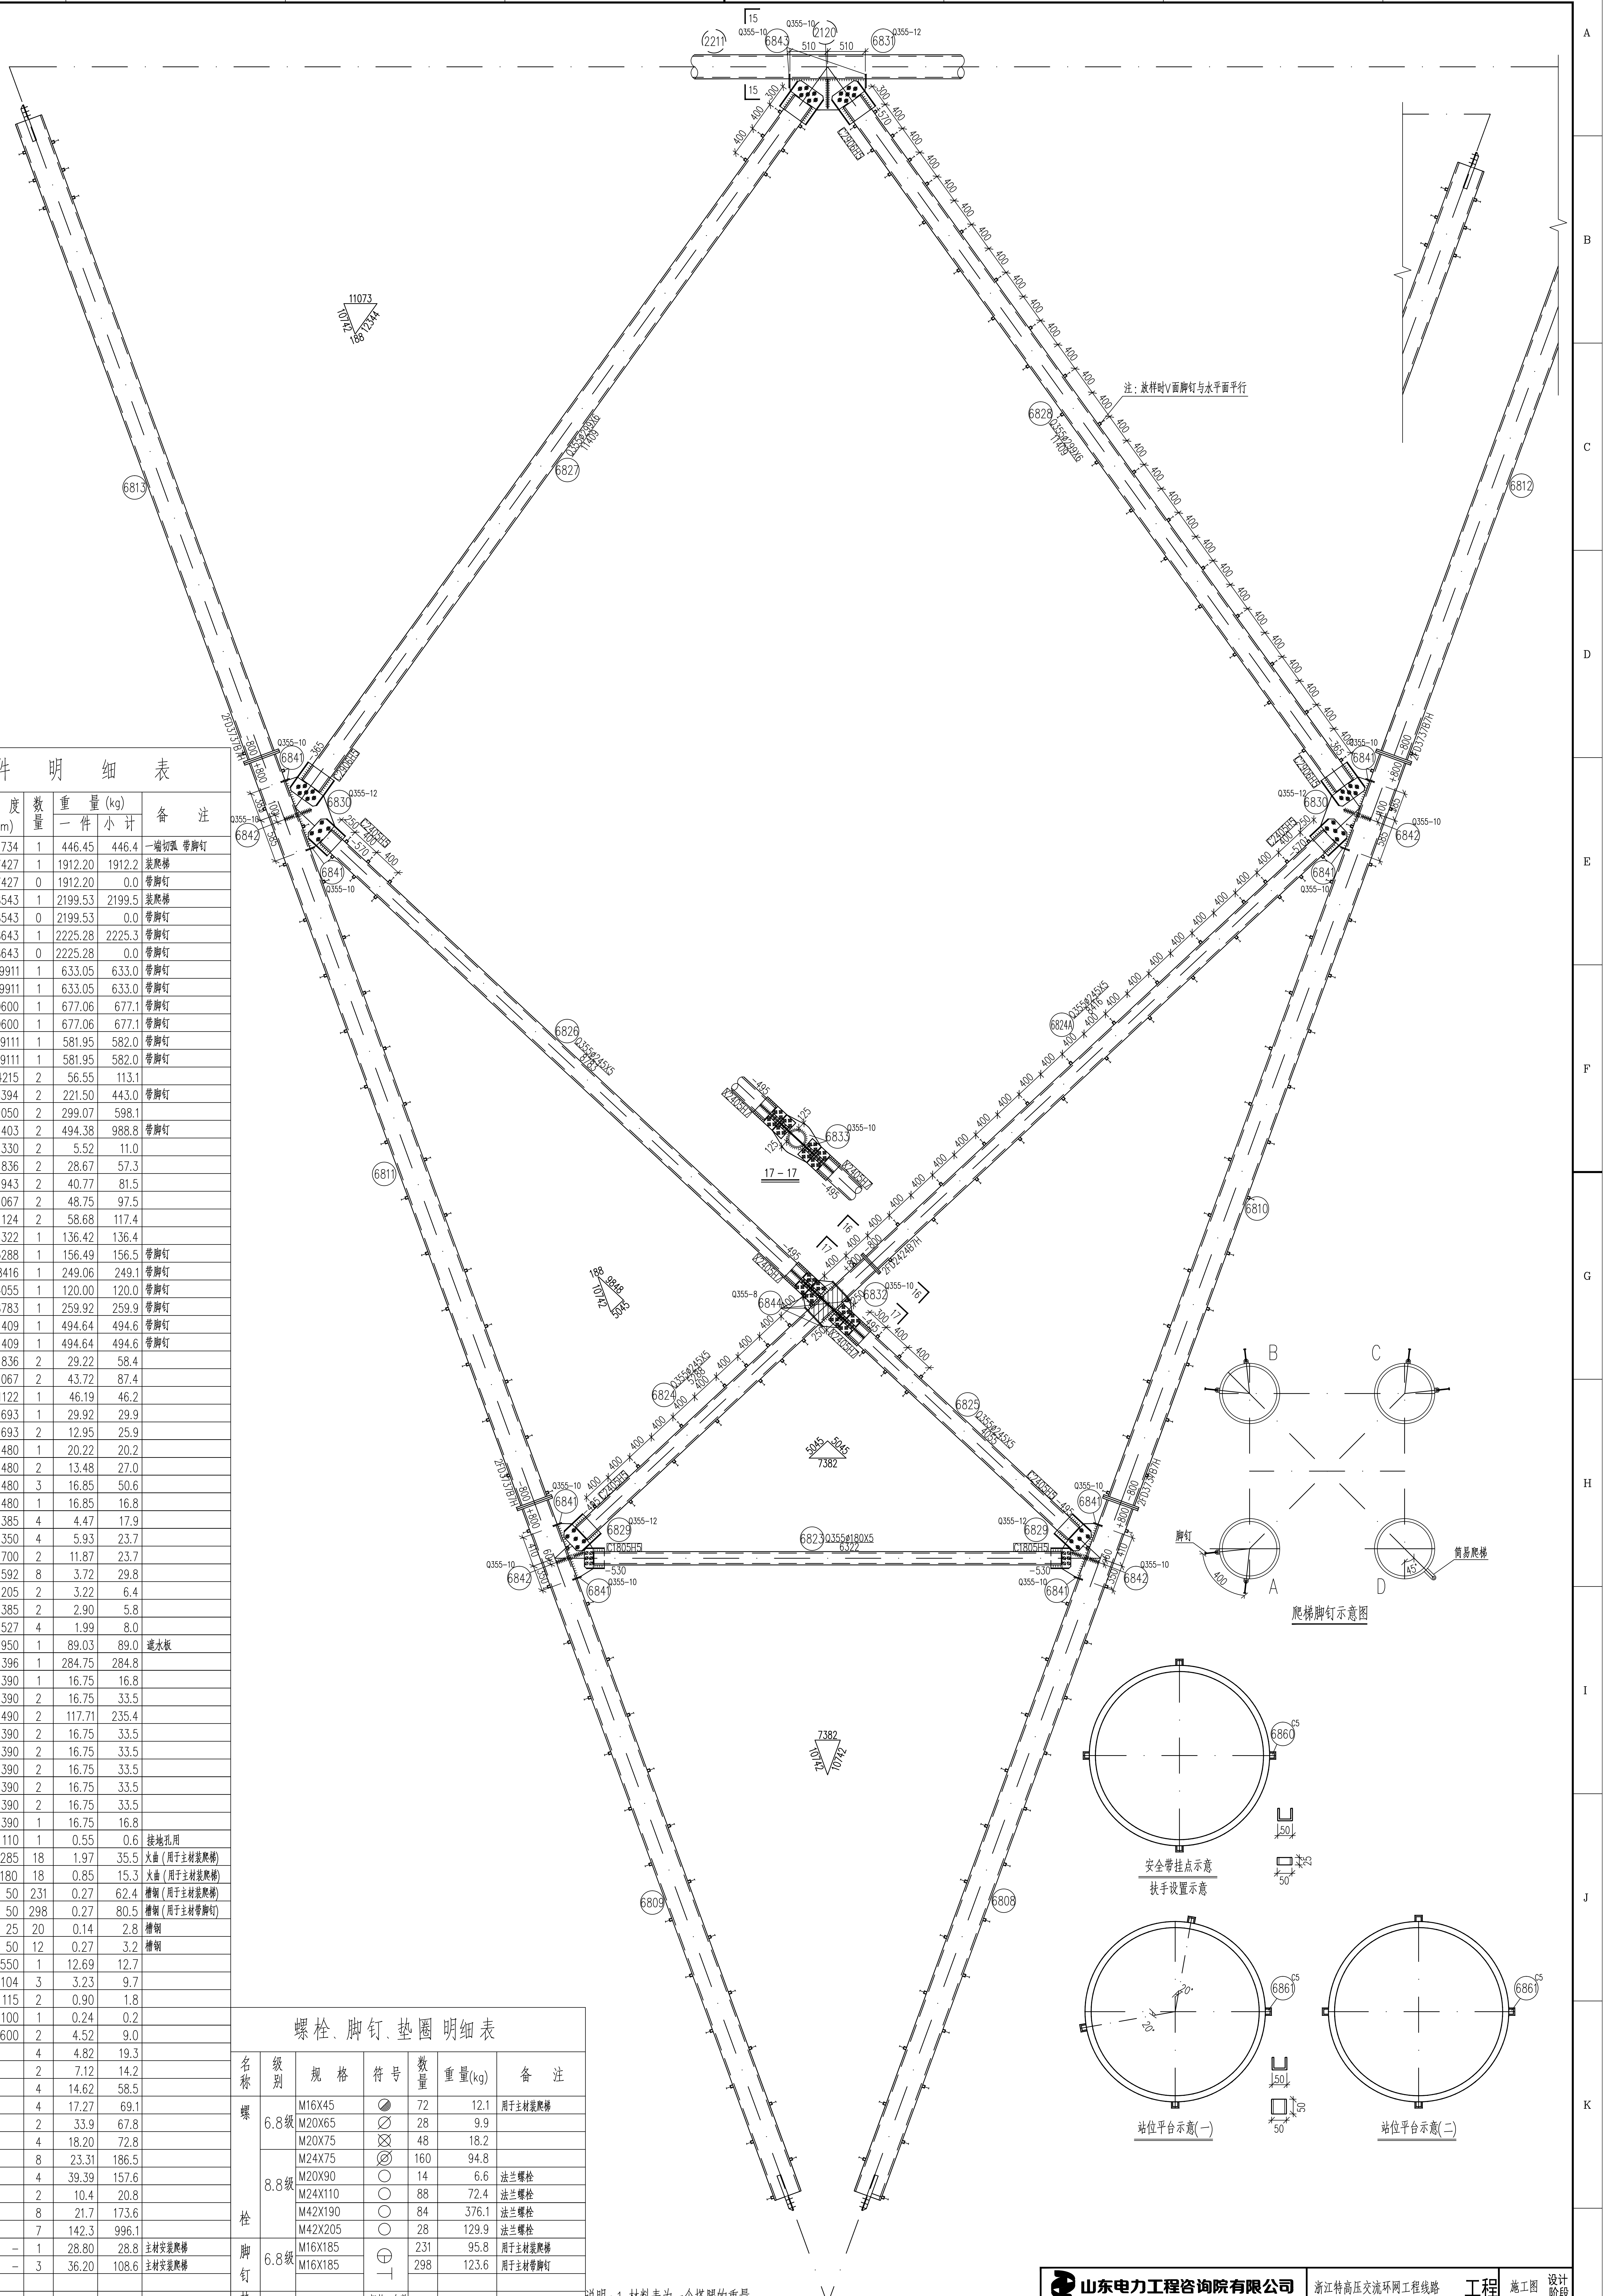

构 件 明 细 表

编号	规 格	长 度 (mm)	数量	重 量 (kg) 一 件	重 量 (kg) 小 计	备 注
6801	Q420ø711X15	1734	1	446.45	446.4	一端切弧 带脚钉
6802	Q420ø711X15	7427	1	1912.20	1912.2	装爬梯
6803	Q420ø711X15	7427	0	1912.20	0.0	带脚钉
6804	Q420ø711X15	8543	1	2199.53	2199.5	装爬梯
6805	Q420ø711X15	8543	0	2199.53	0.0	带脚钉
6806	Q420ø711X15	8643	1	2225.28	2225.3	带脚钉
6807	Q420ø711X15	8643	0	2225.28	0.0	带脚钉
6808	Q355ø377X7	9911	1	633.05	633.0	带脚钉
6809	Q355ø377X7	9911	1	633.05	633.0	带脚钉
6810	Q355ø377X7	10600	1	677.06	677.1	带脚钉
6811	Q355ø377X7	10600	1	677.06	677.1	带脚钉
6812	Q355ø377X7	9111	1	581.95	582.0	带脚钉
6813	Q355ø377X7	9111	1	581.95	582.0	带脚钉
6814	Q355ø140X4	4215	2	56.55	113.1	
6815	Q355ø219X5	8394	2	221.50	443.0	带脚钉
6816	Q355ø273X5	9050	2	299.07	598.1	
6817	Q355ø299X6	11403	2	494.38	988.8	带脚钉
6818	Q355-10X213	330	2	5.52	11.0	
6819	Q355-12X364	836	2	28.67	57.3	
6820	Q355-12X459	943	2	40.77	81.5	
6821	Q355-12X485	1067	2	48.75	97.5	
6822	Q355-14X475	1124	2	58.68	117.4	
6823	Q355ø180X5	6322	1	136.42	136.4	
6824	Q355ø245X5	5288	1	156.49	156.5	带脚钉
6824A	Q355ø245X5	8416	1	249.06	249.1	带脚钉
6825	Q355ø245X5	4055	1	120.00	120.0	带脚钉
6826	Q355ø245X5	8783	1	259.92	259.9	带脚钉
6827	Q355ø299X6	11409	1	494.64	494.6	带脚钉
6828	Q355ø299X6	11409	1	494.64	494.6	带脚钉
6829	Q355-12X371	836	2	29.22	58.4	
6830	Q355-12X435	1067	2	43.72	87.4	
6831	Q355-12X437	1122	1	46.19	46.2	
6832	Q355-10X550	693	1	29.92	29.9	
6833	Q355-10X238	693	2	12.95	25.9	
6834	Q355-12X145	1480	1	20.22	20.2	
6835	Q355-8X145	1480	2	13.48	27.0	
6836	Q355-10X145	1480	3	16.85	50.6	
6837	Q355-10X145	1480	1	16.85	16.8	
6838	Q355-10X148	385	4	4.47	17.9	
6839	Q355-12X180	350	4	5.93	23.7	
6840	Q355-12X180	700	2	11.87	23.7	
6841	Q355-10X80	592	8	3.72	29.8	
6842	Q355-10X200	205	2	3.22	6.4	
6843	Q355-8X120	385	2	2.90	5.8	
6844	Q355-8X60	527	4	1.99	8.0	
6845	-16X950	950	1	89.03	89.0	遮水板
6846	Q420-32X1396	1396	1	284.75	284.8	
6847	Q355-16X342	390	1	16.75	16.8	
6848	Q355-16X342	390	2	16.75	33.5	
6849	Q355-16X629	1490	2	117.71	235.4	
6850	Q355-16X342	390	2	16.75	33.5	
6851	Q355-16X342	390	2	16.75	33.5	
6852	Q355-16X342	390	2	16.75	33.5	
6853	Q355-16X342	390	2	16.75	33.5	
6854	Q355-16X342	390	2	16.75	33.5	
6855	Q355-16X342	390	1	16.75	16.8	
6856	Q355-8X80	110	1	0.55	0.6	接地孔用
6857	L75X6	285	18	1.97	35.5	火曲（用于主材装爬梯）
6858	Q355-6X100	180	18	0.85	15.3	火曲（用于主材装爬梯）
6859	C5	50	231	0.27	62.4	槽钢（用于主材装爬梯）
6859	C5	50	298	0.27	80.5	槽钢（用于主材带脚钉）
6860	C5	25	20	0.14	2.8	槽钢
6861	C5	50	12	0.27	3.2	槽钢
6862	Q355-14X210	550	1	12.69	12.7	
6863	Q355-38X104	104	3	3.23	9.7	
6864	Q355-10X100	115	2	0.90	1.8	
6865	Q355-6X50	100	1	0.24	0.2	
6866	Q355-12X80	600	2	4.52	9.0	
	C1404H5		4	4.82	19.3	
	C1805H5		2	7.12	14.2	
	C2105H5		4	14.62	58.5	
	C2405H5		4	17.27	69.1	
	X2405H7		2	33.9	67.8	
	C2705H5		4	18.20	72.8	
	C2906H5		8	23.31	186.5	
	C3707H5		4	39.39	157.6	
	FD2424B7H		2	10.4	20.8	
	FD3737B7H		8	21.7	173.6	
	FD7171B7D		7	142.3	996.1	
	T5530	-	1	28.80	28.8	主材安装爬梯
	T6980	-	3	36.20	108.6	主材安装爬梯
合 计		18264.7 kg（用于主材带脚钉）				
合 计		18434.8 kg（用于主材装爬梯）				

螺栓、脚钉、垫圈 明细表

名称	级别	规 格	符 号	数量	重 量(kg)	备 注
螺栓	6.8级	M16X45	◎	72	12.1	用于主材装爬梯
		M20X65	∅	28	9.9	
		M20X75	⊗	48	18.2	
	8.8级	M24X75	∅	160	94.8	
		M20X90	○	14	6.6	法兰螺栓
		M24X110	○	88	72.4	法兰螺栓
		M42X190	○	84	376.1	法兰螺栓
		M42X205	○	28	129.9	法兰螺栓
脚钉	6.8级	M16X185	⊖	231	95.8	用于主材装爬梯
		M16X185		298	123.6	用于主材带脚钉
垫圈	Q235		规格X个数			
合 计			831.5 kg （用于主材带脚钉）			
合 计			815.8 kg （用于主材装爬梯）			

说明：1.材料表为一个塔腿的重量。

2.本段塔腿为铁塔D腿，安装爬梯，当为A、B、C腿时需焊接脚钉连接槽钢。

山东电力工程咨询院有限公司				浙江特高压交流环网工程线路 工程	施工图 设计阶段
批 准		校 核		SZK31102A双回路直线塔 135.0-0.0m塔腿结构图(2/2) ㊳	
审 核	高锡鹏				
		设计/勘测			
比 例	1:40	日 期	2026年 08月	图 号 37-SA36901S-T0121-153	版本