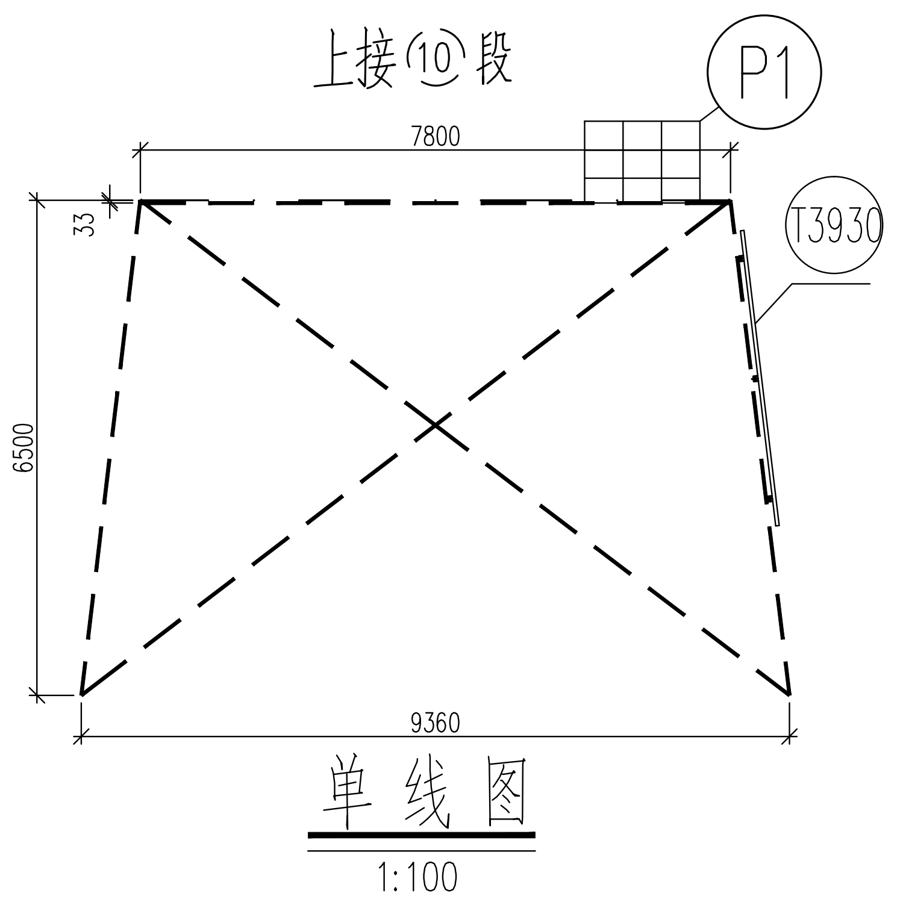

单线图

1:100

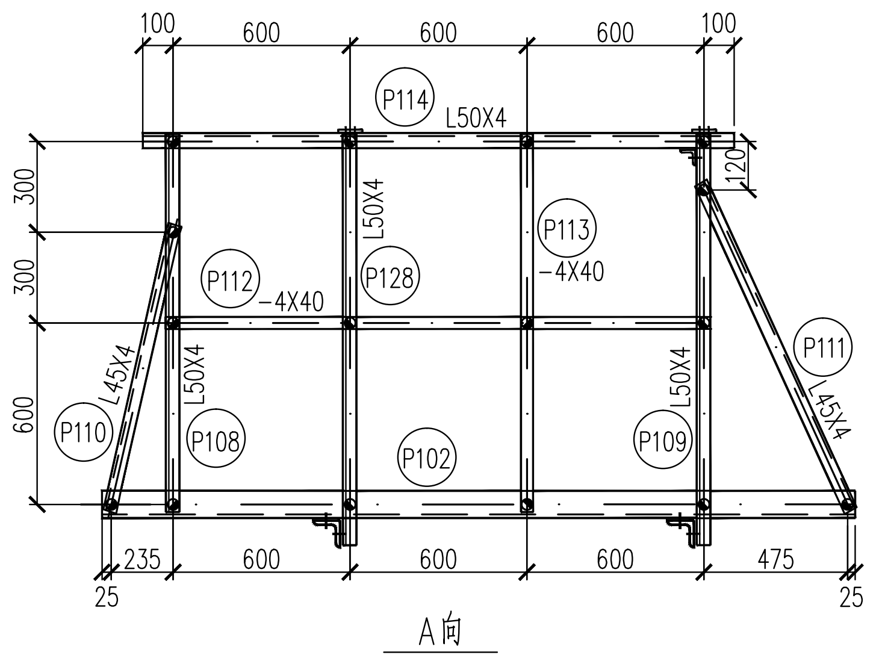

A向

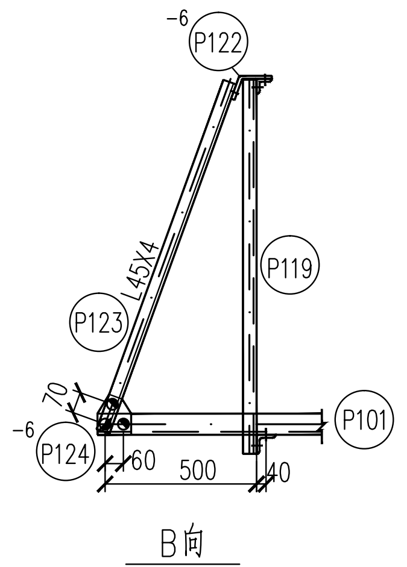

B向

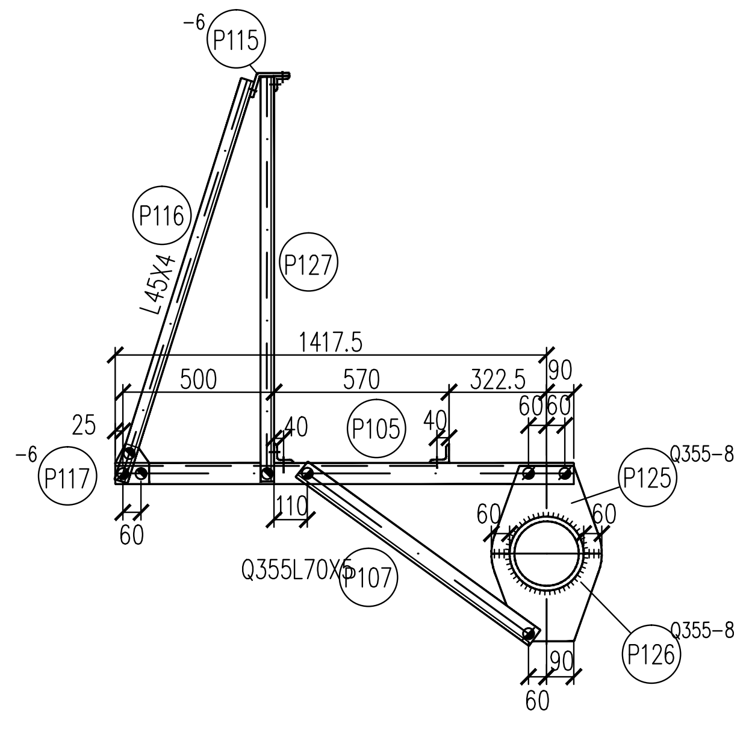

1 - 1

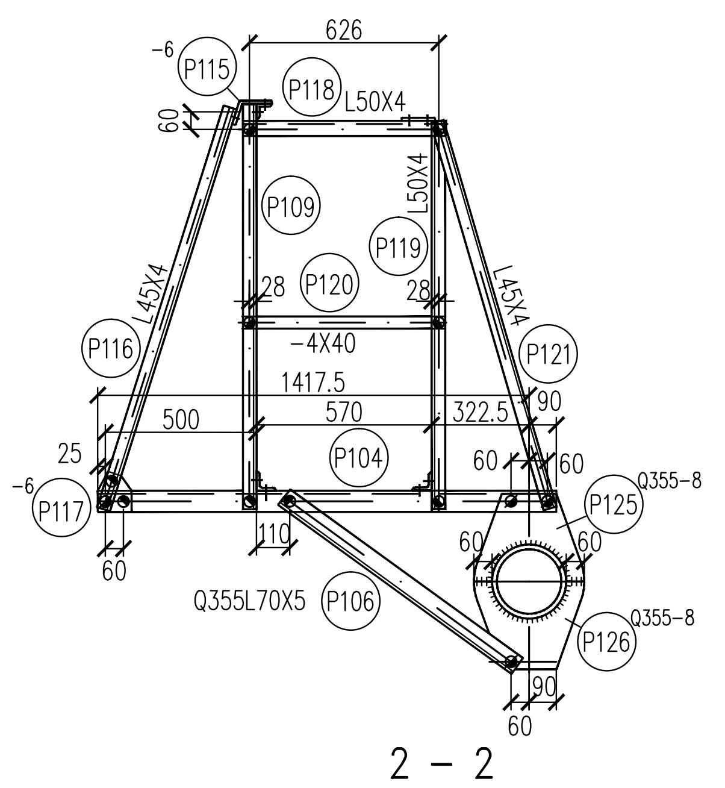

2 - 2

平台及钢格板标准说明:

1. 此段横隔面平台对角布置.
2. 钢格板参考冶金行业标准(YB/T 4001.1-2019)《钢格栅板及配套件》第一部分: 钢格栅板.
3. 钢格栅板长度为总长,加工放样时可用标准件拼装..
4. 钢格板用专用的安装夹具固定,每件钢格板安装夹的数量不少于4个且安装夹间距不大于2m,安装夹由加工厂家配套提供.
5. 钢格板的承载扁钢须搁置在角钢梁上..

说明：平台要结合塔身一起放样。各细部尺寸以实际加工放样为准.

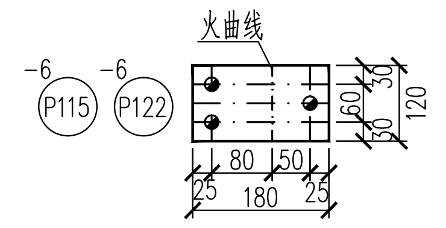

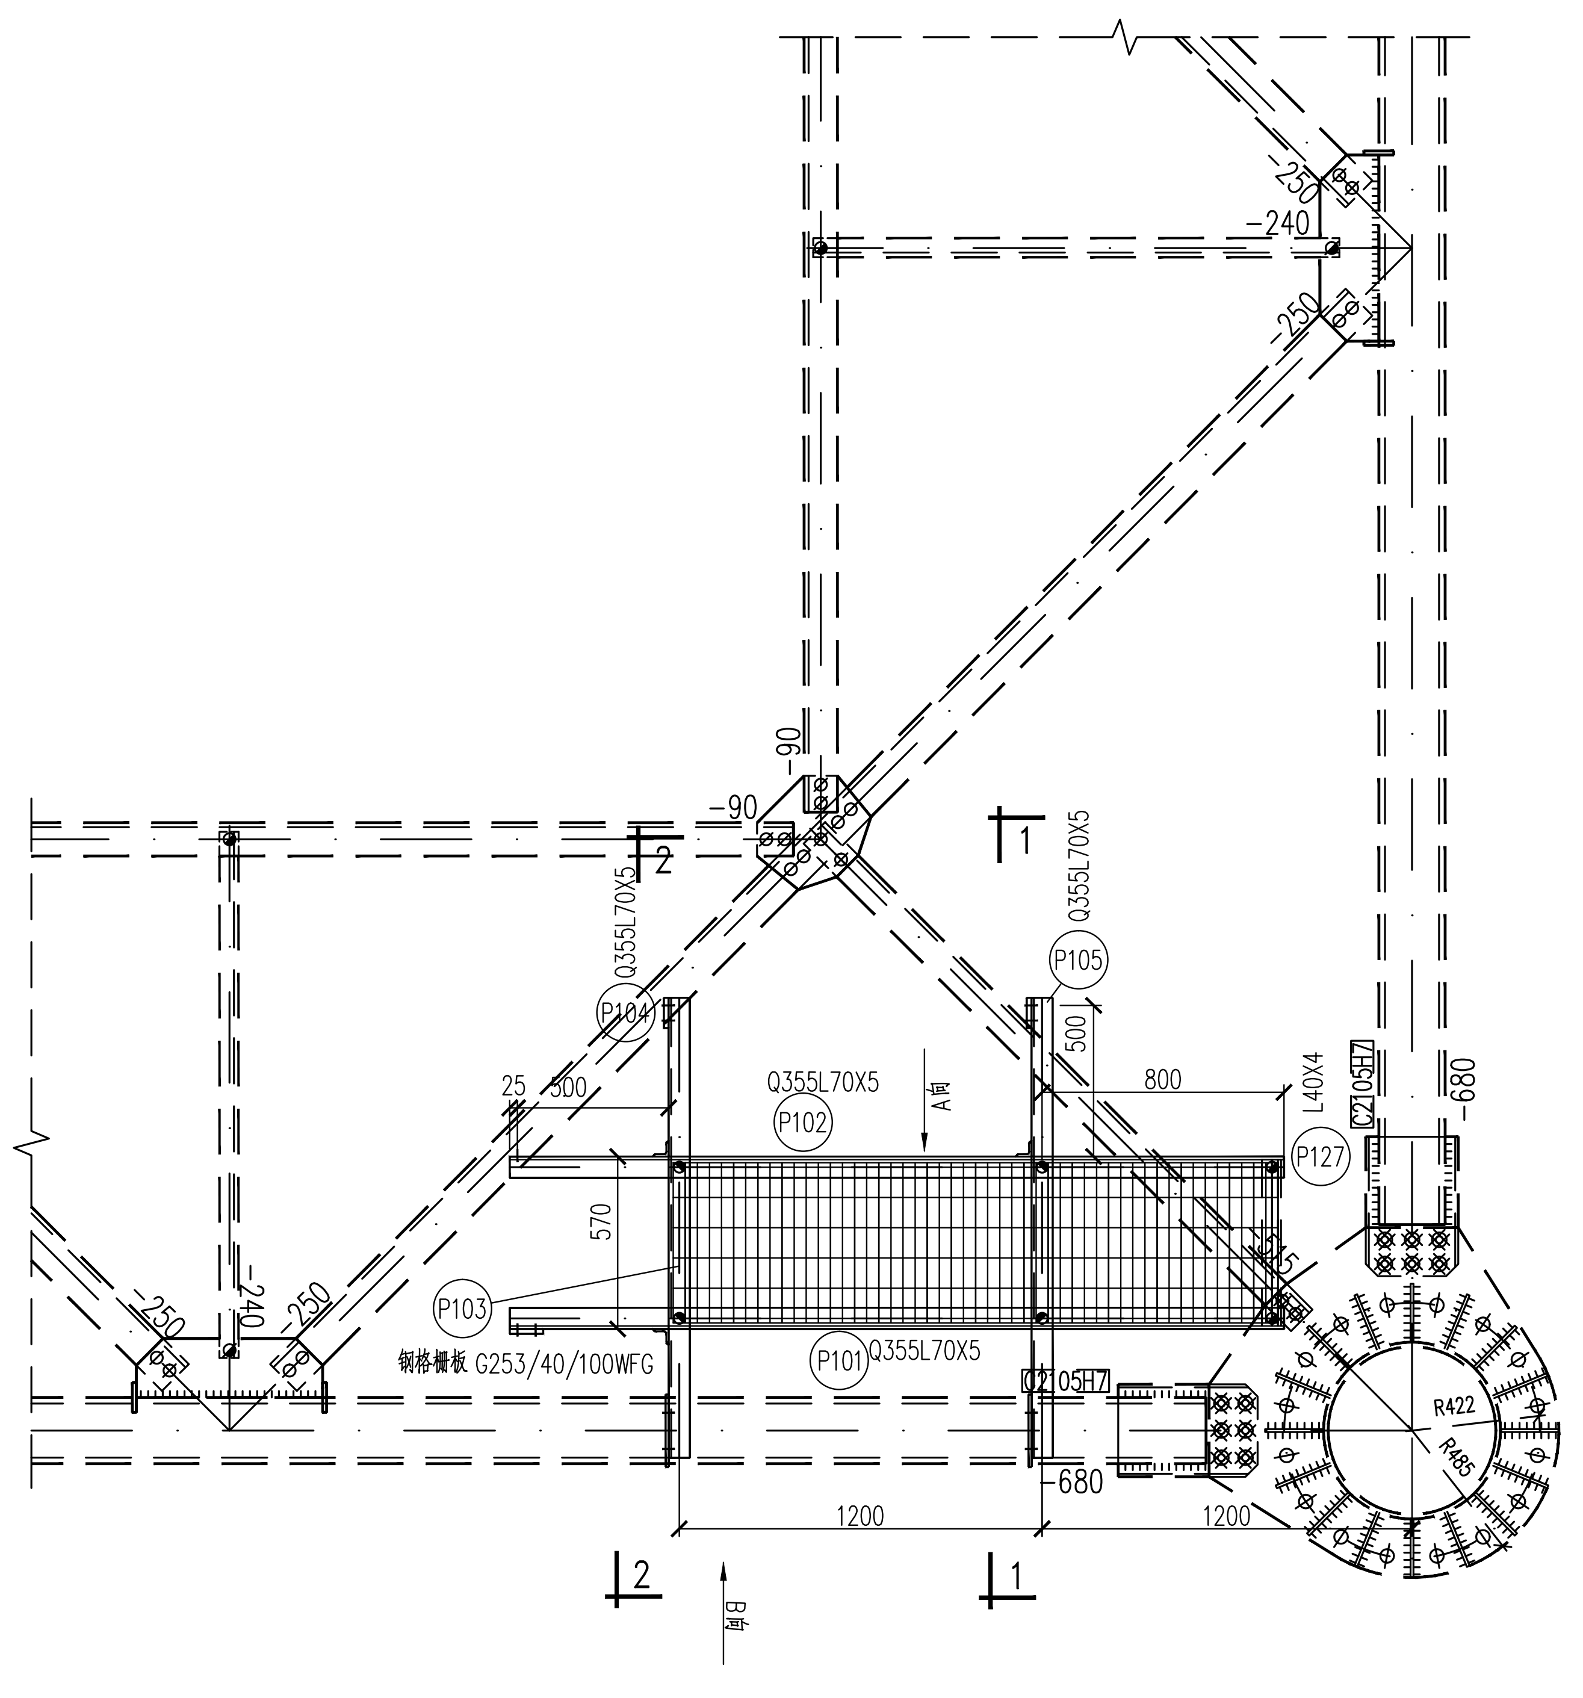

构件明细表

编号	规格	长度 (mm)	数量	重量(kg) 一件	重量(kg) 小计	备注
P101	Q355L70X5	2560	2	13.82	27.6	
P102	Q355L70X5	2560	2	13.82	27.6	
P103	G253/40/100WFG	530X2000	2	26.50	53.0	带夹具重量
P104	Q355L70X5	1521	2	8.21	16.4	
P105	Q355L70X5	1521	2	8.21	16.4	
P106	Q355L70X5	977	2	4.71	9.4	
P107	Q355L70X5	977	2	5.27	10.5	
P108	L50X4	1250	2	3.82	7.6	
P109	L50X4	1320	2	4.04	8.1	
P110	L45X4	973	2	2.66	5.3	
P111	L45X4	1230	2	3.37	6.7	
P112	-4X40	1850	2	2.32	4.6	
P113	-4X40	1250	2	1.57	3.1	
P114	L50X4	2000	2	6.12	12.2	
P115	-6X120	180	4	1.02	4.1	火曲
P116	L45X4	1390	4	3.80	15.2	
P117	-6X110	133	4	0.69	2.8	
P118	L50X4	676	2	2.07	4.1	
P119	L50X4	1260	2	3.85	7.7	
P120	-4X40	676	2	0.85	1.7	
P121	L45X4	1331	2	3.64	7.3	
P122	-6X120	180	2	1.02	2.0	火曲
P123	L45X4	1228	2	3.36	6.7	
P124	-6X110	133	2	0.69	1.4	
P125	Q355-8X340	290	4	6.19	24.8	
P126	Q355-8X340	290	4	6.19	24.8	
P127	L40X4	540	2	1.31	2.6	
P128	L50X4	1320	2	4.04	8.1	
合计		321.8 kg				

螺栓、脚钉、垫圈明细表

名称	级别	规格	符号	数量	重量(kg)	备注
螺栓	6.8级	M16X45	⊘	92	15.5	
		M16X55	⊘	18	3.3	
脚钉			⊖			
			⊣			
垫圈	Q235		规格X个数			
合计			18.8 kg			

山东电力工程咨询院有限公司				浙江特高压交流环网工程线路 工程	施工图 设计阶段
批准		校核	马一丹	SZ27102A双回路直线塔 平台结构图	P1
审核	高锡鹏				
		设计/勘测			
比例	1:25	日期	2026年 08月	图号 37-SA36901S-T0121- 154	版本