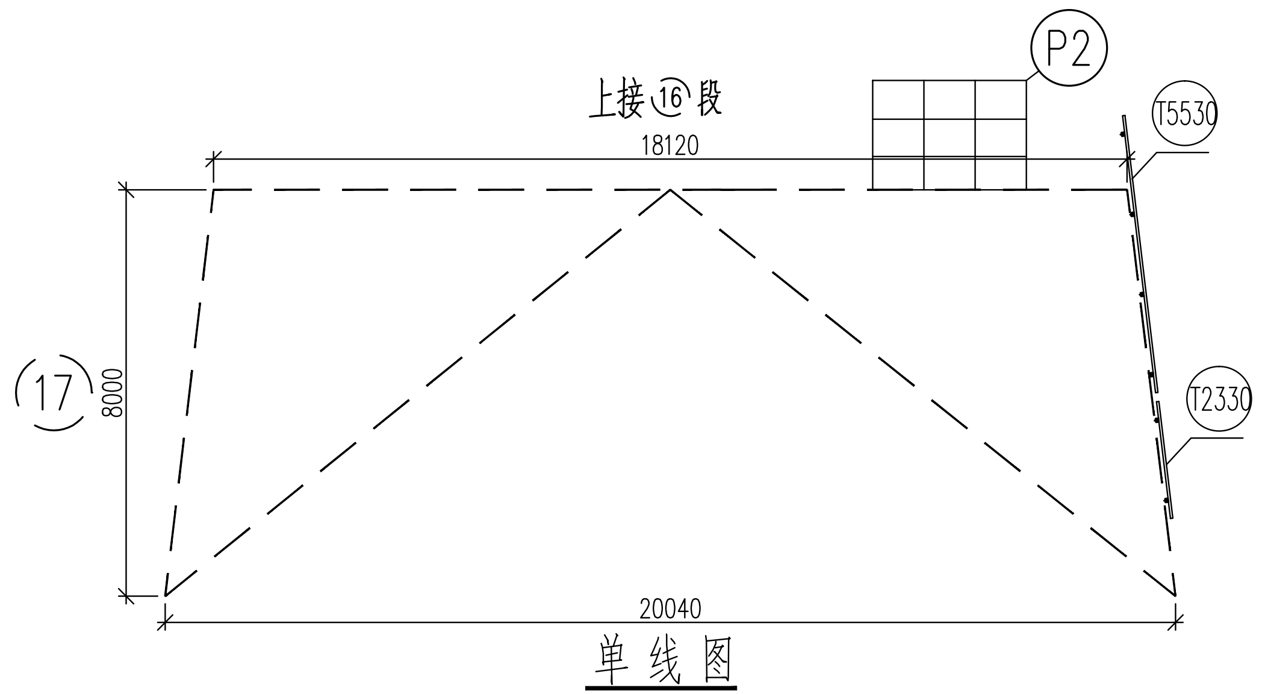

单线图
1:150

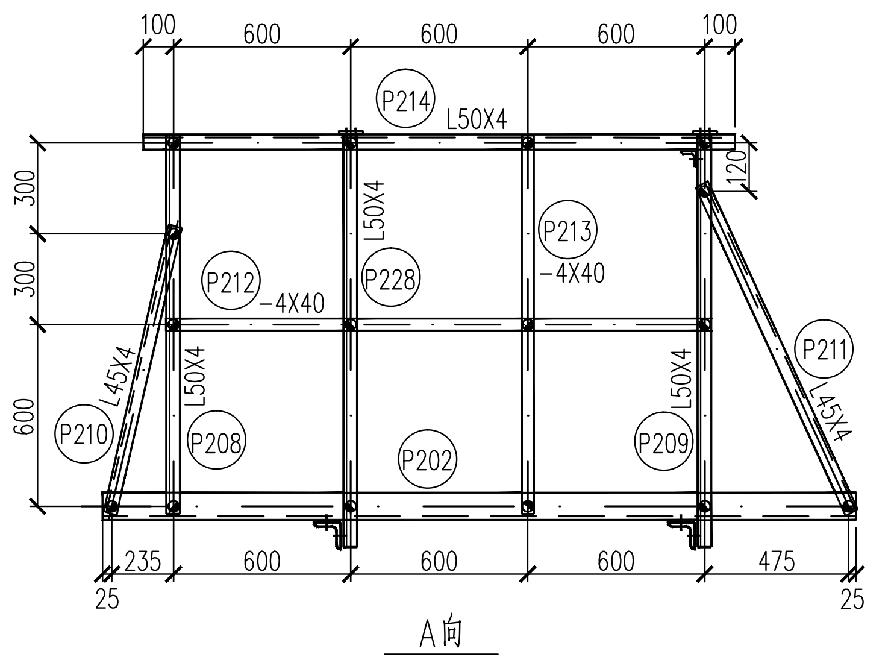

A向

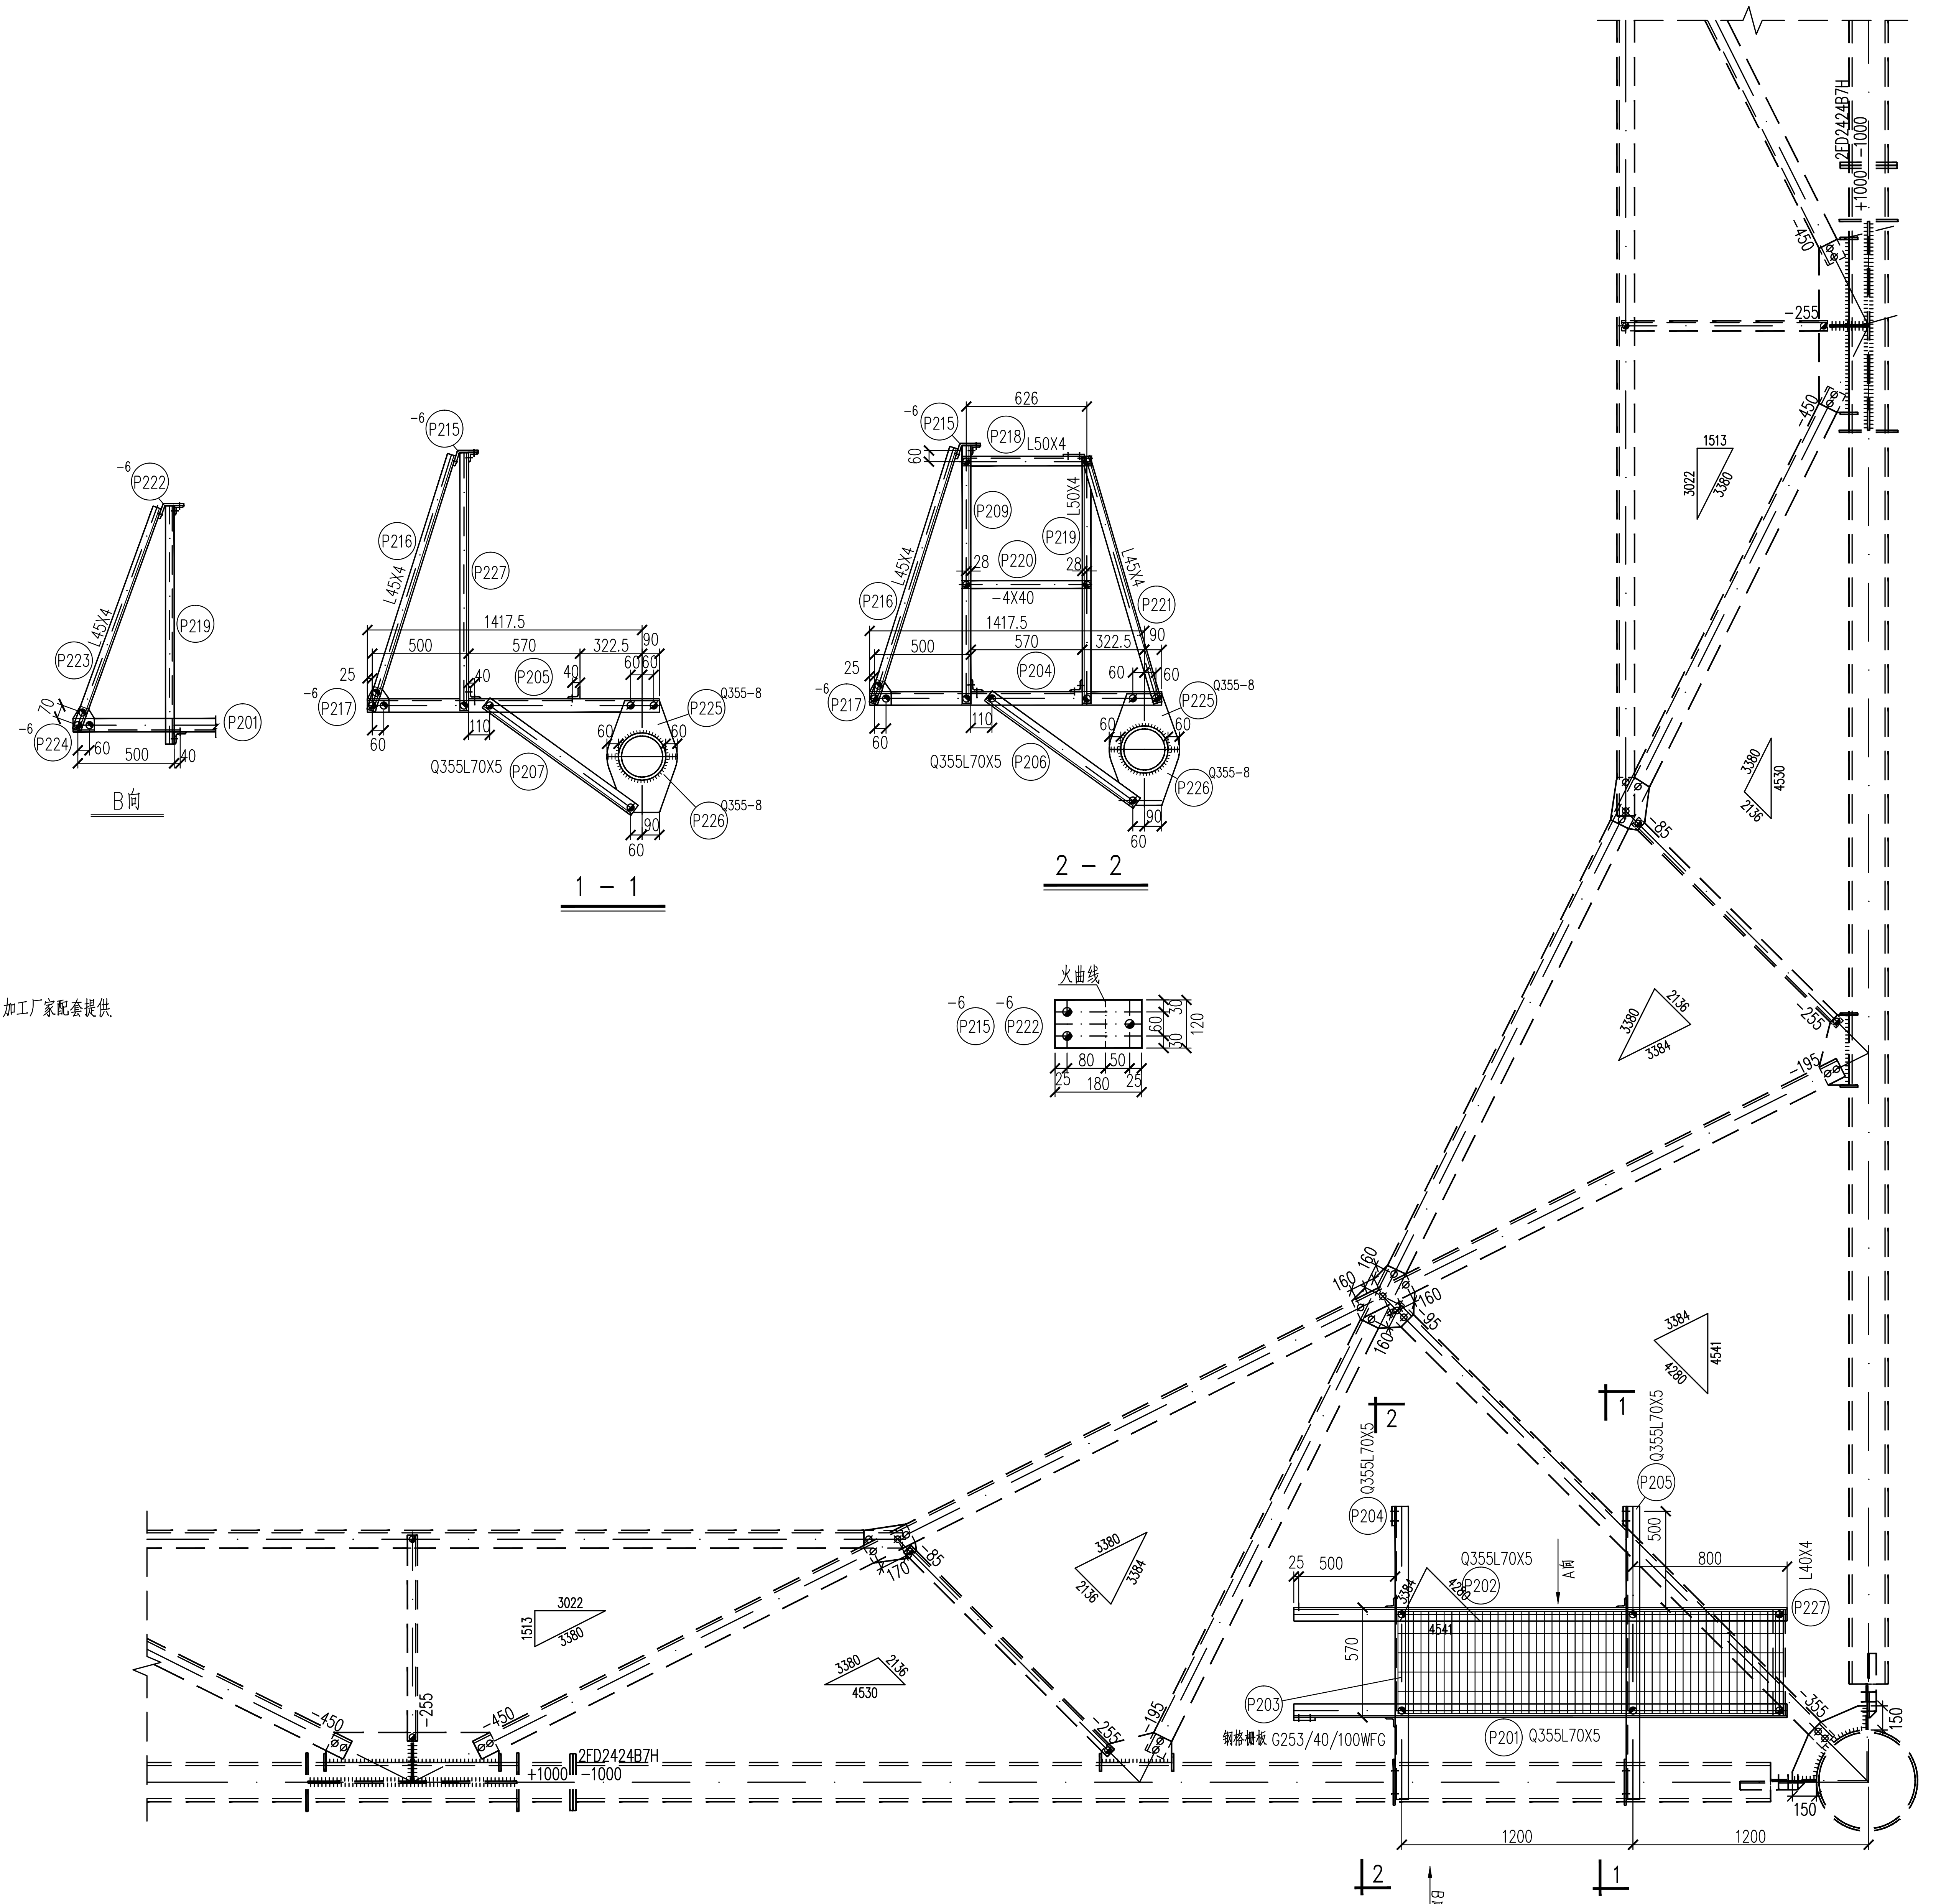

B向

1 - 1

2 - 2

平台及钢格板标准说明:

1. 此段横隔面平台对角布置.
2. 钢格板参考冶金行业标准(YB/T 4001.1-2019)《钢格栅板及配套件》第一部分: 钢格栅板.
3. 钢格栅板长度为总长,加工放样时可用标准件拼装..
4. 钢格板用专用的安装夹具固定,每件钢格板安装夹的数量不少于4个且安装夹间距不大于2m,安装夹由加工厂家配套提供.
5. 钢格板的承载扁钢须搁置在角钢梁上..

说明:平台要结合塔身一起放样。各细部尺寸以实际加工放样为准.

## 构 件 明 细 表

| 编号 | 规 格 | 长 度 (mm) | 数量 | 重 量(kg) |  | 备 注 |
|---|---|---|---|---|---|---|
|  |  |  |  | 一 件 | 小 计 |  |
| P201 | Q355L70X5 | 2560 | 2 | 13.82 | 27.6 |  |
| P202 | Q355L70X5 | 2560 | 2 | 13.82 | 27.6 |  |
| P203 | G253/40/100WFG | 530X2000 | 2 | 26.50 | 53.0 | 带夹具重量 |
| P204 | Q355L70X5 | 1521 | 2 | 8.21 | 16.4 |  |
| P205 | Q355L70X5 | 1521 | 2 | 8.21 | 16.4 |  |
| P206 | Q355L70X5 | 977 | 2 | 4.71 | 9.4 |  |
| P207 | Q355L70X5 | 977 | 2 | 5.27 | 10.5 |  |
| P208 | L50X4 | 1250 | 2 | 3.82 | 7.6 |  |
| P209 | L50X4 | 1320 | 2 | 4.04 | 8.1 |  |
| P210 | L45X4 | 973 | 2 | 2.66 | 5.3 |  |
| P211 | L45X4 | 1230 | 2 | 3.37 | 6.7 |  |
| P212 | -4X40 | 1850 | 2 | 2.32 | 4.6 |  |
| P213 | -4X40 | 1250 | 2 | 1.57 | 3.1 |  |
| P214 | L50X4 | 2000 | 2 | 6.12 | 12.2 |  |
| P215 | -6X120 | 180 | 4 | 1.02 | 4.1 | 火曲 |
| P216 | L45X4 | 1390 | 4 | 3.80 | 15.2 |  |
| P217 | -6X110 | 133 | 4 | 0.69 | 2.8 |  |
| P218 | L50X4 | 676 | 2 | 2.07 | 4.1 |  |
| P219 | L50X4 | 1260 | 2 | 3.85 | 7.7 |  |
| P220 | -4X40 | 676 | 2 | 0.85 | 1.7 |  |
| P221 | L45X4 | 1331 | 2 | 3.64 | 7.3 |  |
| P222 | -6X120 | 180 | 2 | 1.02 | 2.0 | 火曲 |
| P223 | L45X4 | 1228 | 2 | 3.36 | 6.7 |  |
| P224 | -6X110 | 133 | 2 | 0.69 | 1.4 |  |
| P225 | Q355-8X340 | 290 | 4 | 6.19 | 24.8 |  |
| P226 | Q355-8X340 | 290 | 4 | 6.19 | 24.8 |  |
| P227 | L40X4 | 540 | 2 | 1.31 | 2.6 |  |
| P228 | L50X4 | 1320 | 2 | 4.04 | 8.1 |  |
|  |  |  |  |  |  |  |
|  |  |  |  |  |  |  |
|  |  |  |  |  |  |  |
| 合 计 |  | 321.8 kg |  |  |  |  |

## 螺栓、脚钉、垫圈明细表

| 名称 | 级别 | 规 格 | 符 号 | 数量 | 重量(kg) | 备 注 |
|---|---|---|---|---|---|---|
| 螺栓 | 6.8级 | M16X45 | ⊘ | 92 | 15.5 |  |
|  |  | M16X55 | ⊘ | 18 | 3.3 |  |
|  |  |  |  |  |  |  |
|  |  |  |  |  |  |  |
| 脚钉 |  |  | ⊖ ⊣ |  |  |  |
|  |  |  |  |  |  |  |
|  |  |  |  |  |  |  |
| 垫圈 | Q235 |  | 规格X个数 |  |  |  |
|  |  |  |  |  |  |  |
| 合 计 |  |  | 18.8 kg |  |  |  |

| 山东电力工程咨询院有限公司 |  |  |  | 浙江特高压交流环网工程线路 工程 | 施工图 | 设计阶段 |
|---|---|---|---|---|---|---|
| 批 准 | 雷强 | 校 核 | 马一丹 | SZ27102A双回路直线塔<br>平台结构图 | P2 |  |
| 审 核 | 高锡鹏 |  |  |  |  |  |
|  |  | 设计/勘测 | 潘胜光 |  |  |  |
| 比 例 | 1:25 | 日 期 | 2026年 08月 | 图 号 37-SA36901S-T0121-155 | 版本 |  |