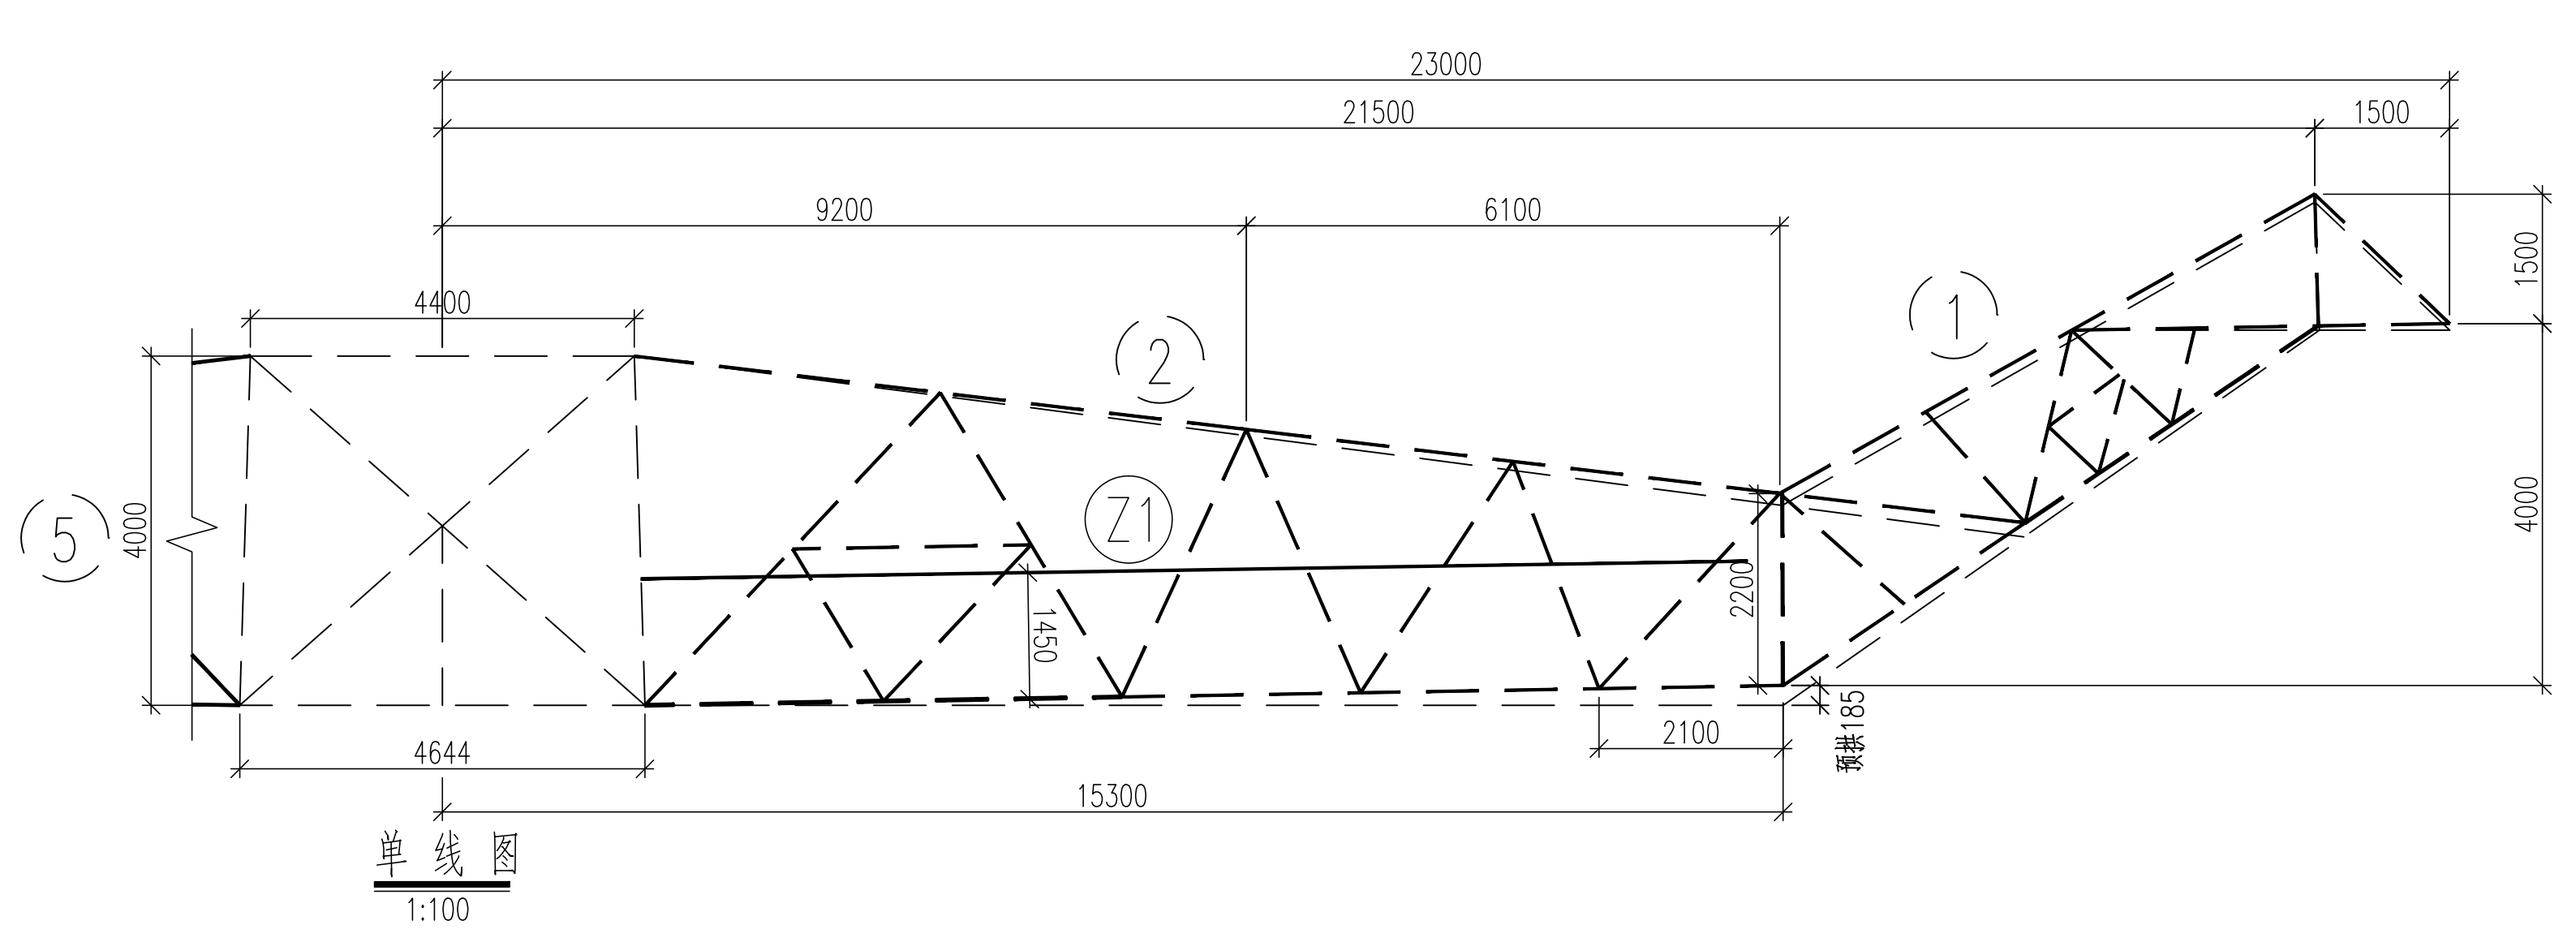
单线图
1:100

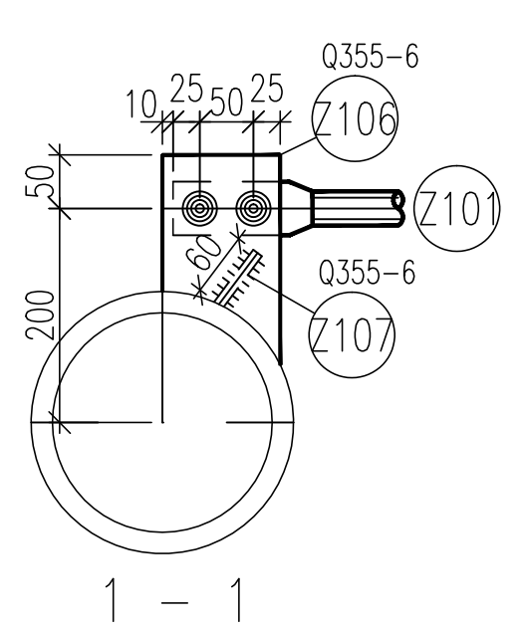
1 – 1
1:10

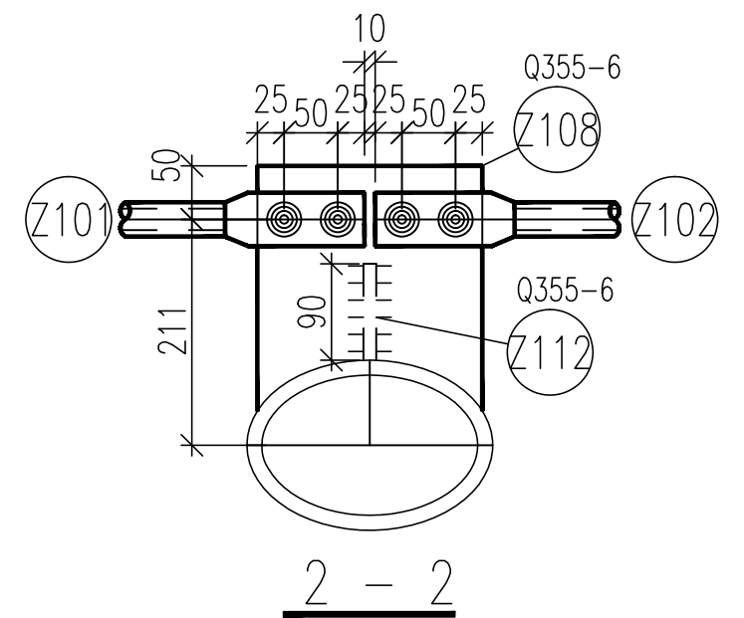
2 – 2
1:10

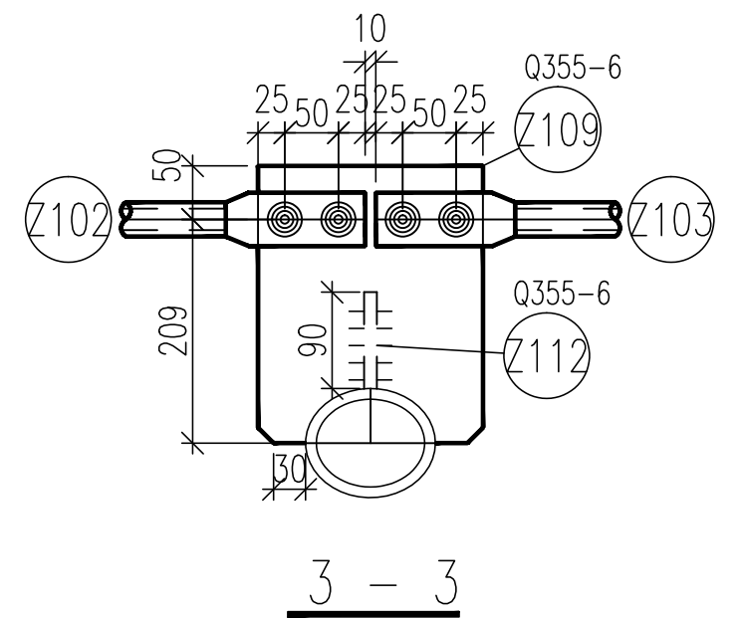
3 – 3
1:10

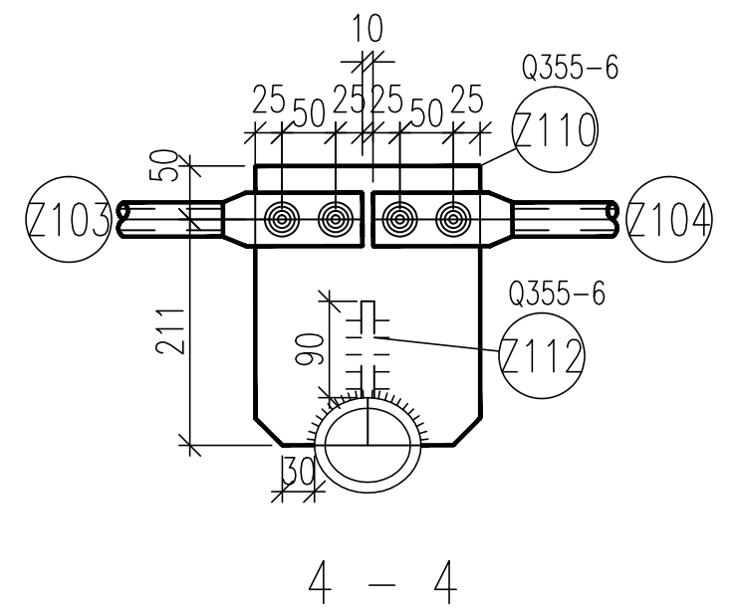
4 – 4
1:10

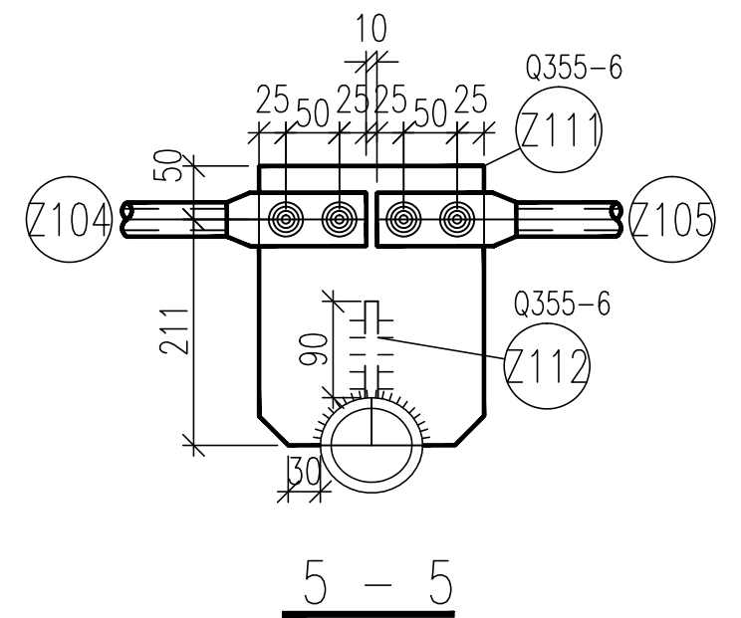
5 – 5
1:10

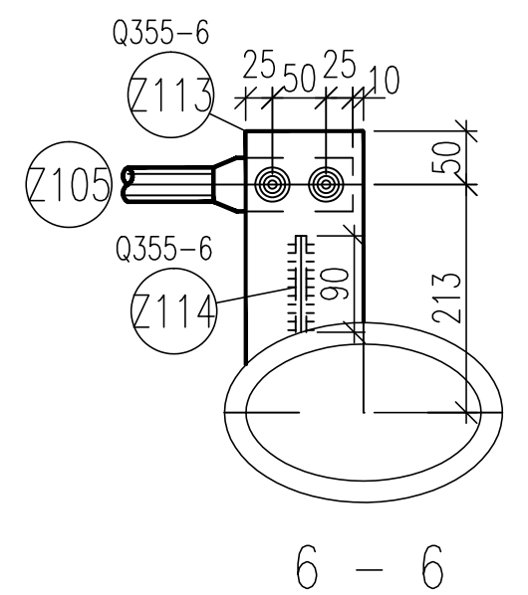
6 – 6
1:10

## 螺栓、脚钉、垫圈明细表

| 名称 | 级别 | 规格 | 符号 | 数量 | 重量(kg) | 备注 |
|---|---|---|---|---|---|---|
| 螺栓 | 6.8级 | M12X45 | ◎ | 40 | 3.9 | |
| | | M16X45 | ⊘ | 104 | 17.5 | |
| | | M16X55 | ⊘ | 48 | 8.9 | |
| 脚钉 | | | | | | |
| | | | | | | |
| | | | | | | |
| 垫圈 | Q235 | | 规格X个数 | | | |
| | | | | | | |
| 合计 | | | 30.3 kg | | | |

## 构件明细表

| 编号 | 规格 | 长度(mm) | 数量 | 重量(kg) 一件 | 重量(kg) 小计 | 备注 |
|---|---|---|---|---|---|---|
| Z101 | Q355ø38X4 | 1425 | 2 | 4.78 | 9.6 | 两端压扁 |
| Z102 | Q355ø38X4 | 3207 | 2 | 10.76 | 21.5 | 两端压扁 |
| Z103 | Q355ø38X4 | 2957 | 2 | 9.92 | 19.8 | 两端压扁 |
| Z104 | Q355ø38X4 | 2803 | 2 | 9.40 | 18.8 | 两端压扁 |
| Z105 | Q355ø38X4 | 1954 | 2 | 6.55 | 13.1 | 两端压扁 |
| Z106 | Q355-6X110 | 190 | 2 | 0.98 | 2.0 | |
| Z107 | Q355-6X60 | 60 | 2 | 0.17 | 0.3 | |
| Z108 | Q355-6X210 | 229 | 2 | 2.27 | 4.5 | |
| Z109 | Q355-6X210 | 259 | 2 | 2.56 | 5.1 | |
| Z110 | Q355-6X210 | 261 | 2 | 2.58 | 5.2 | |
| Z111 | Q355-6X210 | 261 | 2 | 2.58 | 5.2 | |
| Z112 | Q355-6X90 | 60 | 8 | 0.25 | 2.0 | |
| Z113 | Q355-6X110 | 215 | 2 | 1.11 | 2.2 | |
| Z114 | Q355-6X90 | 60 | 2 | 0.25 | 0.5 | |
| Z115 | Q355L70X5 | 6190 | 2 | 33.41 | 66.8 | |
| Z116 | Q355L70X5 | 6190 | 2 | 33.41 | 66.8 | |
| Z117 | Q355L70X5 | 5800 | 2 | 31.30 | 62.6 | |
| Z118 | Q355L70X5 | 5800 | 2 | 31.30 | 62.6 | |
| Z119 | Q355L80X6 | 260 | 4 | 1.92 | 7.7 | 清根 |
| Z120 | G253/40/100WFG | 500X12000 | 2 | 150.00 | 300.0 | 重量含夹具 |
| Z121 | L40X4 | 540 | 12 | 1.31 | 15.7 | |
| Z122 | Q355L63X5 | 982 | 16 | 4.74 | 75.8 | |
| Z123 | Q355L63X5 | 888 | 16 | 4.28 | 68.5 | 切角 |
| Z124 | Q355-8X225 | 393 | 8 | 5.55 | 44.4 | 坡口电焊 |
| Z125 | Q355-8X225 | 393 | 8 | 5.55 | 44.4 | 坡口电焊 |
| Z126 | Q355-8X225 | 365 | 8 | 5.16 | 41.3 | 坡口电焊 |
| Z127 | Q355-8X225 | 365 | 8 | 5.16 | 41.3 | 坡口电焊 |
| | | | | | | |
| | | | | | | |
| | | | | | | |
| 合计 | | 1007.7 kg | | | | |

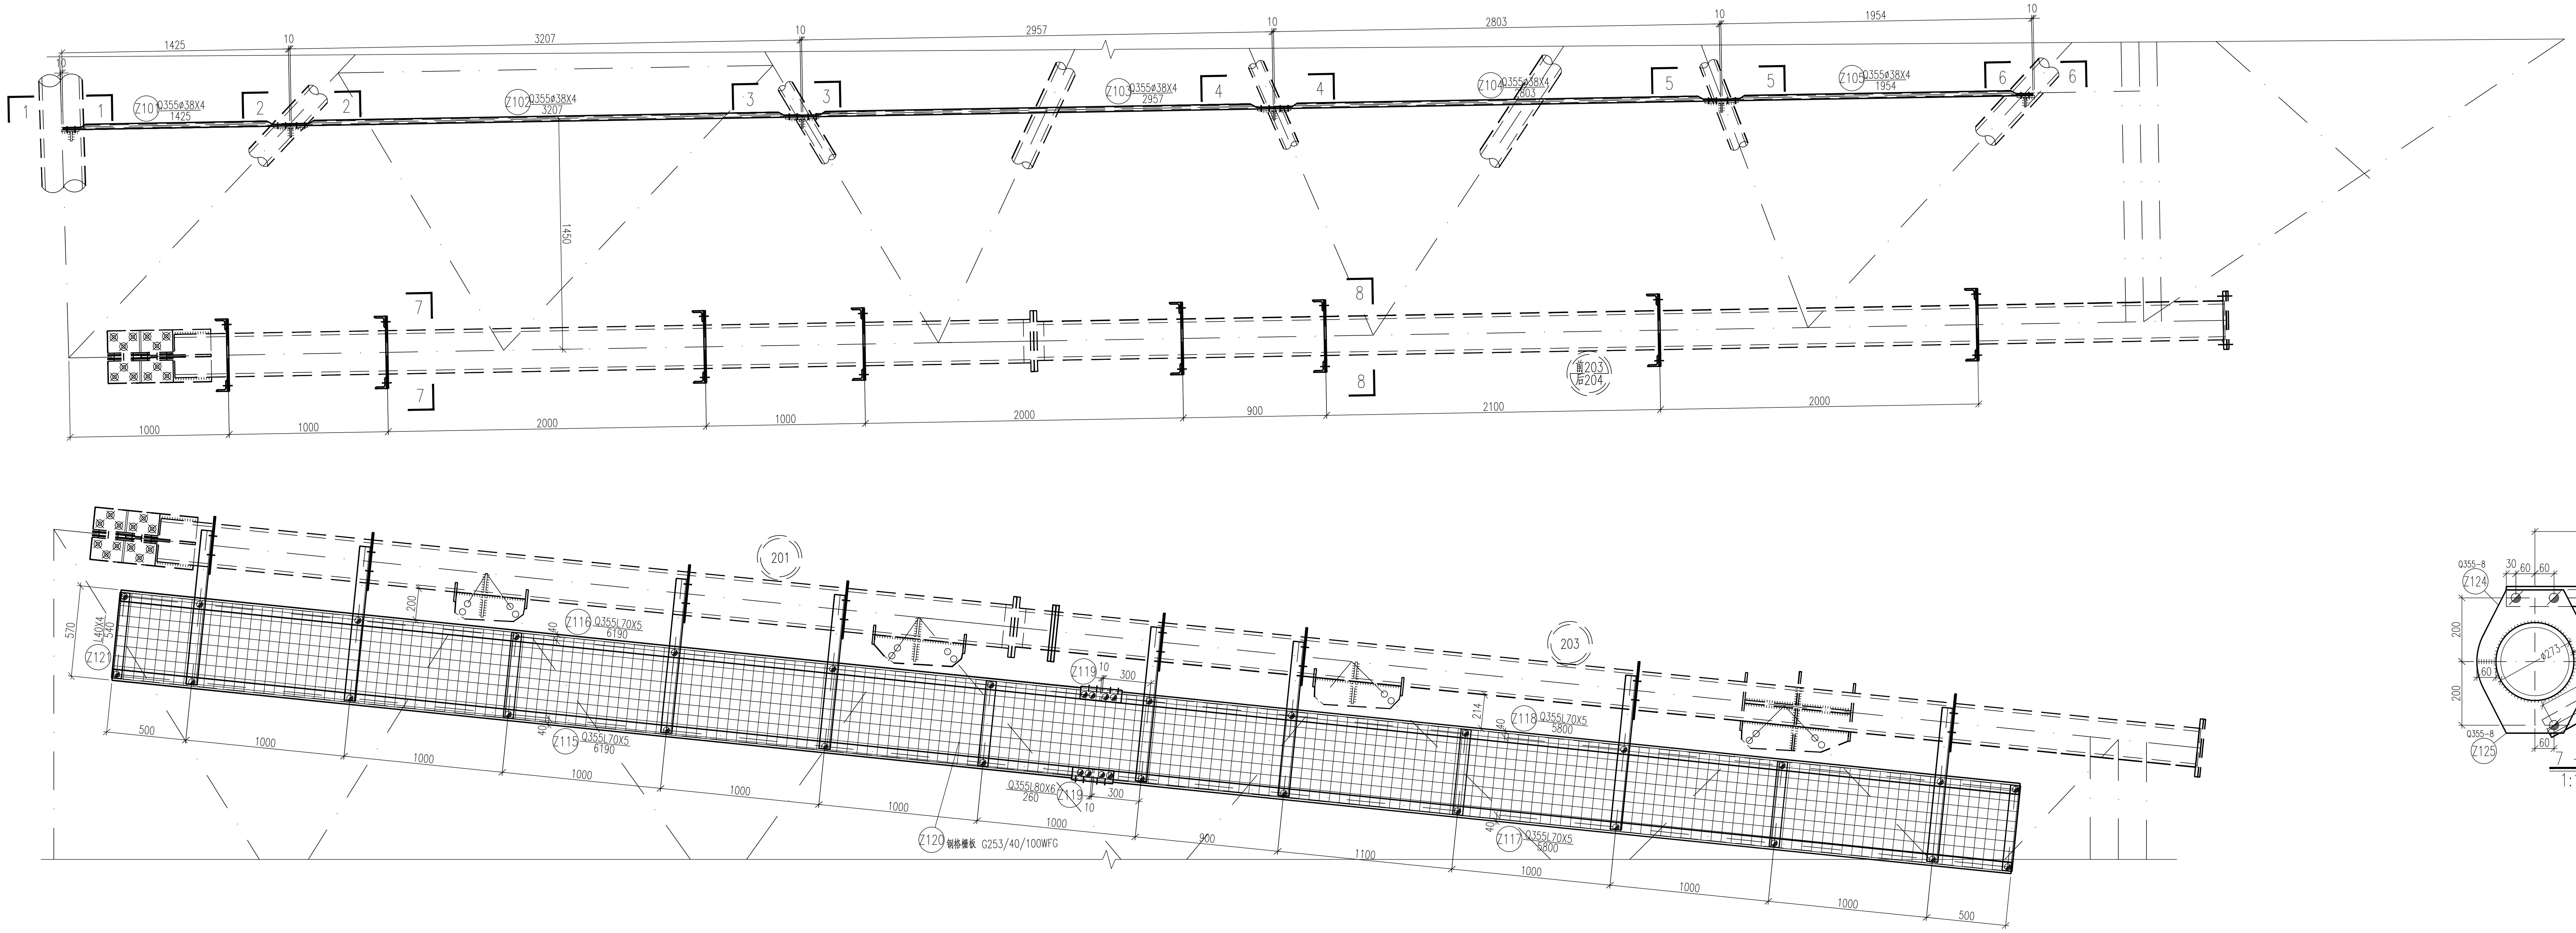

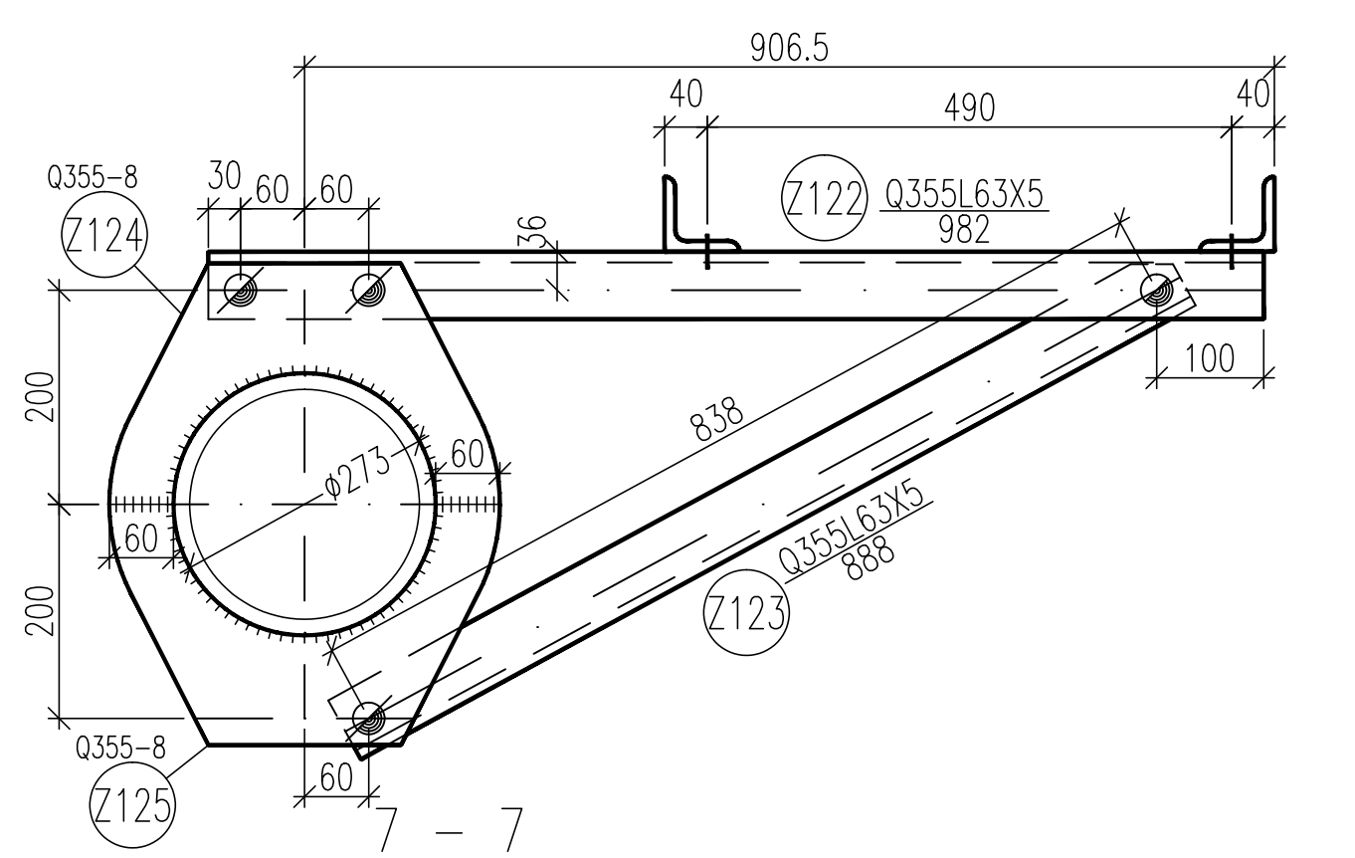
7 – 7
1:10

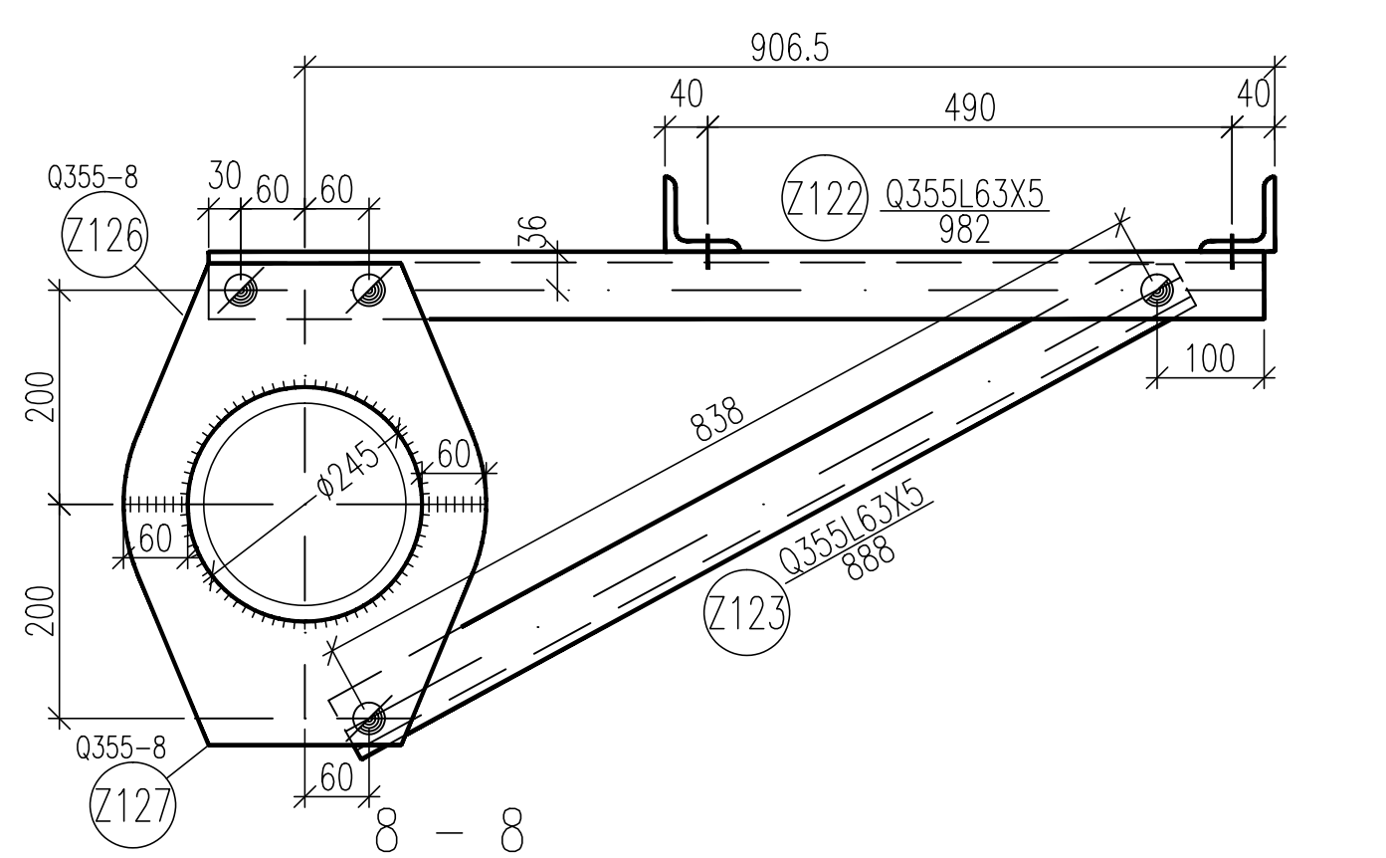
8 – 8
1:10

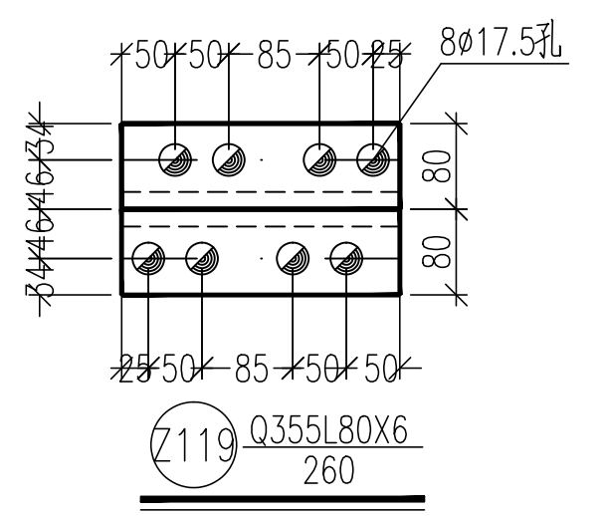
Z119 Q355L80X6
260
1:10

钢格板说明:

1.钢格板按照冶金行业标准(YB/T 4001.1-2019)《钢格栅板及配套件》第一部分:钢格栅板.
2.钢格板用专用的安装夹具固定,每件钢格板安装夹的数量不少于4个且安装夹间距不大于2m,安装夹由加工厂家配套提供.
3.钢格板的承载扁钢须搁置在角钢梁上.
4.左右横担走道均在同侧布置。
5.走道设置在爬梯侧。
6.走道扶手位于走道上方1200mm。

| | | | | | | | |
|---|---|---|---|---|---|---|---|
| 山东电力工程咨询院有限公司 | | | | 浙江特高压交流环网工程线路 工程 | | 施工图 | 设计阶段 |
| 批准 | | 校核 | 马一丹 | SZK31102A直线塔<br>走道结构图 | Z1 | | |
| 审核 | 高锡鹏 | | | | | | |
| | | 设计/勘测 | 潘旭光 | | | | |
| 比例 | | 日期 | 2026年 08月 | 图号 | 37-SA36901S-T0121-157 | 版本 | |