




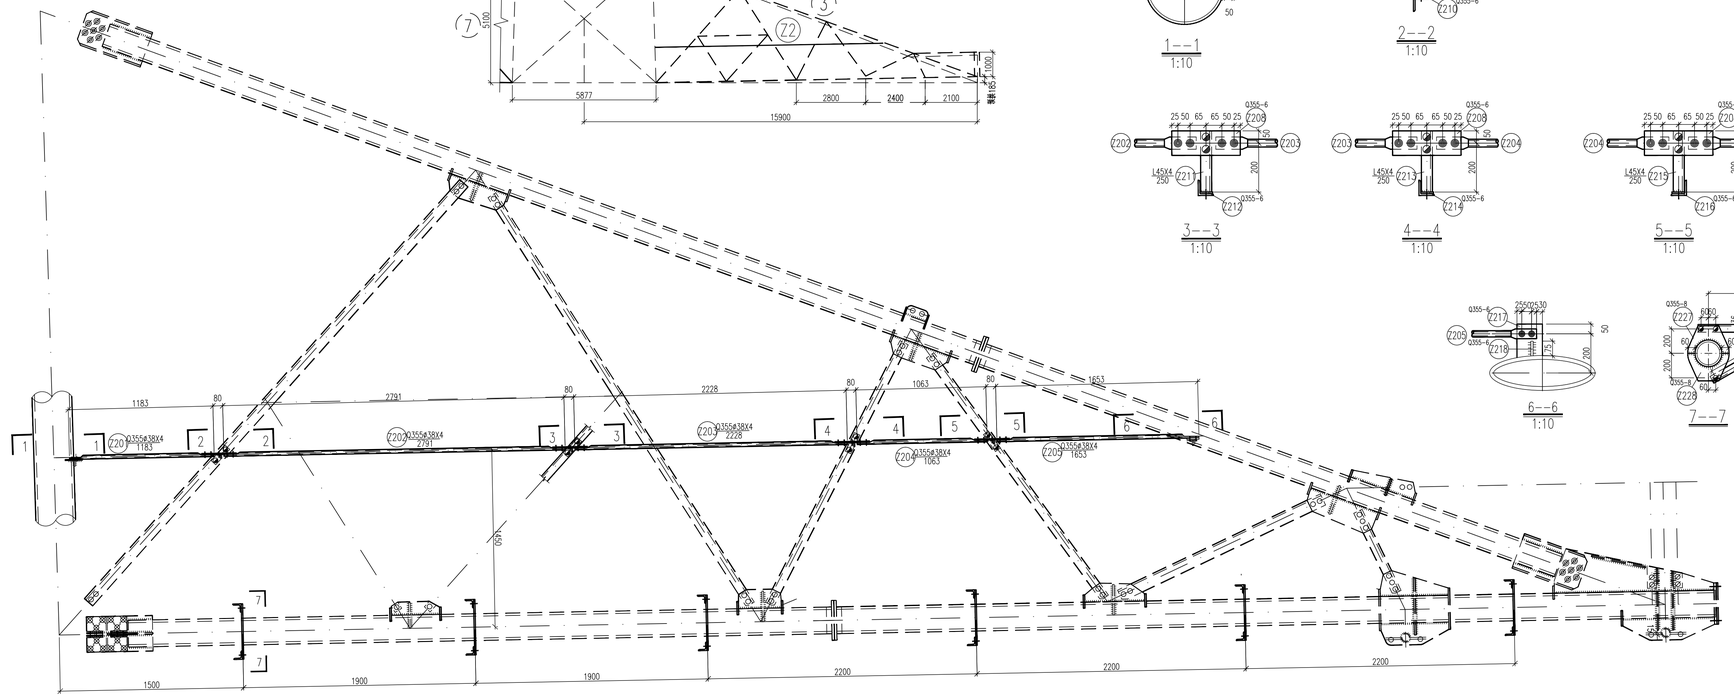


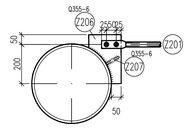


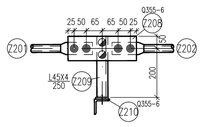

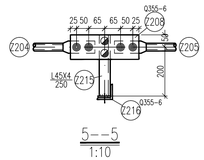

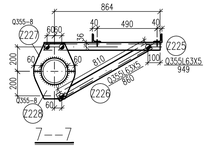

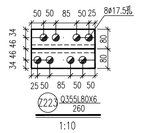

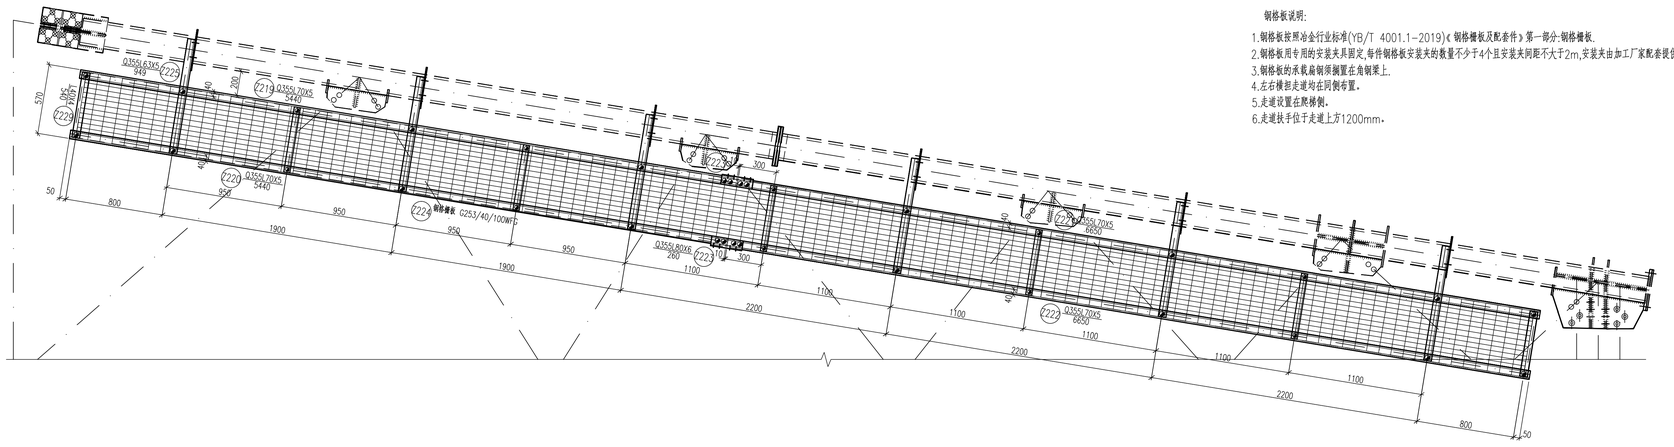

钢格板说明:

1.钢格板按照冶金行业标准(YB/T 4001.1-2019)《钢格栅板及配套件》第一部分:钢格栅板。
2.钢格板用专用的安装夹具固定,每件钢格板安装夹的数量不少于4个且安装夹间距不大于2m,安装夹由加工厂家配套提供。
3.钢格板的承载扁钢须搁置在角钢梁上。
4.左右横担走道均在同侧布置。
5.走道设置在爬梯侧。
6.走道扶手位于走道上方1200mm。

螺栓、脚钉、垫圈明细表

名称	级别	规格	符号	数量	重量(kg)	备注
螺栓	6.8级	M12X45	●	40	3.9	
		M16X45	⊘	128	21.6	
		M16X55	⊘	36	6.6	
脚钉			⊕			
垫圈	Q235		规格X个数			
合计				32.1 kg		

构件明细表

编号	规格	长度(mm)	数量	重量(kg) 一件	重量(kg) 小计	备注
Z201	Q355∞38X4	1183	2	3.97	7.9	两端压扁
Z202	Q355∞38X4	2791	2	9.36	18.7	两端压扁
Z203	Q355∞38X4	2228	2	7.47	14.9	两端压扁
Z204	Q355∞38X4	1063	2	3.57	7.1	两端压扁
Z205	Q355∞38X4	1653	2	5.54	11.1	两端压扁
Z206	Q355-6X250	165	2	1.94	3.9	
Z207	Q355-6X60	75	2	0.21	0.4	
Z208	Q355-6X100	280	8	1.32	10.6	
Z209	L45X4	250	2	0.68	1.4	焊接
Z210	Q355-6X50	200	2	0.47	0.9	
Z211	L45X4	250	2	0.68	1.4	焊接
Z212	Q355-6X50	200	2	0.47	0.9	
Z213	L45X4	250	2	0.68	1.4	焊接
Z214	Q355-6X50	200	2	0.47	0.9	
Z215	L45X4	250	2	0.68	1.4	焊接
Z216	Q355-6X50	200	2	0.47	0.9	
Z217	Q355-6X130	170	2	1.04	2.1	
Z218	Q355-6X60	75	2	0.21	0.4	
Z219	Q355L70X5	5440	2	29.36	58.7	
Z220	Q355L70X5	5440	2	29.36	58.7	
Z221	Q355L70X5	6650	2	35.89	71.8	
Z222	Q355L70X5	6650	2	35.89	71.8	
Z223	Q355L80X6	260	4	1.92	7.7	滑板
Z224	GZ53/40/100MWG	500X12090	2	151.13	302.3	重量含夹具
Z225	Q355L63X5	949	12	4.58	55.0	
Z226	Q355L63X5	860	12	4.15	49.8	切角
Z227	Q355-8X225	339	12	4.79	57.5	坡口焊接
Z228	Q355-8X225	339	12	4.79	57.5	坡口焊接
Z229	L40X4	540	14	1.31	18.3	
合计				895.4 kg		

山东电力工程咨询院有限公司				浙江特高压交流环网工程线路 工程	施工图	设计阶段
批准		校核		SZK31102A直线塔 走道结构图 Z2		
审核		设计/勘测				
比例		日期	2026年08月	图号 37-SA36901S-T0121-158	版本	