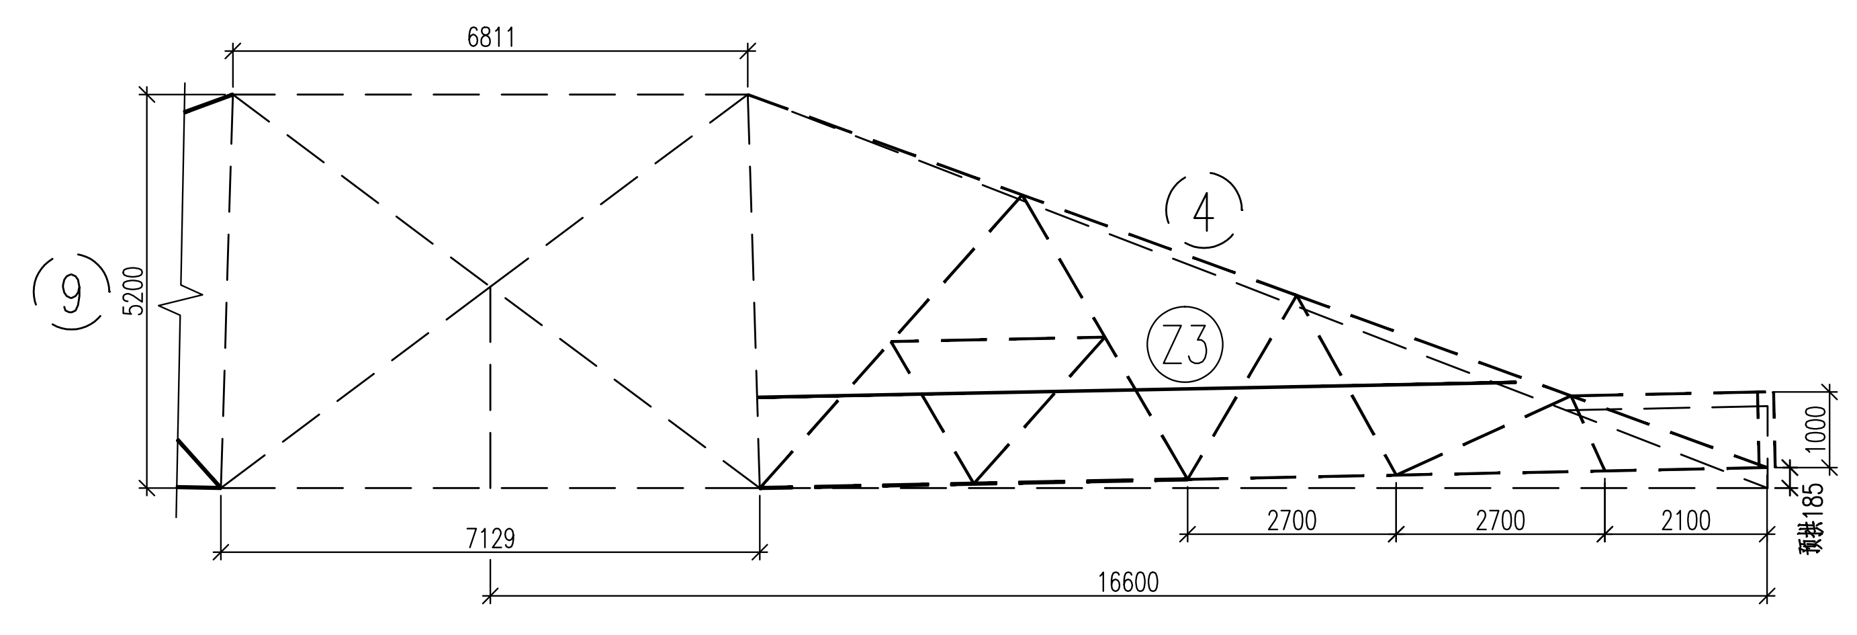

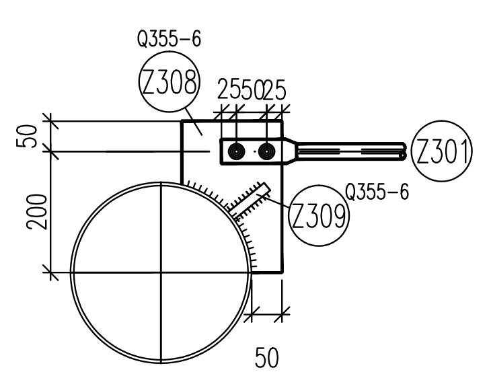

1--1
1:10

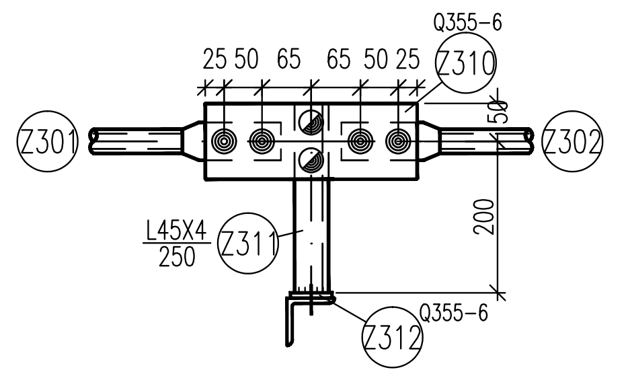

2--2
1:10

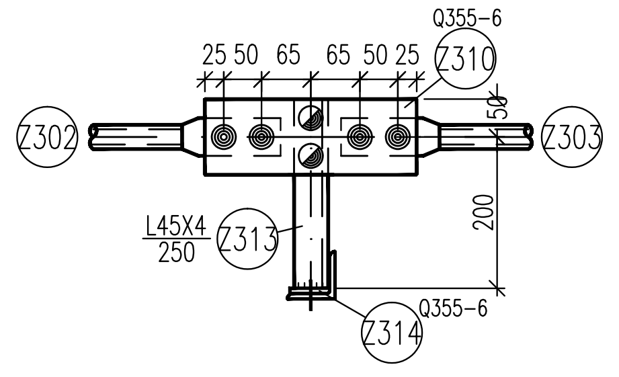

3--3
1:10

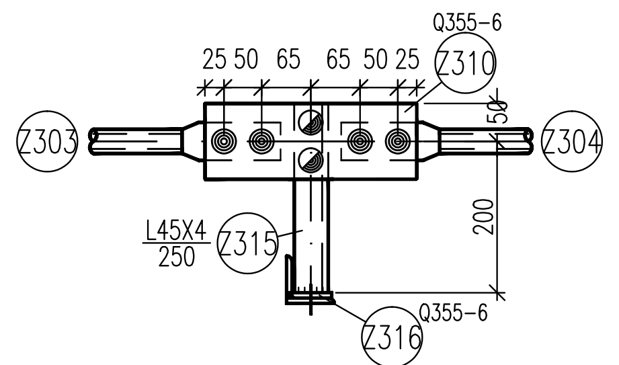

4--4
1:10

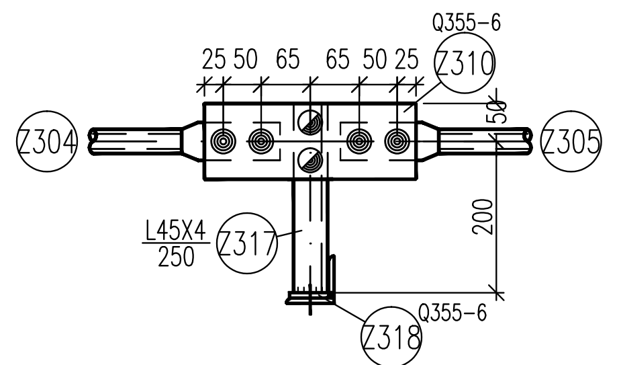

5--5
1:10

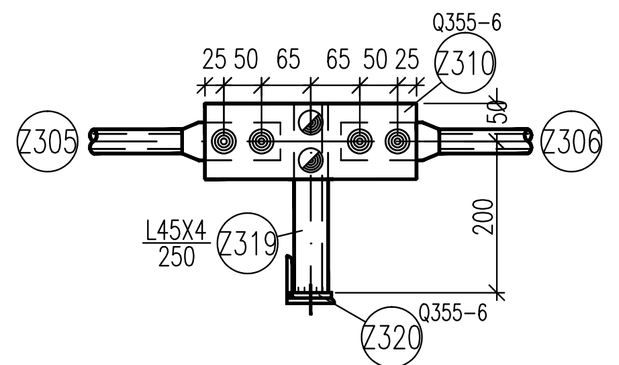

6--6
1:10

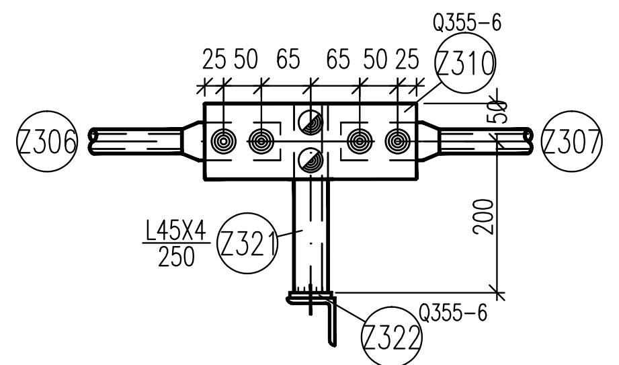

7--7
1:10

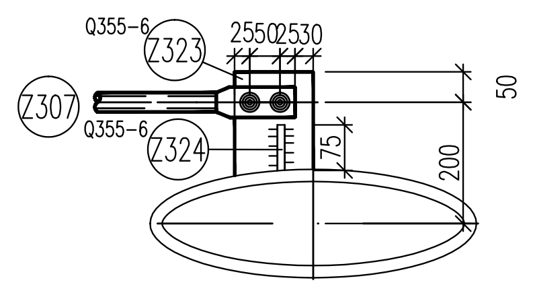

8--8
1:10

螺栓、脚钉、垫圈明细表

名称	级别	规格	符号	数量	重量(kg)	备注
螺栓	6.8级	M12X45	⊗	48	4.6	
		M16X45	⊘	120	20.2	
		M16X55	⊘	36	6.6	
脚钉			⊖			
			⊣			
垫圈	Q235		规格X个数			
合计			31.4 kg			

构件明细表

编号	规格	长度(mm)	数量	重量(kg) 一件	重量(kg) 小计	备注
Z301	Q355ø38X4	1066	2	3.58	7.2	两端压扁
Z302	Q355ø38X4	607	2	2.04	4.1	两端压扁
Z303	Q355ø38X4	2063	2	6.92	13.8	两端压扁
Z304	Q355ø38X4	621	2	2.08	4.2	两端压扁
Z305	Q355ø38X4	1597	2	5.36	10.7	两端压扁
Z306	Q355ø38X4	1051	2	3.53	7.1	两端压扁
Z307	Q355ø38X4	1885	2	6.32	12.6	两端压扁
Z308	Q355-6X250	165	2	1.94	3.9	
Z309	Q355-6X60	75	2	0.21	0.4	
Z310	Q355-6X100	280	12	1.32	15.8	
Z311	L45X4	250	2	0.68	1.4	电焊
Z312	Q355-6X50	200	2	0.47	0.9	
Z313	L45X4	250	2	0.68	1.4	电焊
Z314	Q355-6X50	200	2	0.47	0.9	
Z315	L45X4	250	2	0.68	1.4	电焊
Z316	Q355-6X50	200	2	0.47	0.9	
Z317	L45X4	250	2	0.68	1.4	电焊
Z318	Q355-6X50	200	2	0.47	0.9	
Z319	L45X4	250	2	0.68	1.4	电焊
Z320	Q355-6X50	200	2	0.47	0.9	
Z321	L45X4	250	2	0.68	1.4	电焊
Z322	Q355-6X50	200	2	0.47	0.9	
Z323	Q355-6X130	170	2	1.04	2.1	
Z324	Q355-6X60	75	2	0.21	0.4	
Z325	Q355L70X5	6590	2	35.57	71.1	
Z326	Q355L70X5	6590	2	35.57	71.1	
Z327	Q355L70X5	5500	2	29.68	59.4	
Z328	Q355L70X5	5500	2	29.68	59.4	
Z329	Q355L80X6	260	4	1.92	7.7	清根
Z330	G253/40/100WFG	500X12100	2	151.25	302.5	重量含夹具
Z331	Q355L63X5	955	12	4.61	55.3	
Z332	L40X4	540	14	1.31	18.3	
Z333	Q355L63X5	861	12	4.15	49.8	切角
Z334	Q355-8X225	339	12	4.79	57.5	坡口电焊
Z335	Q355-8X225	339	12	4.79	57.5	坡口电焊
合计		905.7 kg				

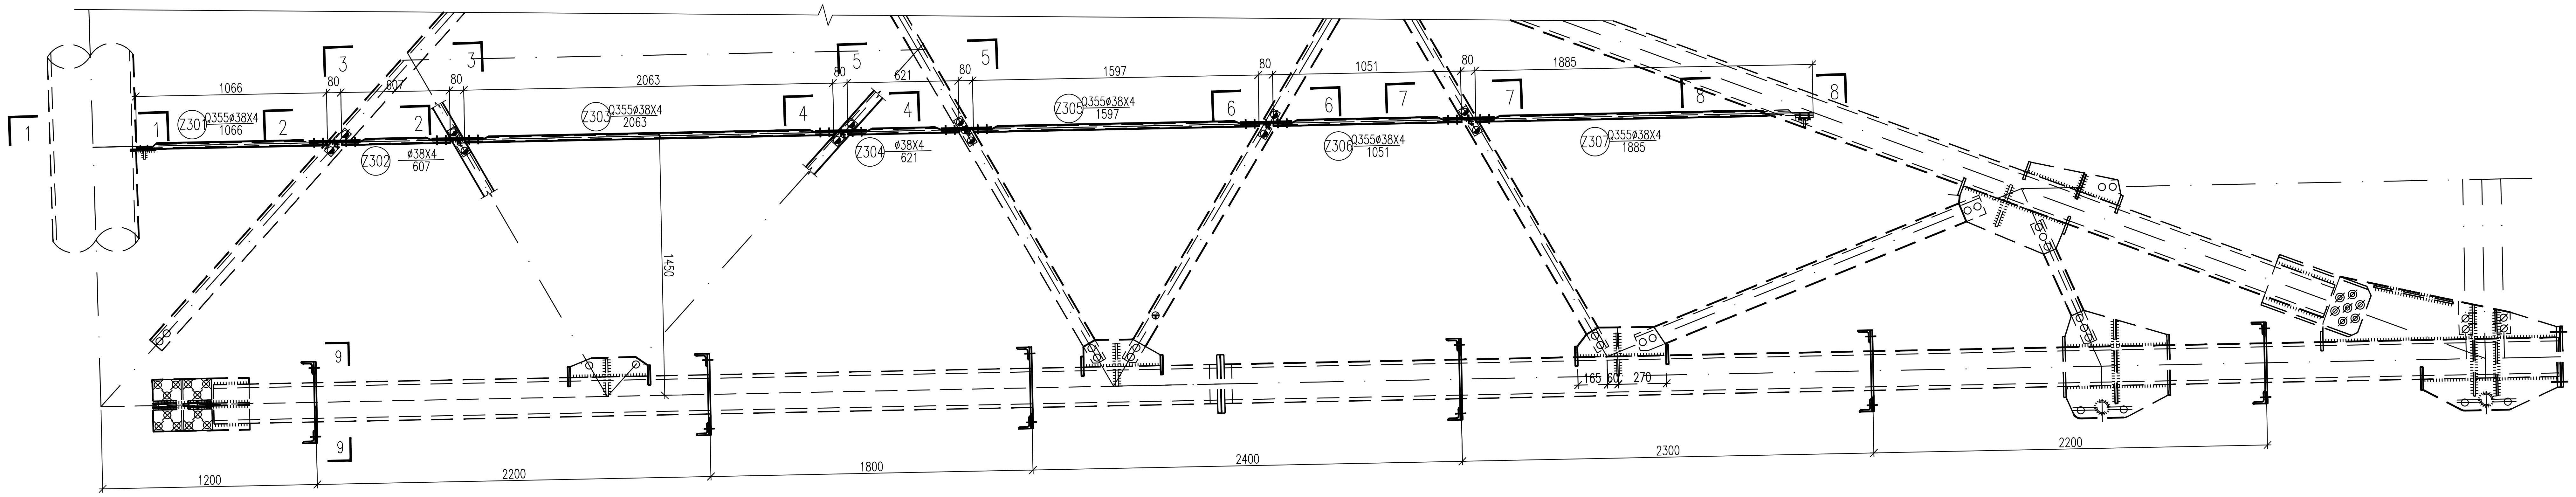

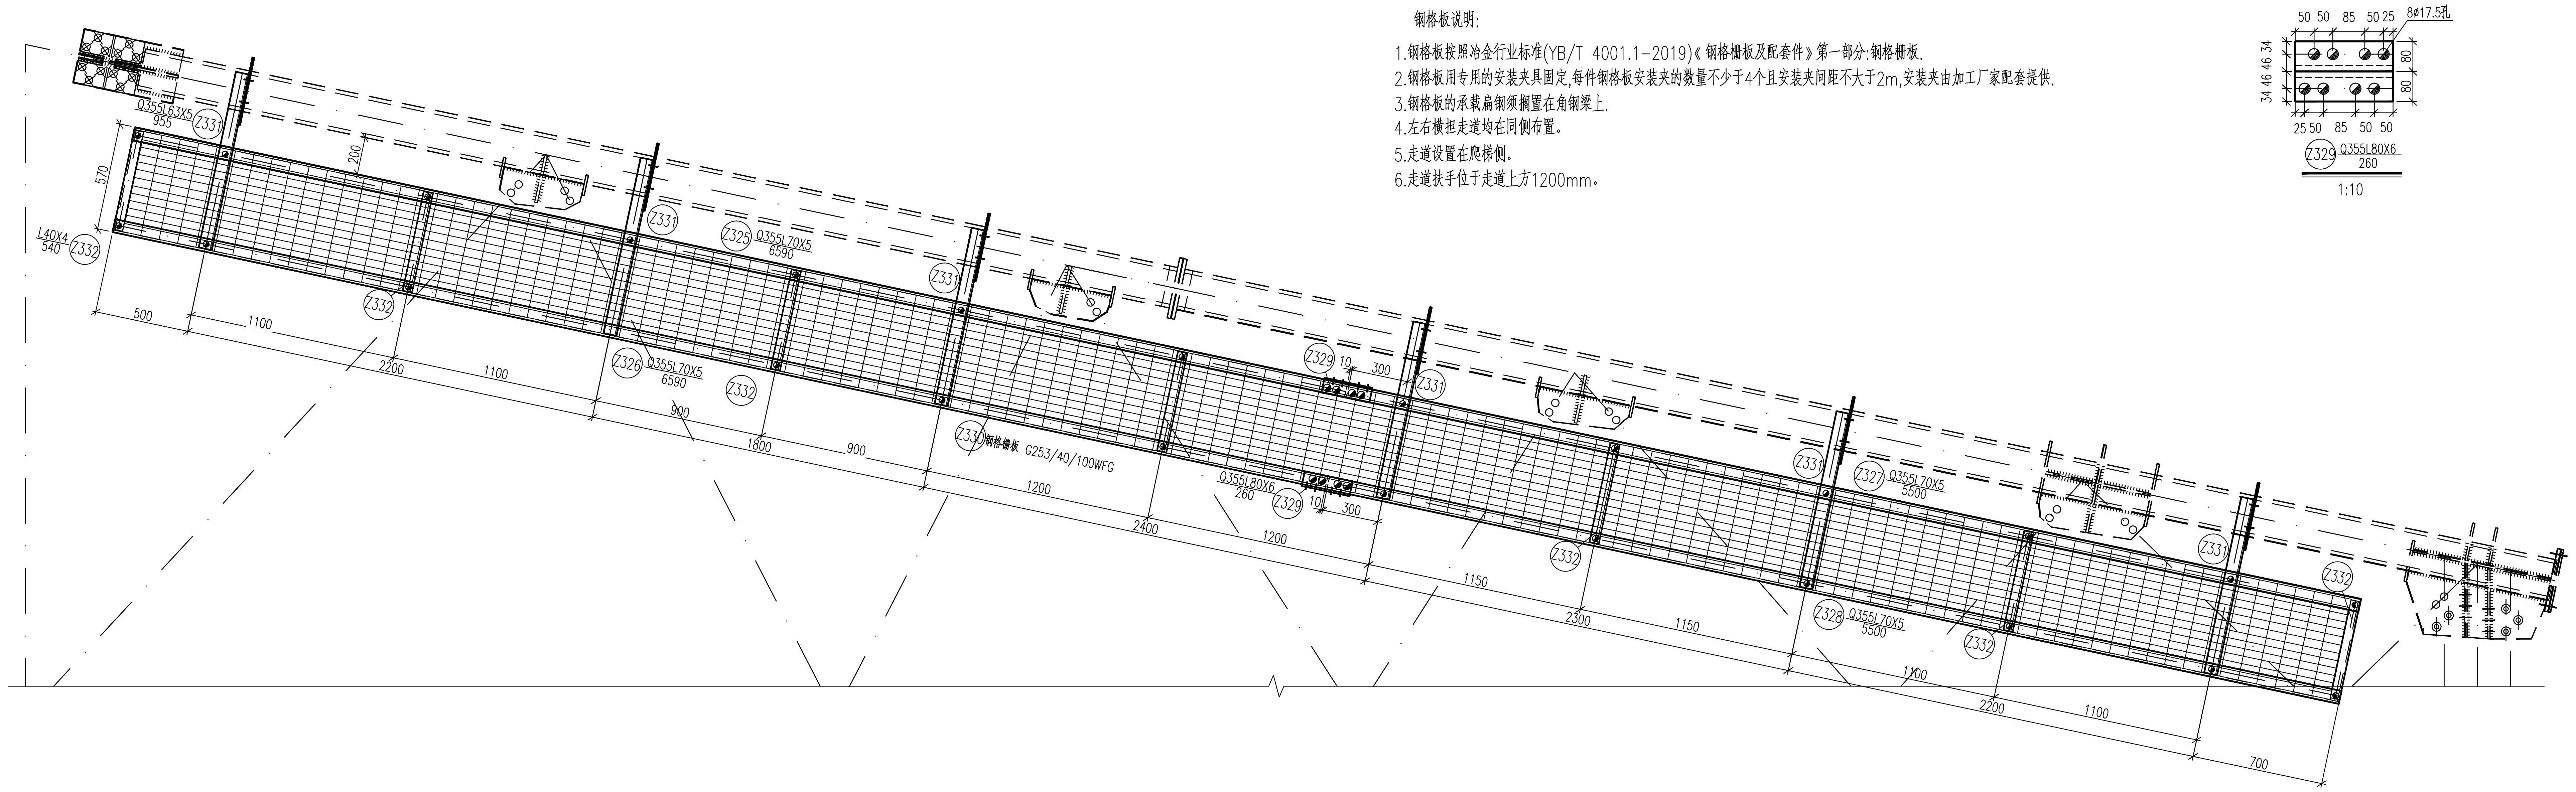

钢格板说明:

1.钢格板按照冶金行业标准(YB/T 4001.1-2019)《钢格栅板及配套件》第一部分:钢格栅板.

2.钢格板用专用的安装夹具固定,每件钢格板安装夹的数量不少于4个且安装夹间距不大于2m,安装夹由加工厂家配套提供.

3.钢格板的承载扁钢须搁置在角钢梁上.

4.左右横担走道均在同侧布置。

5.走道设置在爬梯侧。

6.走道扶手位于走道上方1200mm。

1:10

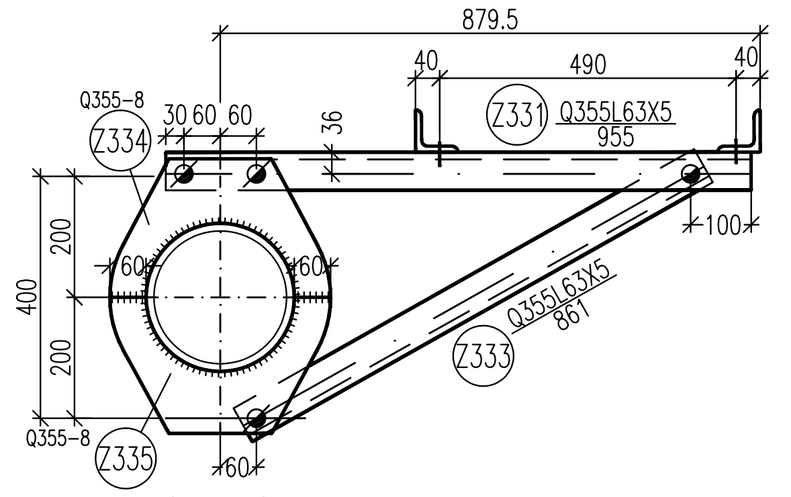

9--9
1:10

山东电力工程咨询院有限公司			浙江特高压交流环网工程线路 **工程**	施工图 **设计阶段**
批 准	雷强	**校 核** 马一丹	SZK31102A直线塔 走道结构图 Z3	
审 核	高畅鹏			
		设计/勘测		
比 例		**日 期** 2026年 08月	**图 号** 37-SA36901S-T0121-159	**版本**