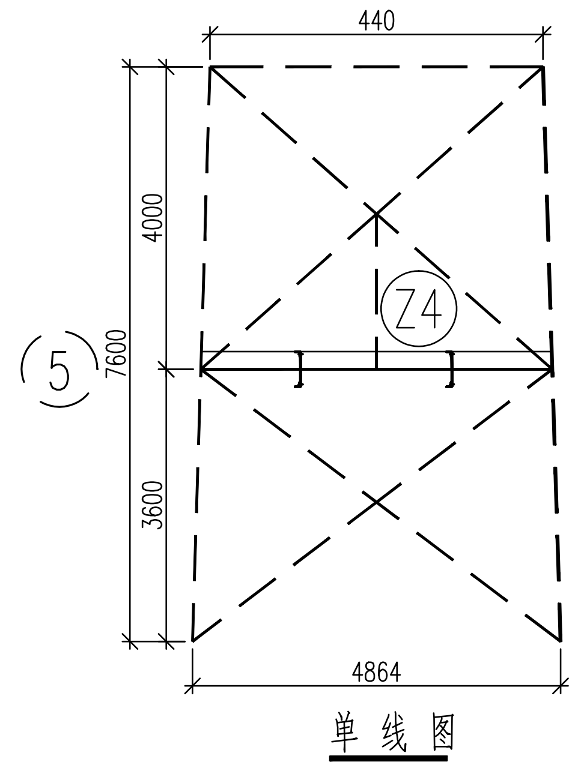

单线图
1:100

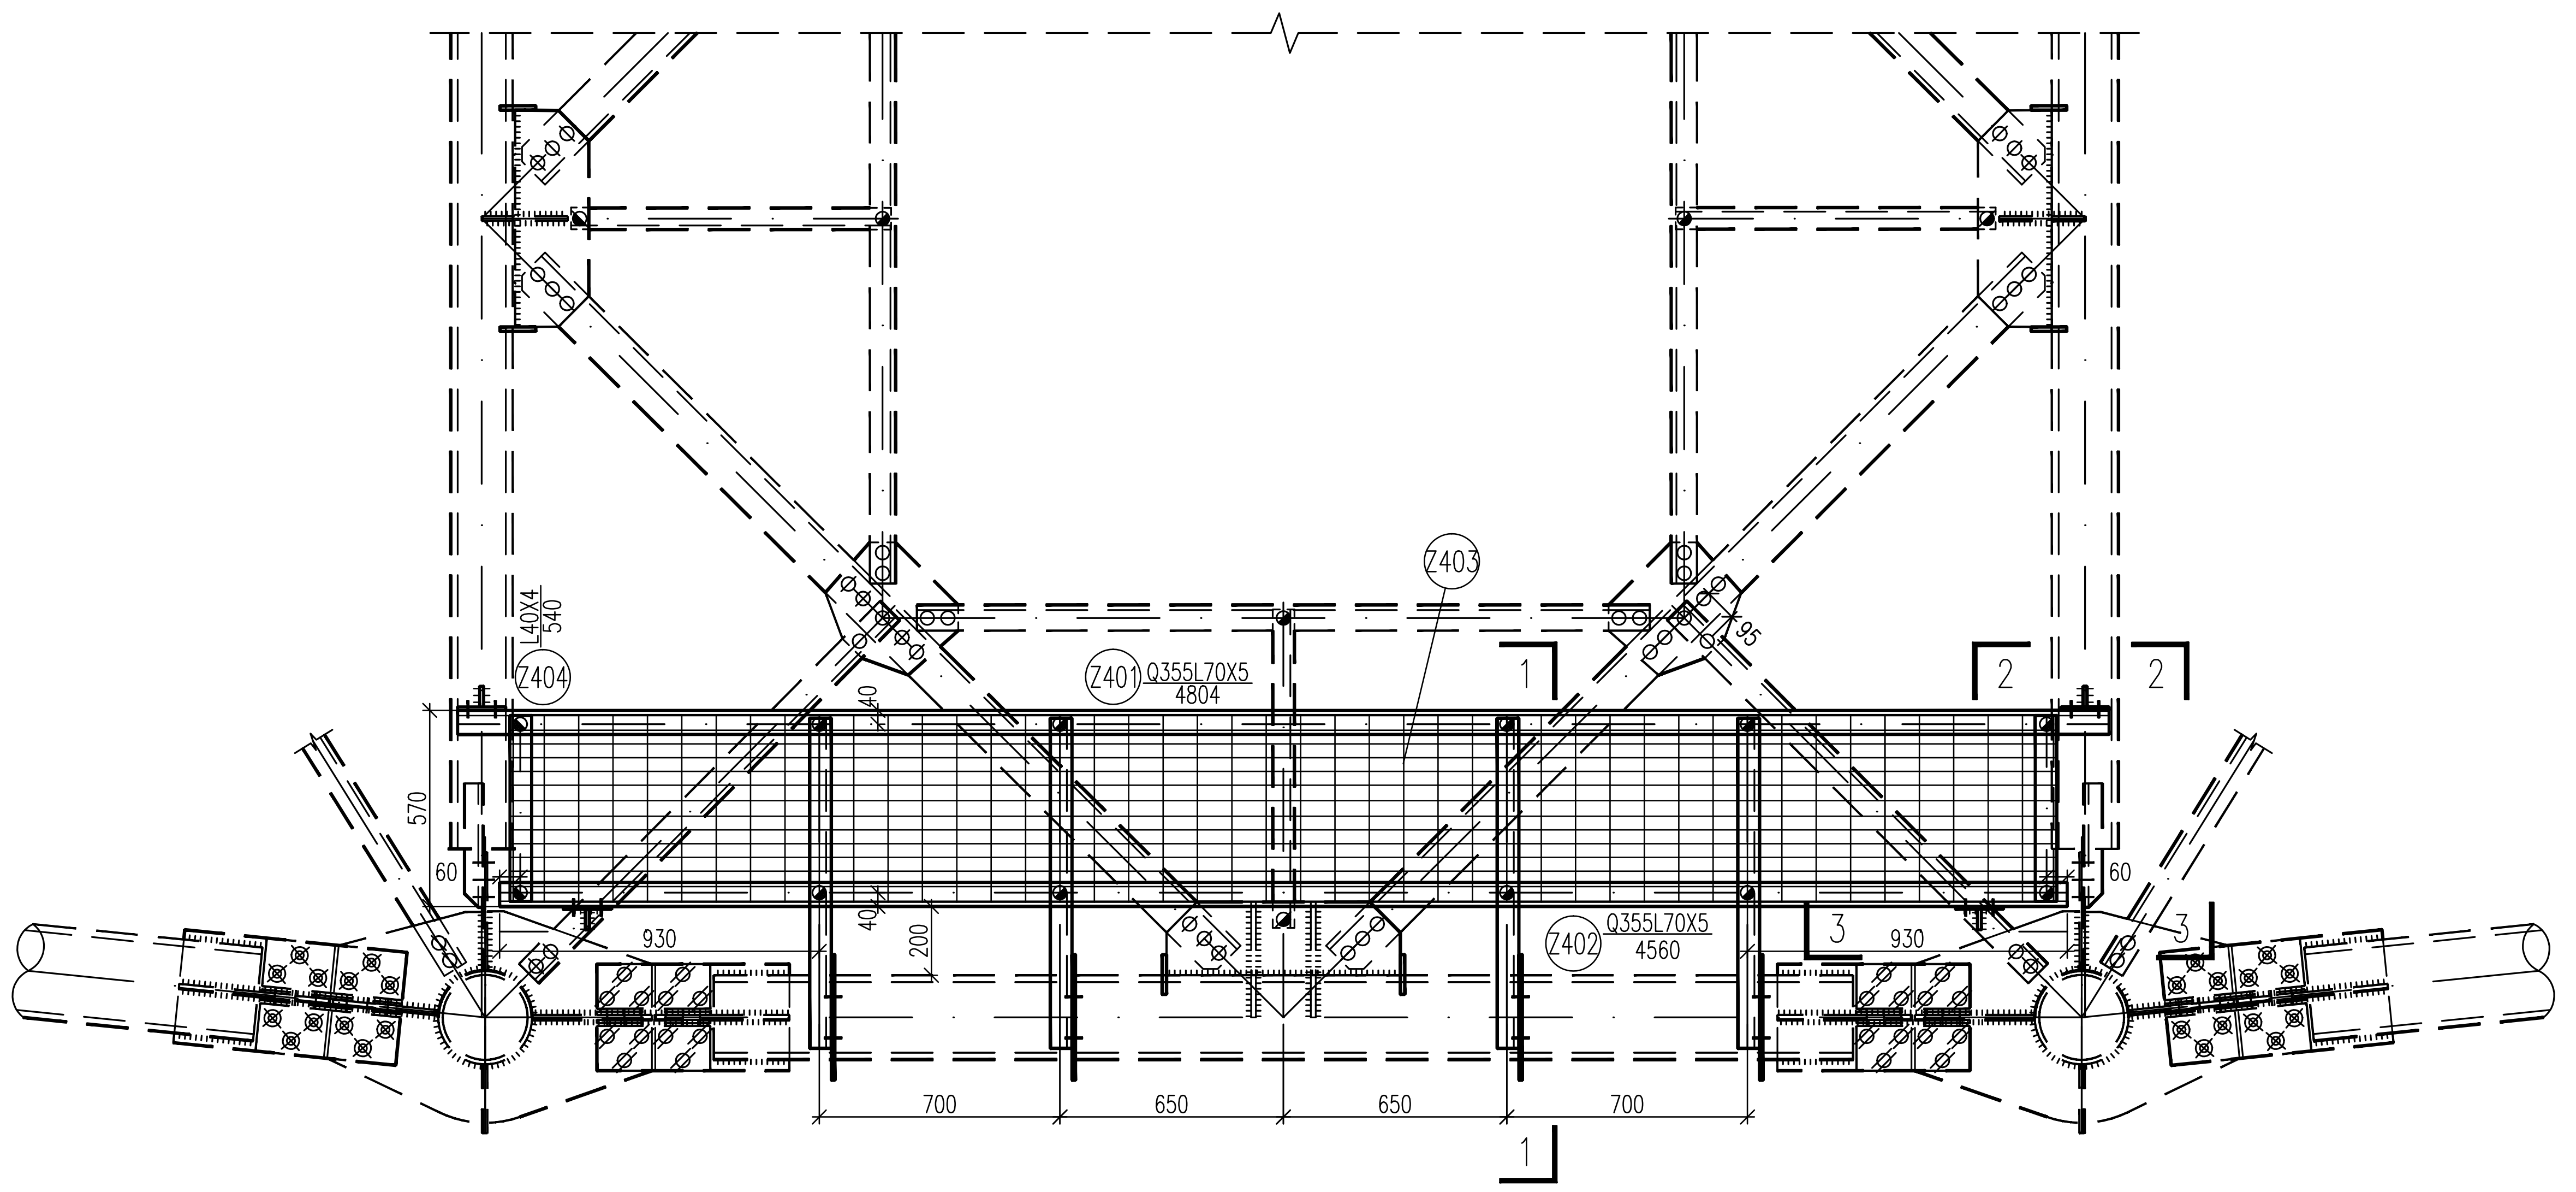

钢格板说明:

1.钢格板按照冶金行业标准(YB/T 4001.1-2019)《钢格栅板及配套件》第一部分:钢格栅板.

2.钢格板用专用的安装夹具固定,每件钢格板安装夹的数量不少于4个且安装夹间距不大于2m,安装夹由加工厂家配套提供.

3.钢格板的承载扁钢须搁置在角钢梁上.

4.走道设置在爬梯侧。

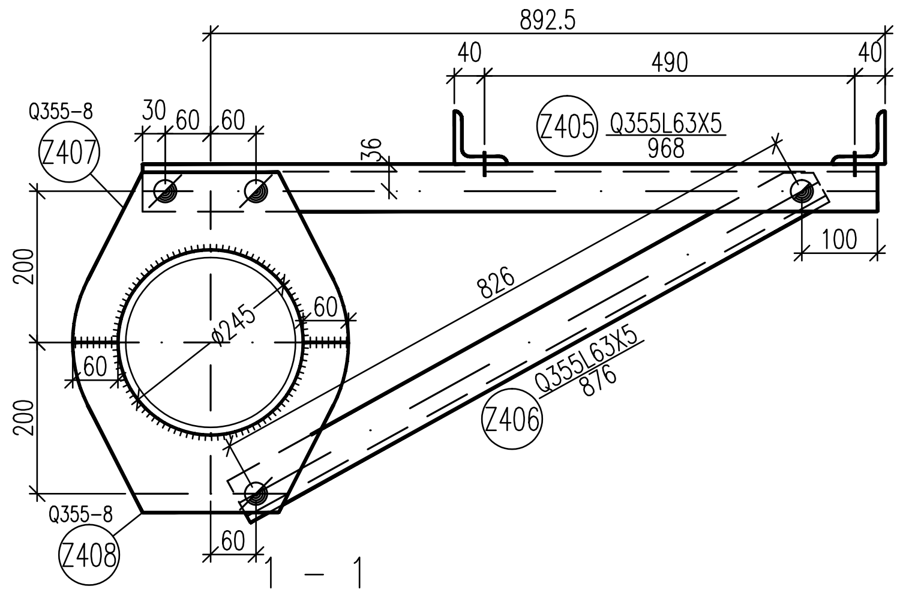

1 - 1
1:10

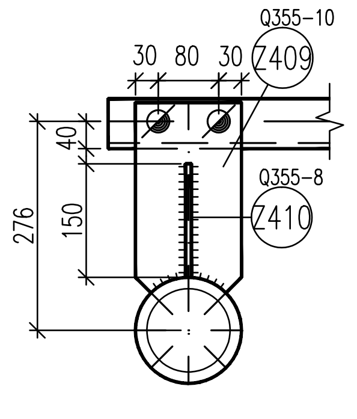

2--2
1:10

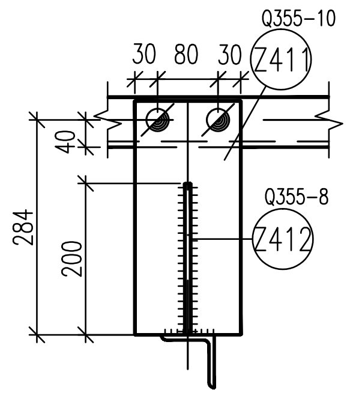

3--3
1:10

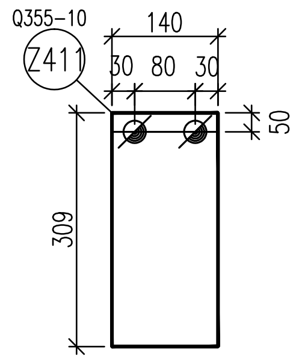

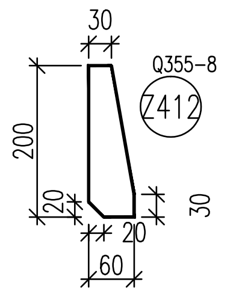

构件明细表

编号	规格	长度(mm)	数量	重量(kg) 一件	重量(kg) 小计	备注
Z401	Q355L70X5	4804	1	25.93	25.9	
Z402	Q355L70X5	4560	1	24.61	24.6	
Z403	G253/40/100WFG	500X4500	1	56.25	56.3	重量含夹具
Z404	L40X4	540	2	1.31	2.6	
Z405	Q355L63X5	968	4	4.67	18.7	
Z406	Q355L63X5	876	4	4.22	16.9	切角
Z407	Q355-8X225	365	4	5.16	20.6	坡口电焊
Z408	Q355-8X225	365	4	5.16	20.6	坡口电焊
Z409	Q355-10X140	250	2	2.75	5.5	坡口电焊
Z410	Q355-8X60	150	2	0.57	1.1	电焊
Z411	Q355-10X140	309	2	3.40	6.8	电焊
Z412	Q355-8X60	200	2	0.75	1.5	电焊
合计		201.1 kg				

螺栓、脚钉、垫圈明细表

名称	级别	规格	符号	数量	重量(kg)	备注
螺栓	6.8级	M16X45	⊘	16	2.7	
		M16X55	⊘	20	3.7	
脚钉			⊖ ⊣			
垫圈	Q235		规格X个数			
合计			6.4 kg			

山东电力工程咨询院有限公司

浙江特高压交流环网工程线路 **工程**				施工图	**设计阶段**
批 准	雷强	**校 核**	习一丹	SZK31102A直线塔 走道结构图	Z4
审 核	高锡鹏				
		设计/勘测	潘兆光		
比 例		**日 期**	2026年 08月	**图 号** 37-SA36901S-T0121-160	**版本**