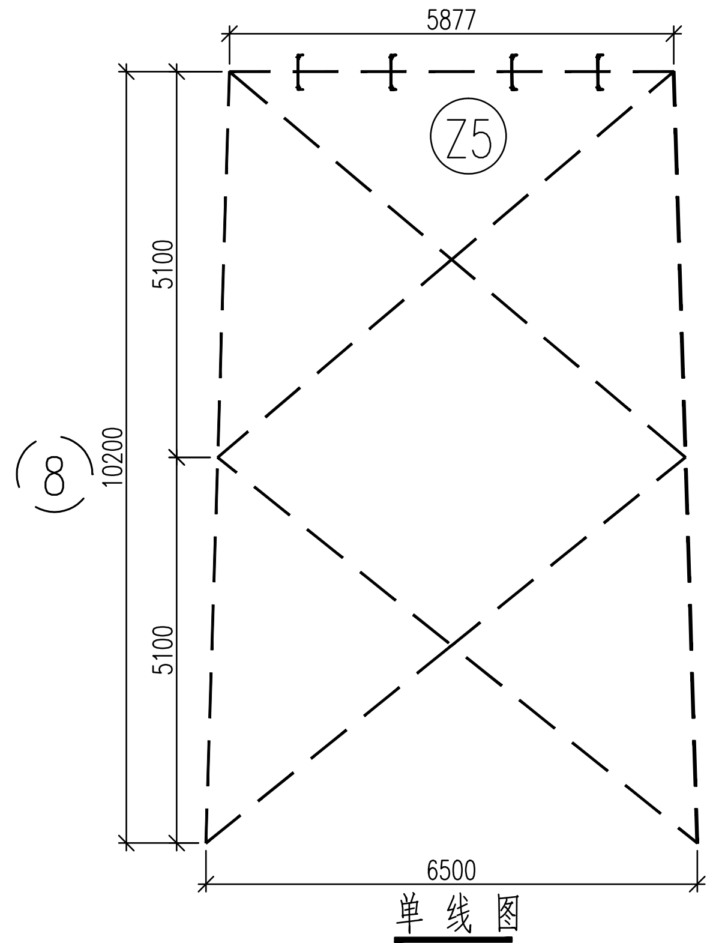
5877
Z5
8
10200
5100
5100
6500

单线图
1:100

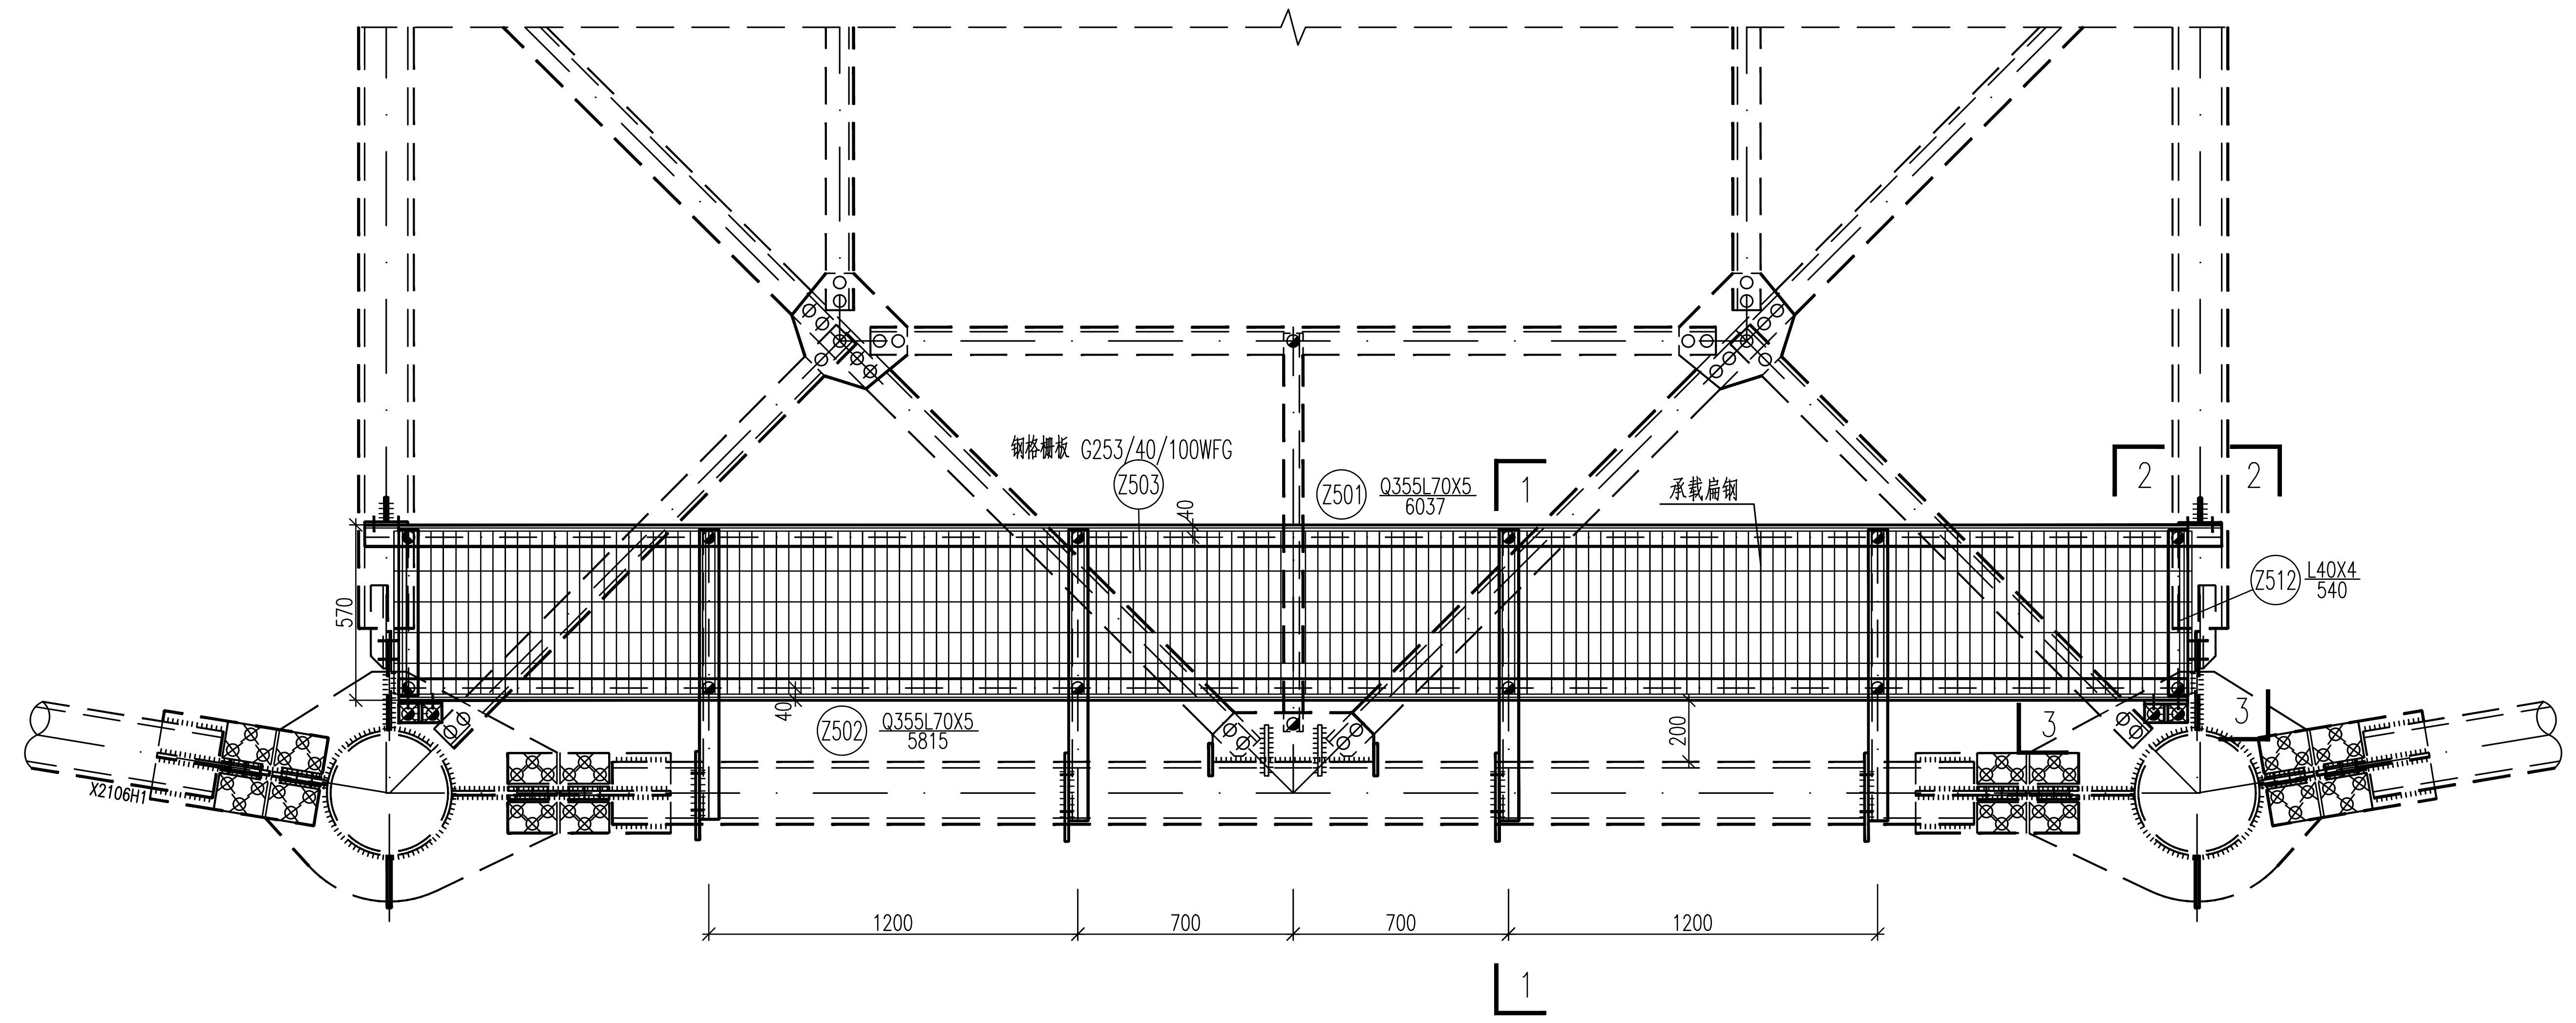
钢格栅板 G253/40/100WFG
Z503
40
Z501
Q355L70X5
6037
1
承载扁钢
2
2
Z512
L40X4
540
570
40
Z502
Q355L70X5
5815
200
3
3
X2106H1
1200
700
700
1200
1

钢格板说明:

1.钢格板按照冶金行业标准(YB/T 4001.1-2019)《钢格栅板及配套件》第一部分:钢格栅板.
2.钢格板用专用的安装夹具固定,每件钢格板安装夹的数量不少于4个且安装夹间距不大于2m,安装夹由加工厂家配套提供.
3.钢格板的承载扁钢须搁置在角钢梁上.
4.走道设置在爬梯侧。

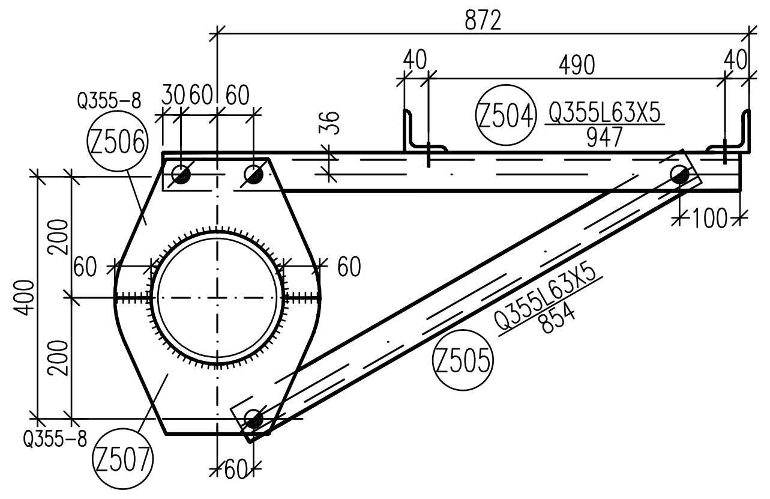
872
40
490
40
Q355-8
30 60 60
Z506
36
Z504
Q355L63X5
947
100
400
200
200
60
60
Q355L63X5
854
Z505
Q355-8
Z507
60

1--1
1:10

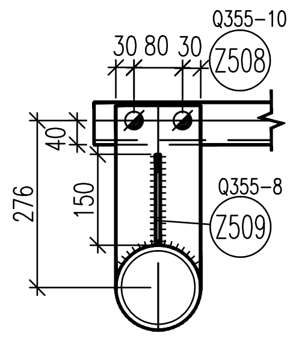
Q355-10
30 80 30
Z508
40
276
150
Q355-8
Z509

2--2
1:10

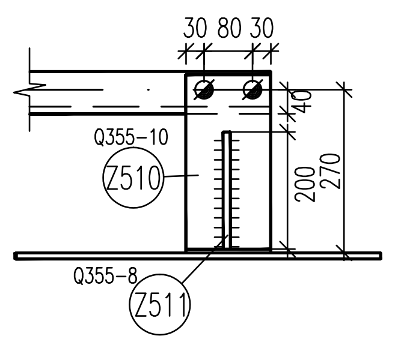
30 80 30
40
Q355-10
Z510
200
270
Q355-8
Z511

3--3
1:10

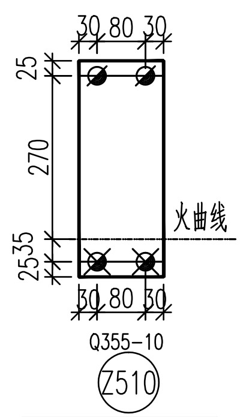
30 80 30
25
270
火曲线
25 35
30 80 30
Q355-10
Z510

1:10

构件明细表

编号	规格	长度(mm)	数量	重量(kg)		备注
				一件	小计	
Z501	Q355L70X5	6037	1	32.58	32.6	
Z502	Q355L70X5	5815	1	31.38	31.4	
Z503	G253/40/100WFG	500X5815	1	72.69	72.7	重量含夹具
Z504	Q355L63X5	947	4	4.57	18.3	
Z505	Q355L63X5	854	4	4.12	16.5	切角
Z506	Q355-8X225	323	4	4.56	18.2	坡口电焊
Z507	Q355-8X225	323	4	4.56	18.2	坡口电焊
Z508	Q355-10X140	302	2	3.32	6.6	坡口电焊
Z509	Q355-8X80	150	2	0.75	1.5	坡口电焊
Z510	Q355-10X140	355	2	3.90	7.8	火曲
Z511	Q355-8X60	200	2	0.75	1.5	坡口电焊
Z512	L40X4	540	2	1.31	2.6	
合计		227.9 kg				

螺栓、脚钉、垫圈明细表

名称	级别	规格	符号	数量	重量(kg)	备注
螺栓	6.8级	M16X45	⊘	16	2.7	
		M16X55	⊘	20	3.7	
		M16X65	⊗	4	0.8	
脚钉			⊖ ⊣			
垫圈	Q235		规格X个数			
合计			7.2 kg			

山东电力工程咨询院有限公司				浙江特高压交流环网工程线路 **工程**	施工图	**设计阶段**
批准	雷强	**校核**	马一丹	SZK31102A直线塔 走道结构图 Z5		
审核	高锡鹏					
		设计/勘测	潘旭光			
比例		**日期**	2026年 08月	**图号** 37-SA36901S-T0121-161	**版本**	