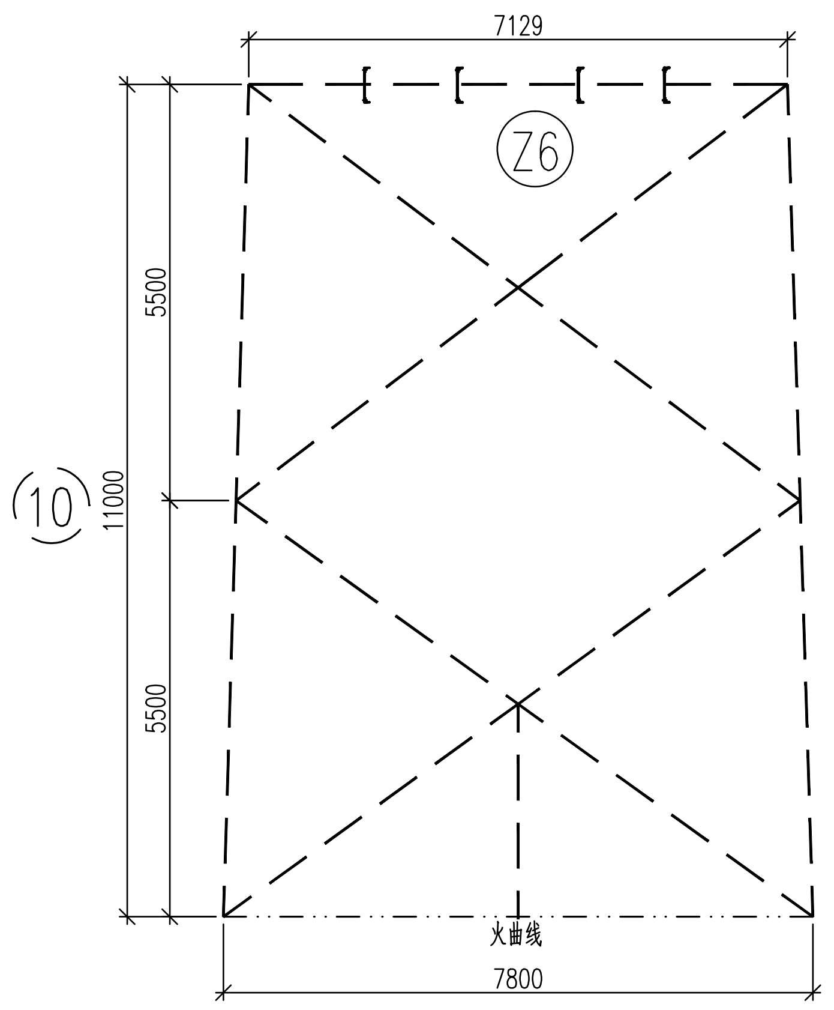

单线图
1:100

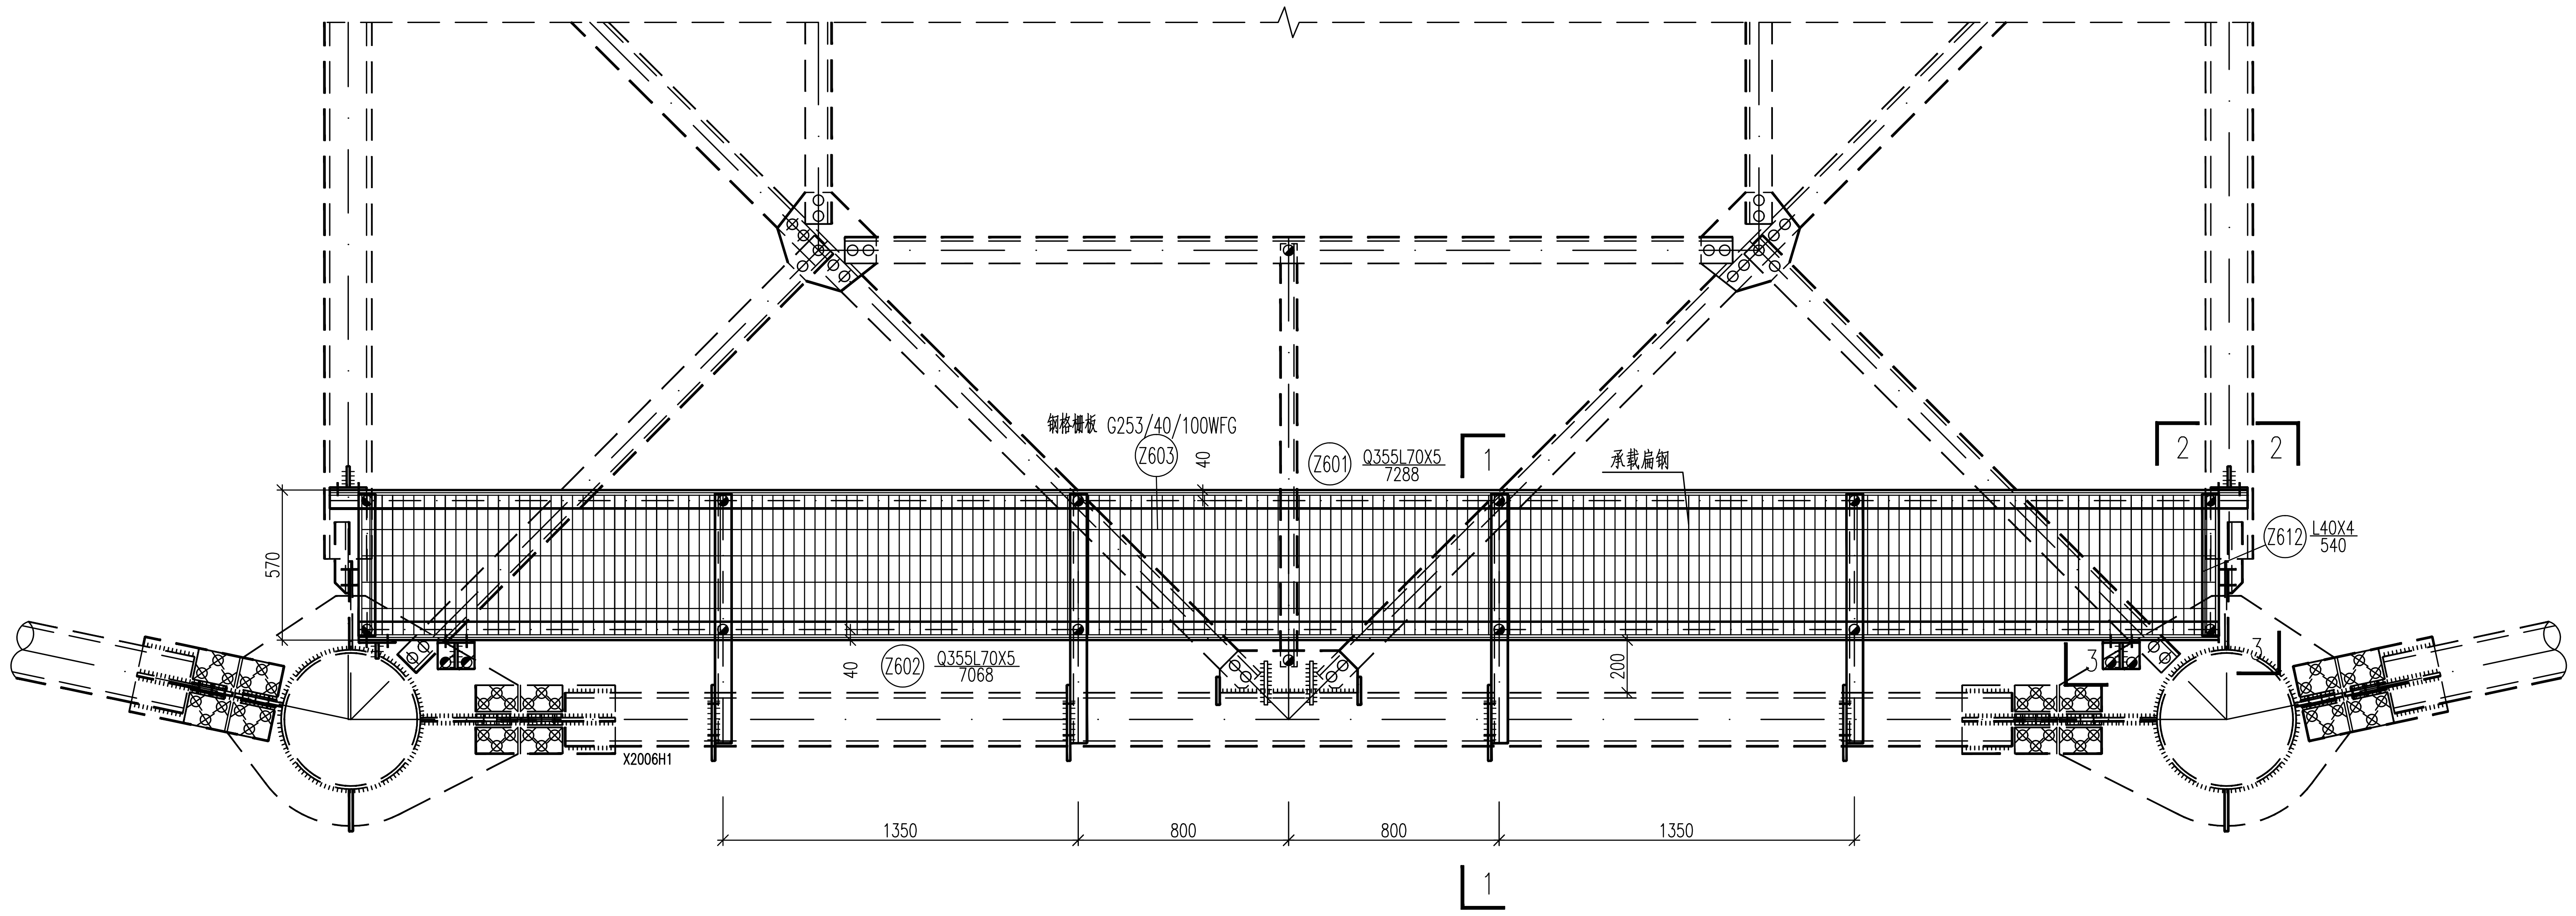

钢格板说明:
1.钢格板按照冶金行业标准(YB/T 4001.1-2007)《钢格栅板及配套件》第一部分:钢格栅板.
2.钢格板用专用的安装夹具固定,每件钢格板安装夹的数量不少于4个且安装夹间距不大于2m,安装夹由加工厂家配套提供.
3.钢格板的承载扁钢须搁置在角钢梁上.
4.走道设置在爬梯侧。

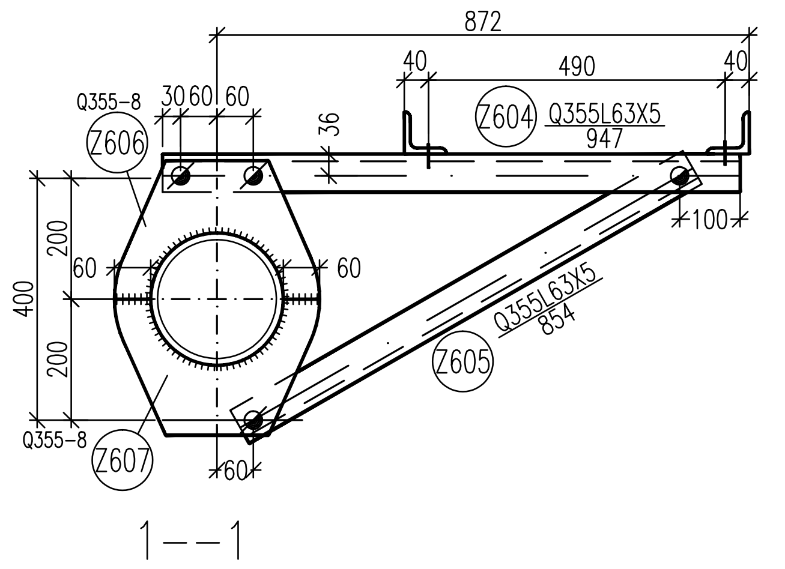

1--1
1:10

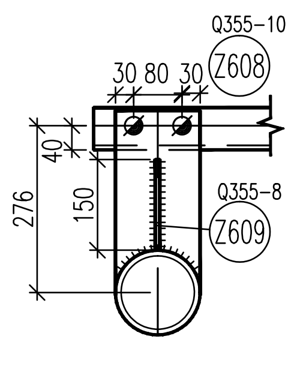

2--2
1:10

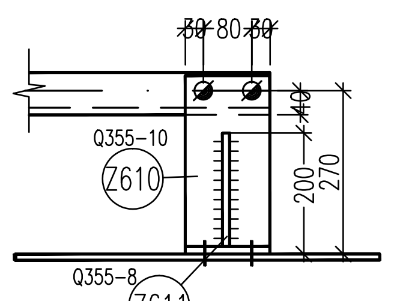

3--3
1:10

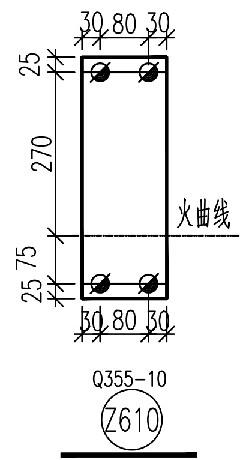

1:10

构 件 明 细 表

编号	规 格	长 度 (mm)	数量	重 量 (kg) 一 件	重 量 (kg) 小 计	备 注
Z601	Q355L70X5	7288	1	39.33	39.3	
Z602	Q355L70X5	7068	1	38.15	38.2	
Z603	G253/40/100WFG	500X7068	1	88.35	88.3	重量含夹具
Z604	Q355L63X5	947	4	4.57	18.3	
Z605	Q355L63X5	854	4	4.12	16.5	切角
Z606	Q355-8X225	323	4	4.56	18.2	坡口电焊
Z607	Q355-8X225	323	4	4.56	18.2	坡口电焊
Z608	Q355-10X140	300	2	3.30	6.6	坡口电焊
Z609	Q355-8X80	150	2	0.75	1.5	坡口电焊
Z610	Q355-10X140	395	2	4.34	8.7	坡口电焊 火曲
Z611	Q355-8X100	200	2	1.26	2.5	坡口电焊
Z612	L40X4	540	2	1.31	2.6	
合 计		258.9 kg				

螺栓、脚钉、垫圈明细表

名称	级别	规 格	符 号	数量	重量(kg)	备 注
螺栓	6.8级	M16X45	⊘	16	2.7	
		M16X55	⊘	24	4.4	
脚钉			⊖			
			⊣			
垫圈	Q235		规格X个数			
合 计			7.1 kg			

山东电力工程咨询院有限公司				浙江特高压交流环网工程线路 工程	施工图	设计阶段
批 准	雷强	校 核	马一丹	SZK31102A直线塔 走道结构图 Z6		
审 核	高锡鹏					
		设计/勘测	潘兆光			
比 例		日 期	2026年 08月	图 号	37-SA36901S-T0121-162	版本