各呼高（含减退）防坠落装置总长统计表

呼高(m)	90.0m		呼高(m)	93.0m		呼高(m)	96.0m		呼高(m)	99.0m	
本体段号	①～⑰㉓		本体段号	①～⑰㉓		本体段号	①～⑰㉓		本体段号	①～⑲㉔	
接腿	段号	刚性导轨长(m)	接腿	段号	刚性导轨长(m)	接腿	段号	刚性导轨长(m)	接腿	段号	刚性导轨长(m)
−4.5m	㉗X4	141.7	−4.5m	㉙X4	144.7	−4.5m	㉛X4	147.7	−4.5m	㉟X4	150.7
−3.0m	㉘X4	143.2	−3.0m	㉚X4	146.2	−3.0m	㉜X4	149.2	−3.0m	㊱X4	152.2
−1.5m	㉙X4	144.7	−1.5m	㉛X4	147.7	−1.5m	㉝X4	150.7	−1.5m	㊲X4	153.7
−0.0m	㉚X4	146.2	−0.0m	㉜X4	149.2	−0.0m	㉞X4	152.2	−0.0m	㊳X4	155.2

呼高(m)	102.0m		呼高(m)	105.0m		呼高(m)	108.0m		呼高(m)	111.0m	
本体段号	①～⑲㉔		本体段号	①～⑲㉔		本体段号	①～⑲㉕		本体段号	①～⑲㉕	
接腿	段号	刚性导轨长(m)	接腿	段号	刚性导轨长(m)	接腿	段号	刚性导轨长(m)	接腿	段号	刚性导轨长(m)
−4.5m	㊲X4	153.7	−4.5m	㊴X4	156.7	−4.5m	㊸X4	159.7	−4.5m	㊺X4	162.7
−3.0m	㊳X4	155.2	−3.0m	㊵X4	158.2	−3.0m	㊹X4	161.2	−3.0m	㊻X4	164.2
−1.5m	㊴X4	156.7	−1.5m	㊶X4	159.7	−1.5m	㊺X4	162.7	−1.5m	㊼X4	165.7
−0.0m	㊵X4	158.2	−0.0m	㊷X4	161.2	−0.0m	㊻X4	164.2	−0.0m	㊽X4	167.2

呼高(m)	114.0m		呼高(m)	117.0m		呼高(m)	120.0m		呼高(m)	123.0m	
本体段号	①～⑲㉕		本体段号	①～⑲㉕		本体段号	①～㉑㉖		本体段号	①～㉑㉖	
接腿	段号	刚性导轨长(m)	接腿	段号	刚性导轨长(m)	接腿	段号	刚性导轨长(m)	接腿	段号	刚性导轨长(m)
−4.5m	㊼X4	165.7	−4.5m	㊾X4	168.7	−4.5m	(53)X4	171.7	−4.5m	(55)X4	174.7
−3.0m	㊽X4	167.2	−3.0m	㊿X4	170.2	−3.0m	(54)X4	173.2	−3.0m	(56)X4	176.2
−1.5m	㊾X4	168.7	−1.5m	(51)X4	171.7	−1.5m	(55)X4	174.7	−1.5m	(57)X4	177.7
−0.0m	㊿X4	170.2	−0.0m	(52)X4	173.2	−0.0m	(56)X4	176.2	−0.0m	(58)X4	179.2

呼高(m)	126.0m		呼高(m)	129.0m		呼高(m)	132.0m		呼高(m)	135.0m	
本体段号	①～㉑㉖		本体段号	①～㉑㉖		本体段号	①～㉒		本体段号	①～㉒	
接腿	段号	刚性导轨长(m)	接腿	段号	刚性导轨长(m)	接腿	段号	刚性导轨长(m)	接腿	段号	刚性导轨长(m)
−4.5m	(57)X4	177.7	−4.5m	(59)X4	180.7	−4.5m	(63)X4	183.7	−4.5m	(65)X4	186.7
−3.0m	(58)X4	179.2	−3.0m	(60)X4	182.2	−3.0m	(64)X4	185.2	−3.0m	(66)X4	188.2
−1.5m	(59)X4	180.7	−1.5m	(61)X4	183.7	−1.5m	(65)X4	186.7	−1.5m	(67)X4	189.7
−0.0m	(60)X4	182.2	−0.0m	(62)X4	185.2	−0.0m	(66)X4	188.2	−0.0m	(68)X4	191.2

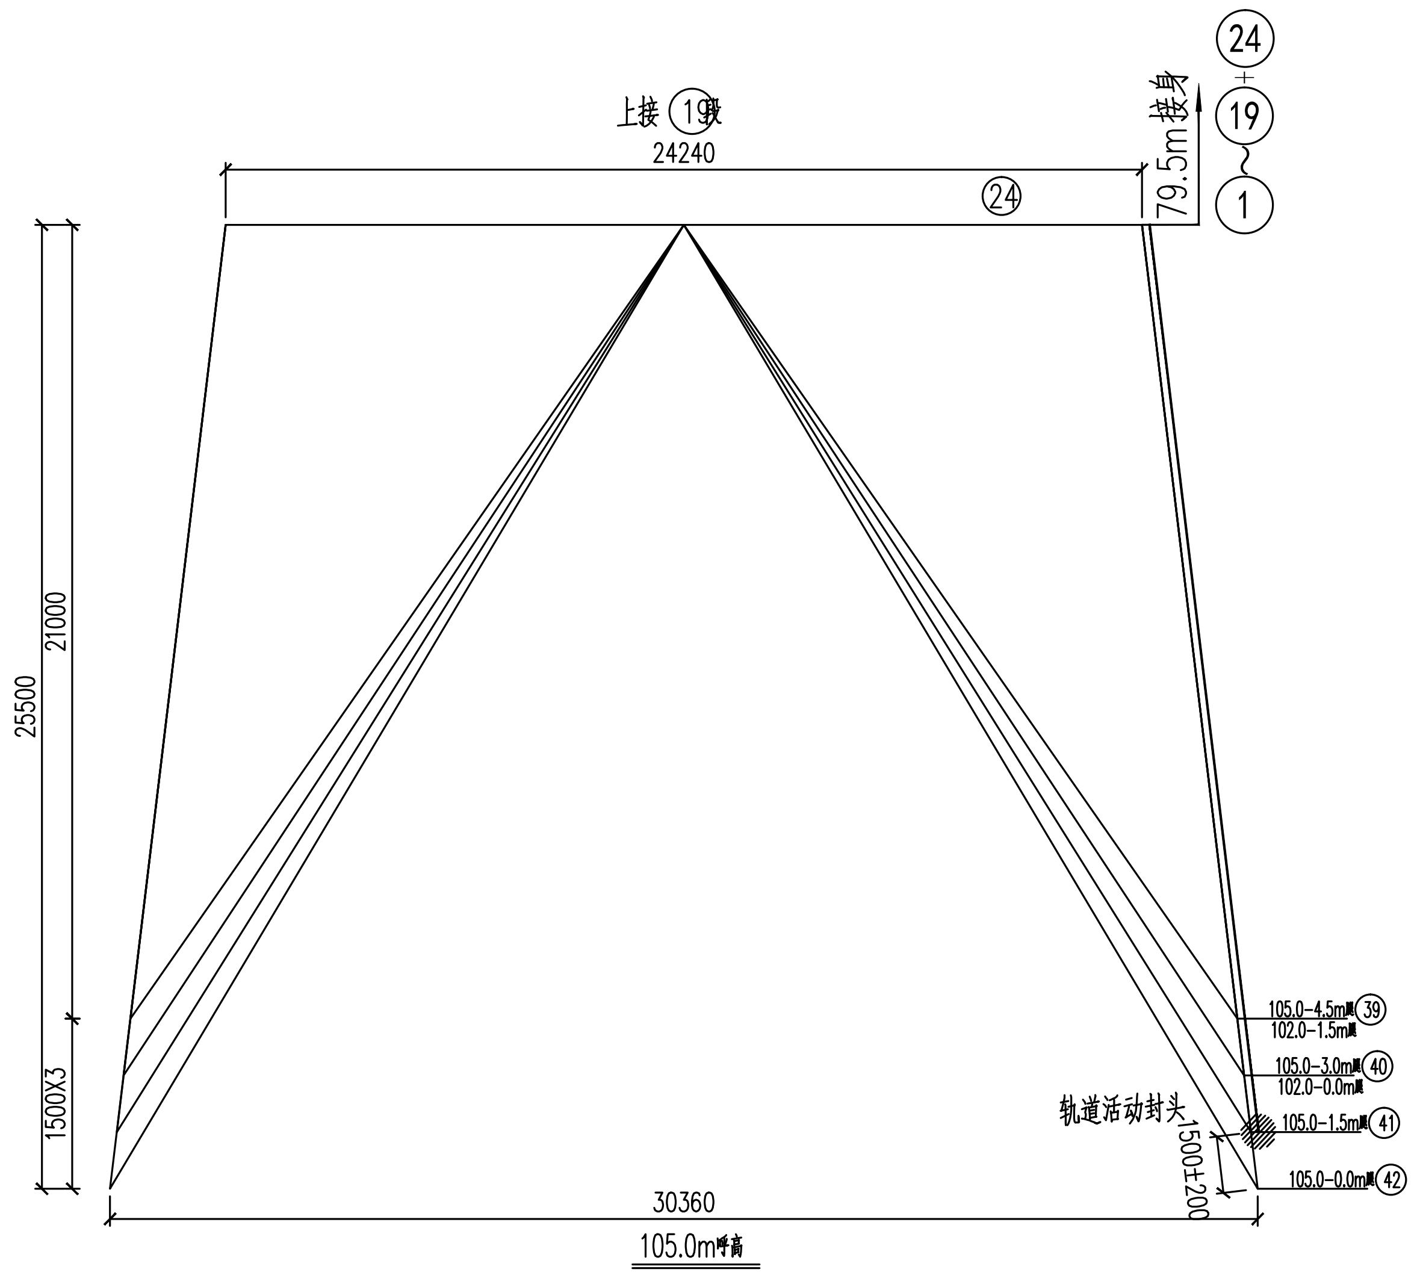

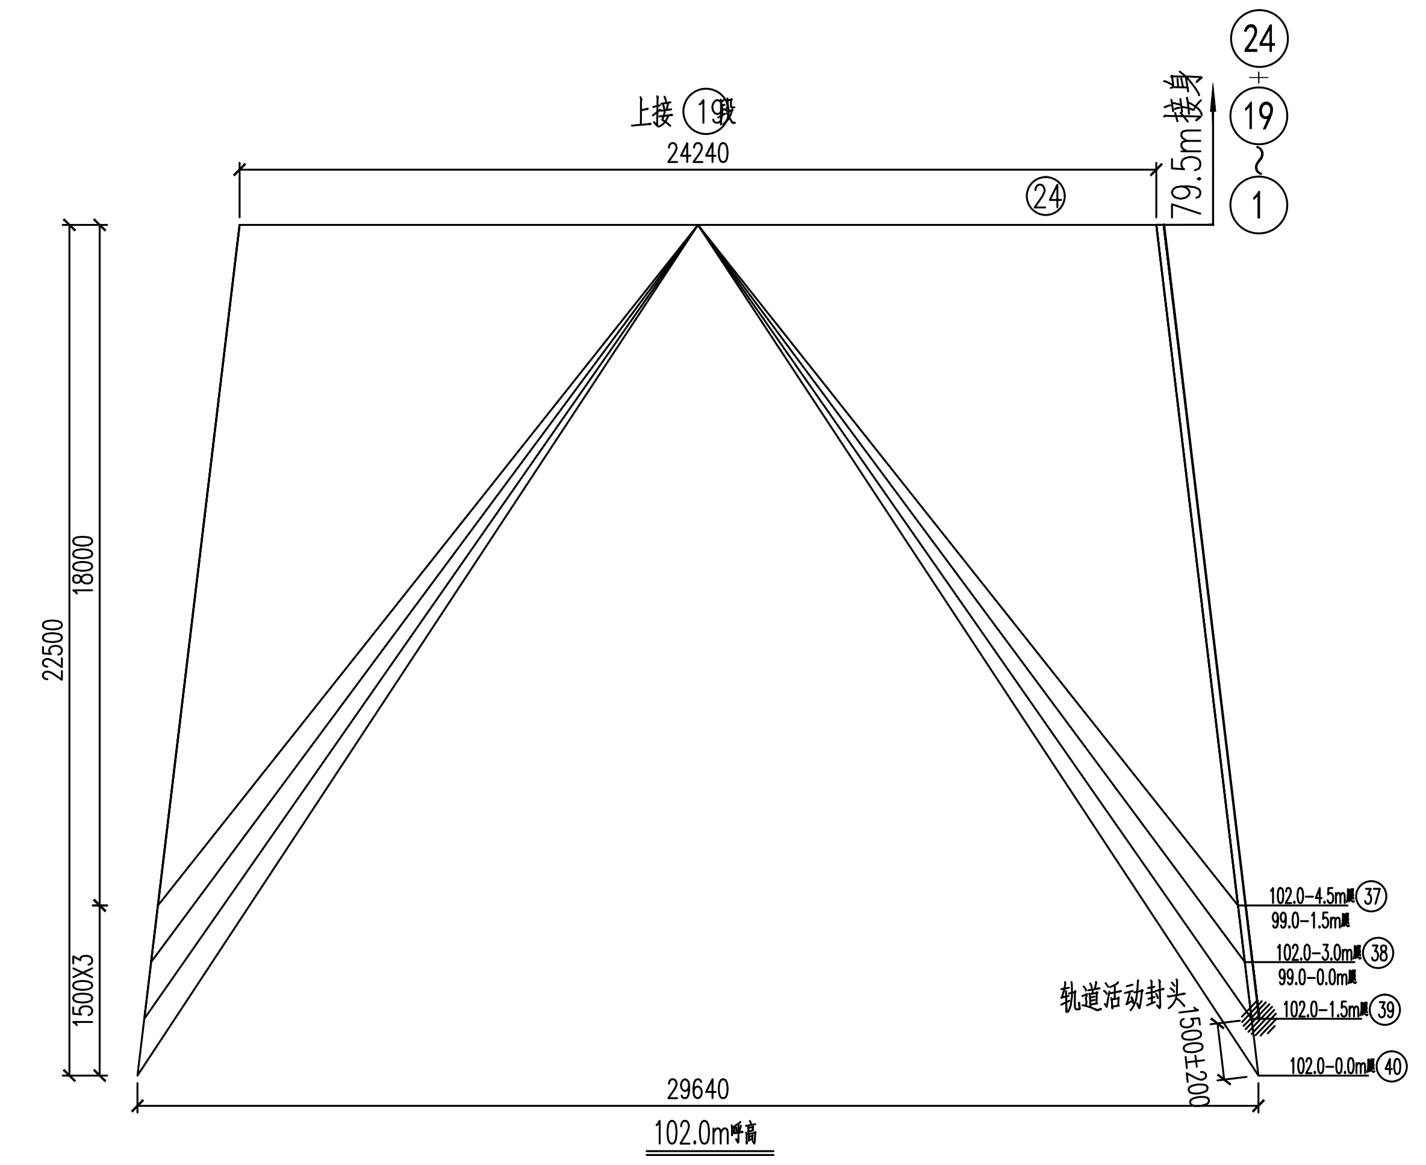

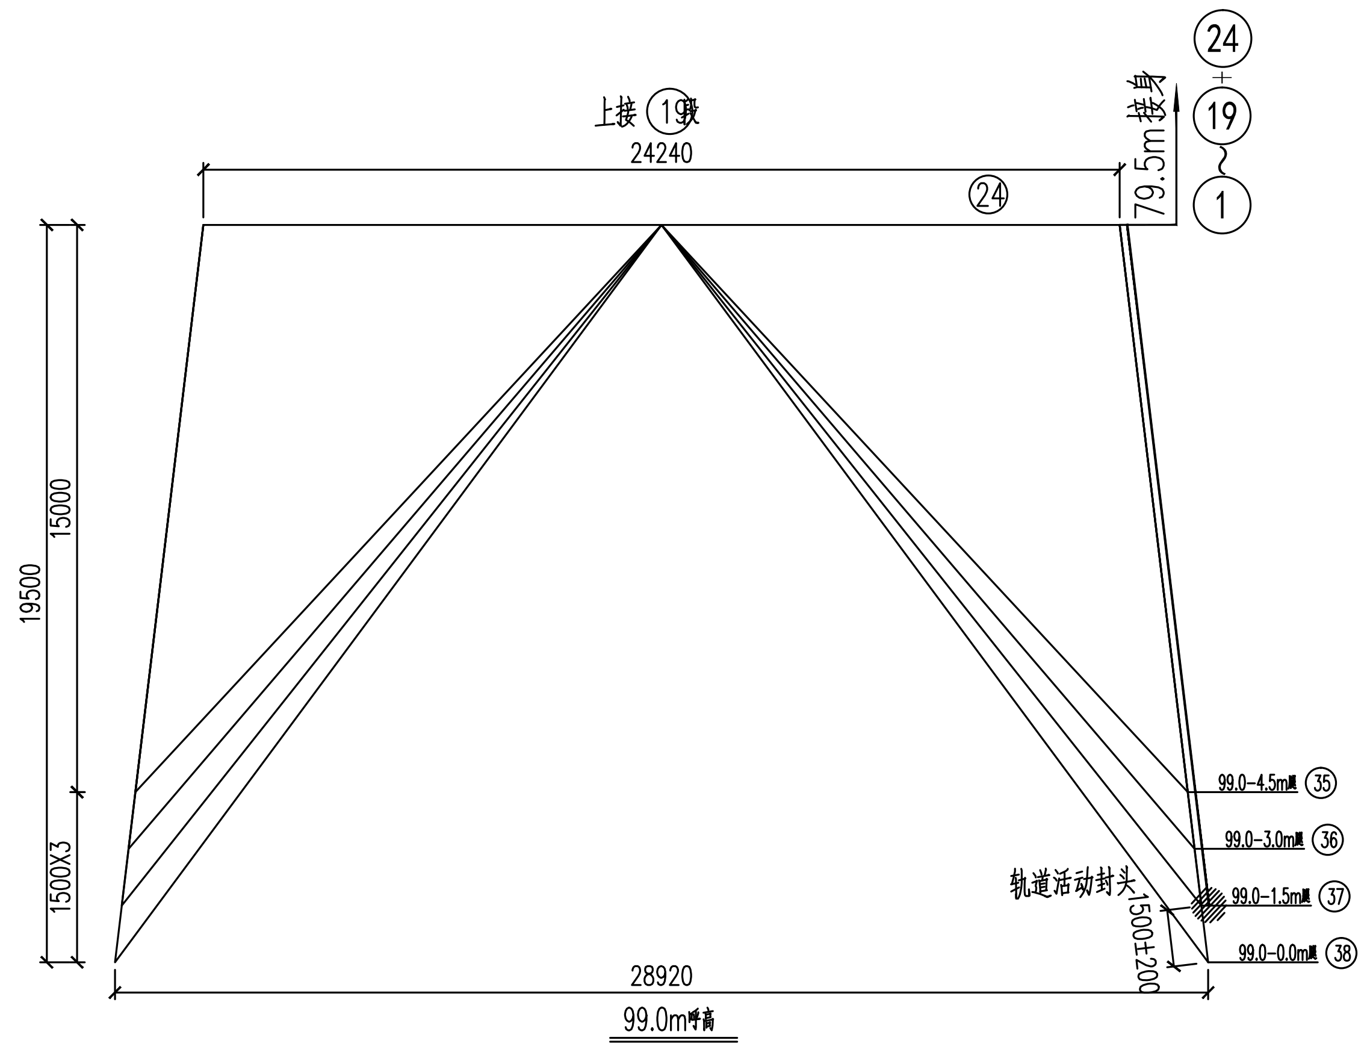

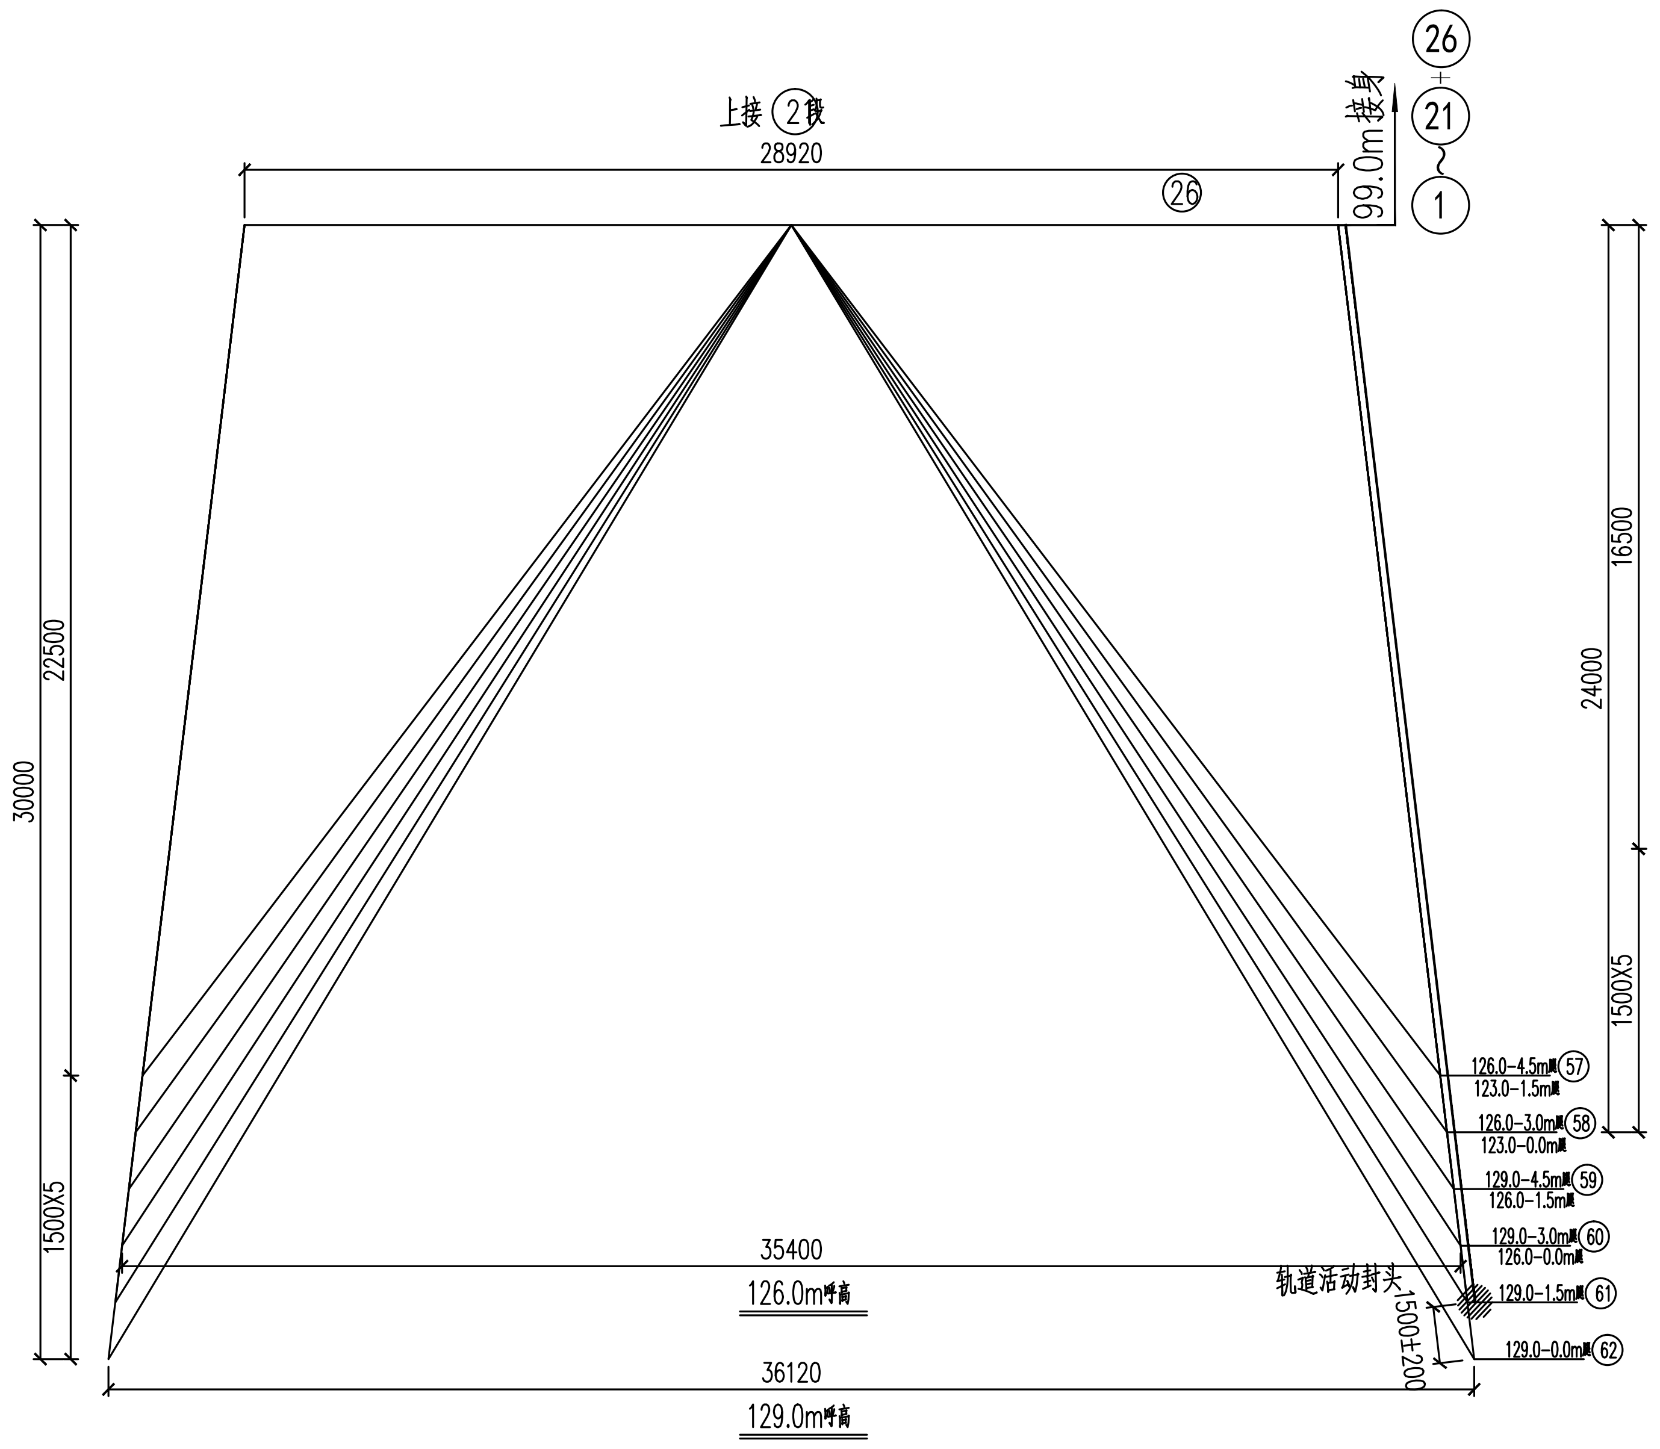

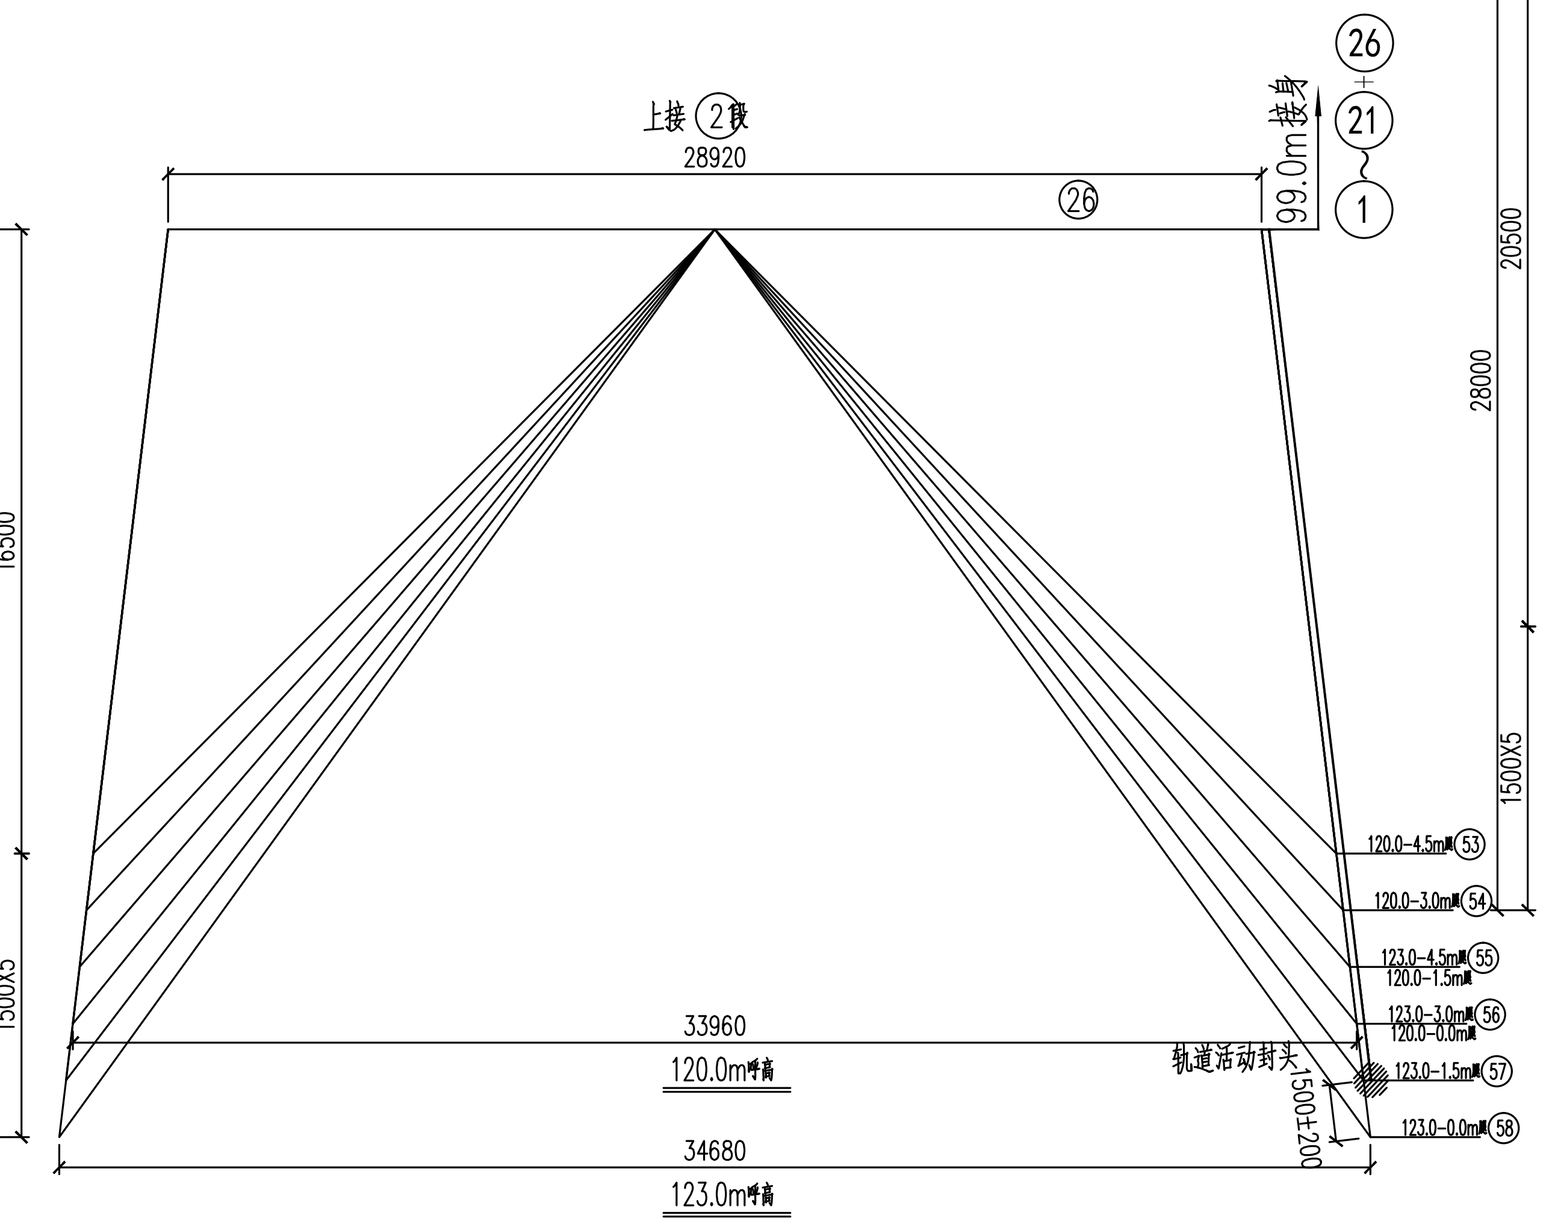

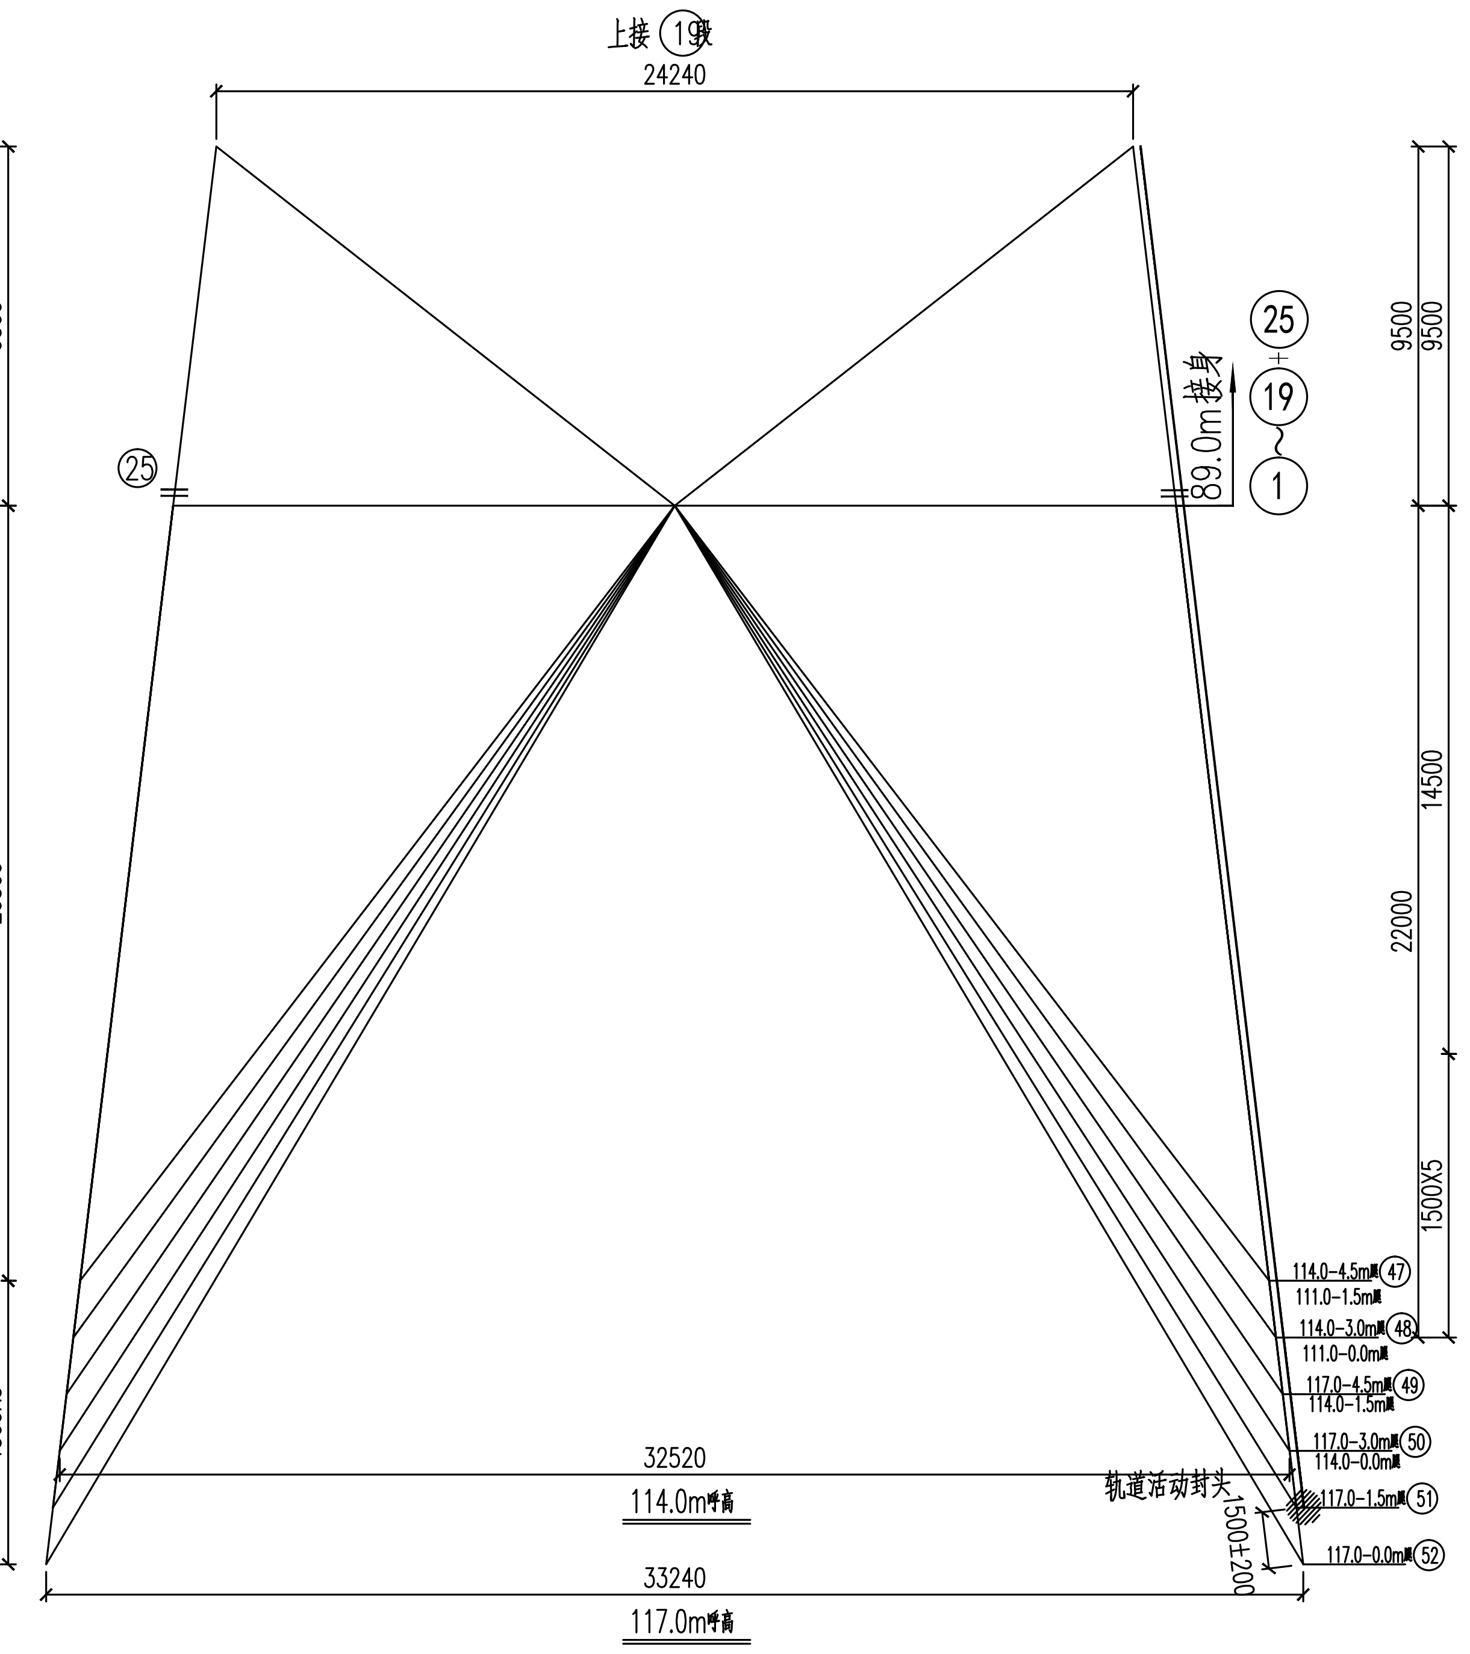

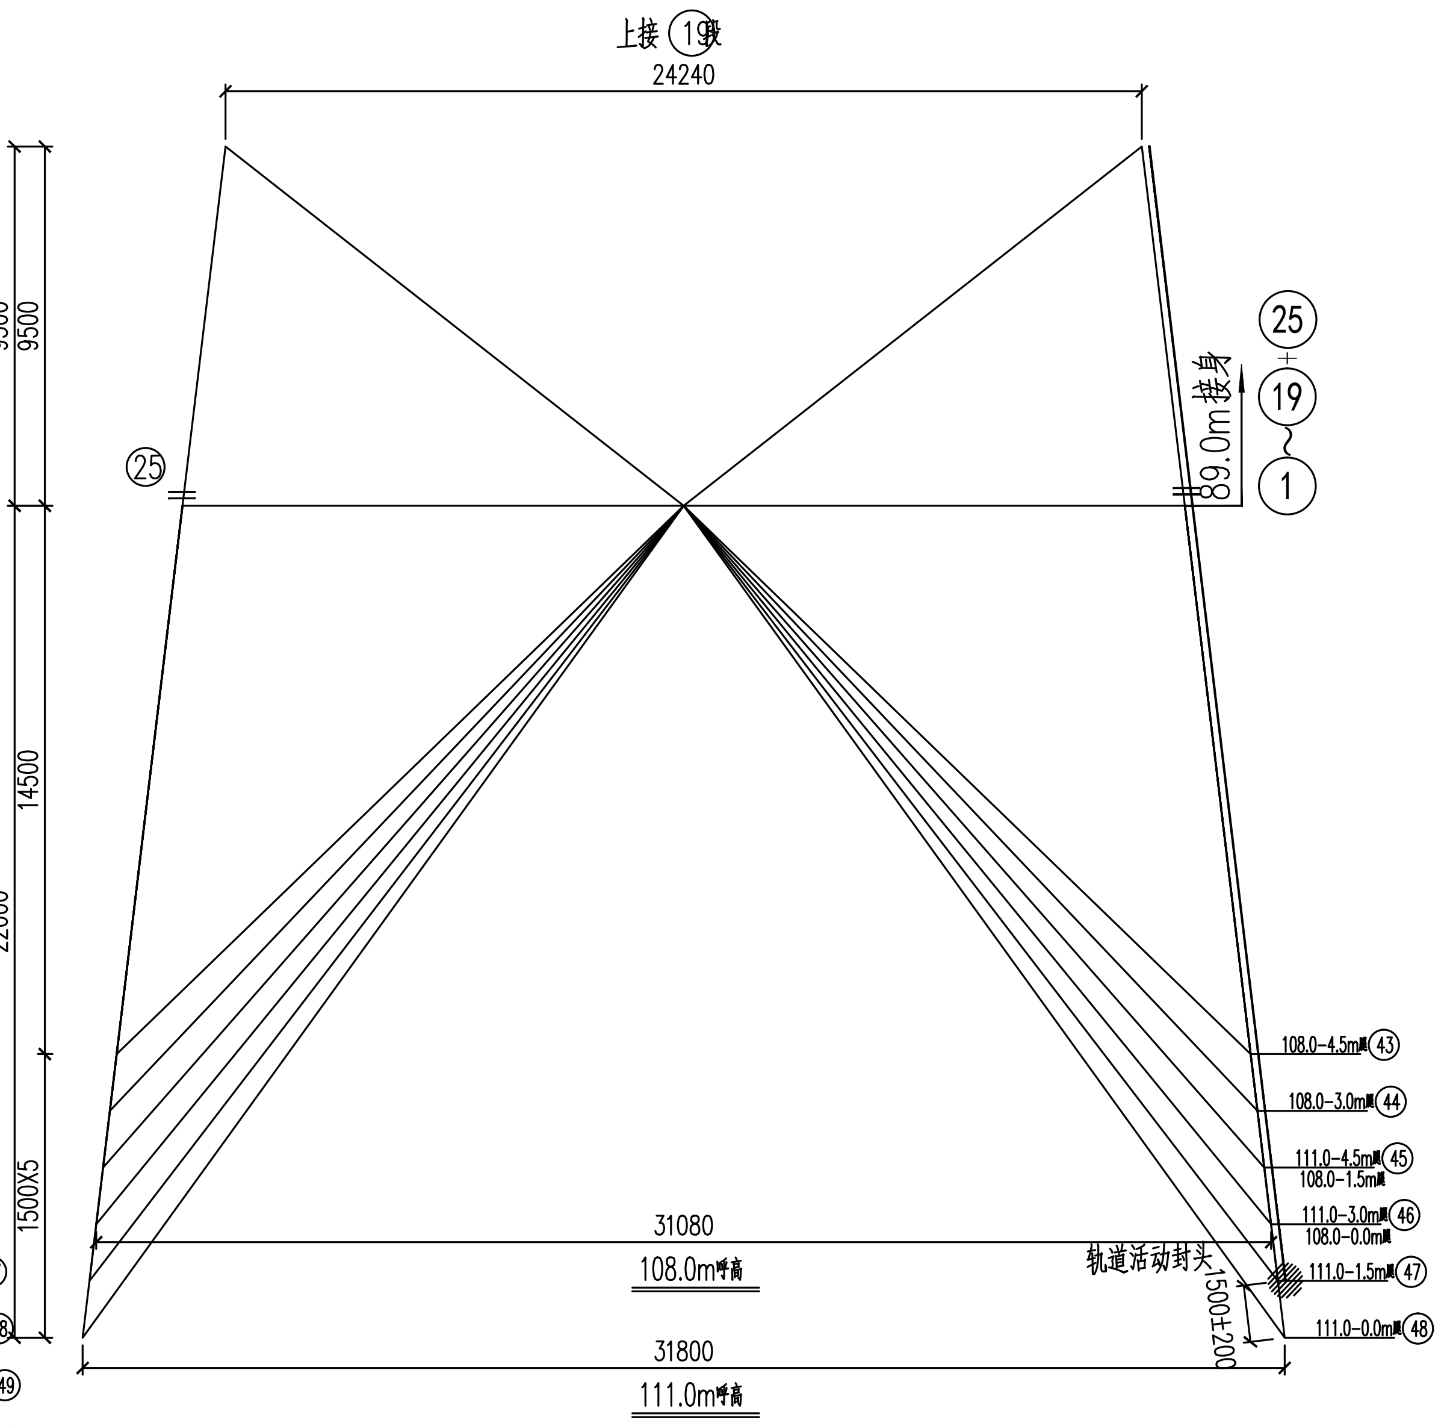

本 院 图 号		山东电力工程咨询院有限公司				浙江特高压交流环网工程线路 工程	施工图	设计阶段
		批 准		校 核	马一丹	SZK31102A双回路直线塔 防坠落装置布置图(2/2)		
		审 核	高锡鹏	设计/勘测				
		比 例	1:200	日 期	2026年 08月	图 号	37-SA36901S-T0121-164	版本